
CASA ÁNGEL · PISOS Y ZÓCALOS · FICHA TP-11 · ESCALONES 20CM

TP-11 · Escalones 20cm · hormigón · 2,57 m²


TP-11 · planta (00. Planta Baja) 1:15

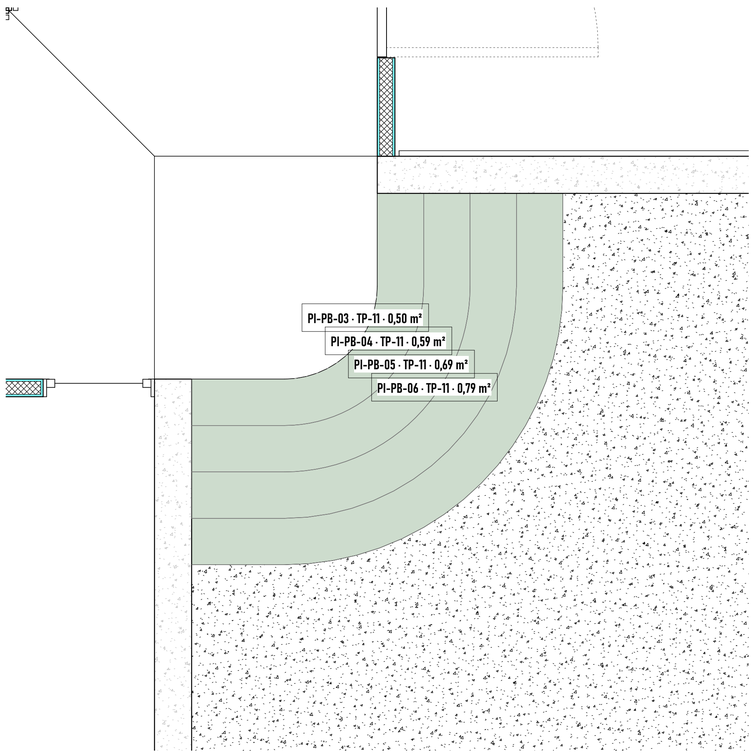

TP-11 · corte de paquete 1:5



TP-11 · axonométrica 1:15

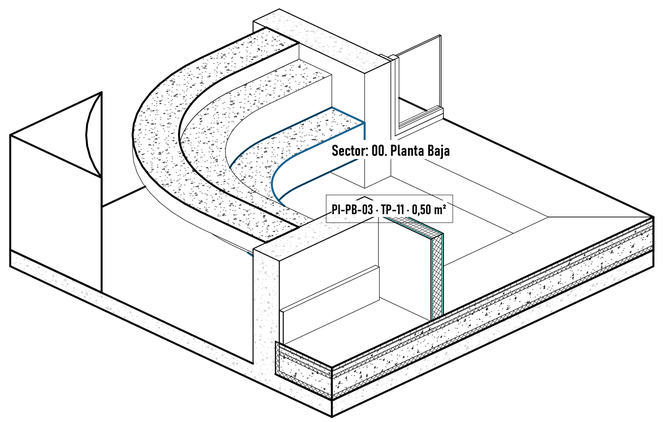

TP-11 · Escalones 20cm · hormigón · 2,57 m²
Paquete: hormigón 20 cm · total 20,00 cm
Locales: sin local asociado
Piezas: PI-PB-03, PI-PB-04, PI-PB-05, PI-PB-06

Pisos: paquetes según tipo de piso del modelo; terminación = capa superior. Cotas en metros (no asociativas). Códigos TP/PI/ZO como anotación. Zócalos: solo 5 tramos modelados; el resto se computa por perímetro de local.

https://ezeader.myportfolio.com/ezequiel-ader

Consultant Address Address Phone Fax e-mail	Consultant Address Address Phone Fax e-mail
Consultant Address Address Phone Fax e-mail	Consultant Address Address Phone Fax e-mail

No.	Description	Date

Angel Luis Brusca

CASA ANGEL

PIS-F-TP-11

Project number	0001
Date	18 de Agosto, 2025
Drawn by	Author
Checked by	Checker

Pisos · TP-11

Scale: As indicated

10/23/2026 7:35:28 PM