
CASA ÁNGEL · PISOS Y ZÓCALOS · PLANTA DE PISOS · 01. PLANTA ALTA

Planta de pisos · 01. Planta Alta 1:60

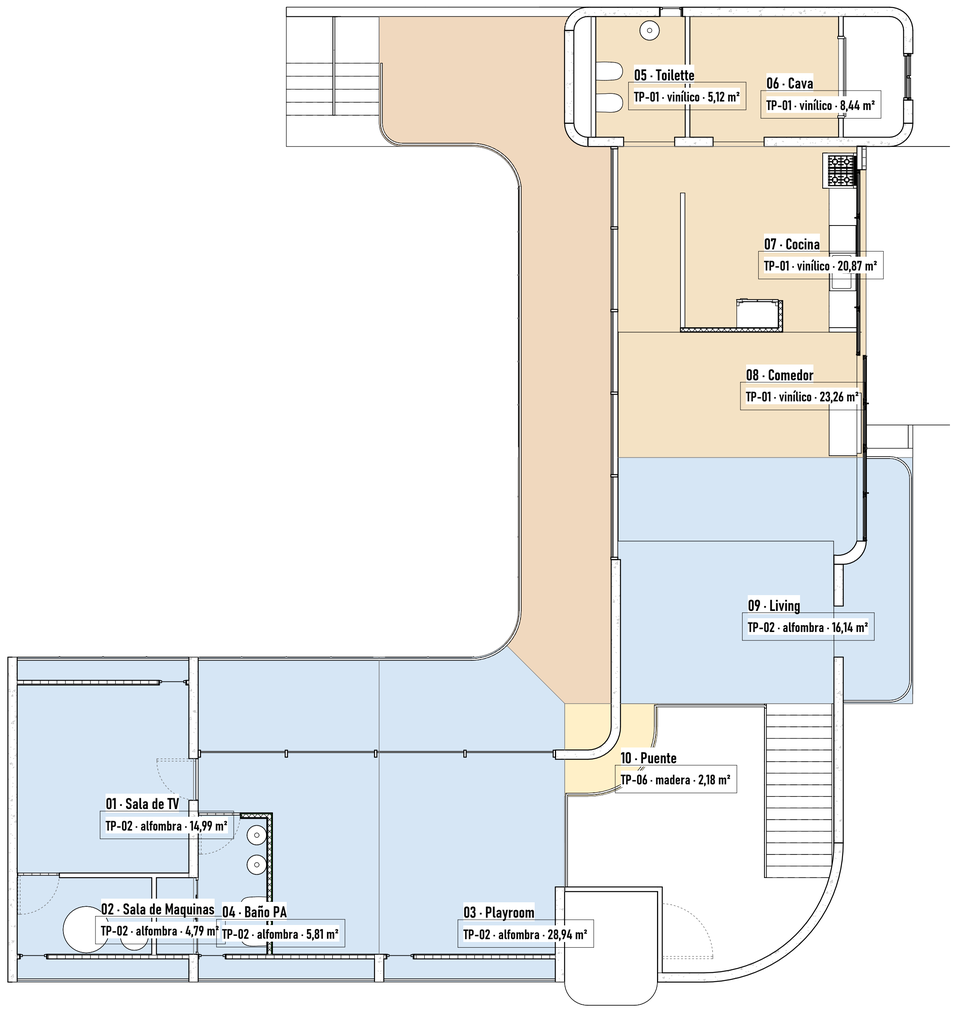

258,97 m² de pisos · TP-01 65,35 m² · TP-02 127,56 m² · TP-06 3,52 m² · TP-09 11,20 m² · TP-10 51,34 m²

Pisos: paquetes según tipo de piso del modelo; terminación = capa superior. Cotas en metros (no asociativas). Códigos TP/PI/ZO como anotación. Zócalos: solo 5 tramos modelados; el resto se computa por perímetro de local.

https://ezeader.myportfolio.com/ezequiel-ader

Consultant
Address
Address
Phone
Fax
e-mail

Consultant
Address
Address
Phone
Fax
e-mail

Consultant
Address
Address
Phone
Fax
e-mail

Consultant
Address
Address
Phone
Fax
e-mail

No.	Description	Date

Angel Luis Brusca

CASA ANGEL

PIS-PA-01

Project number	0001
Date	18 de Agosto, 2025
Drawn by	Author
Checked by	Checker

Pisos · PA

Scale 1 : 60

10/23/2026 7:35:09 PM