
CASA ÁNGEL · PISOS Y ZÓCALOS · PLANTA DE PISOS · 00. PLANTA BAJA

Planta de pisos · 00. Planta Baja 1:75

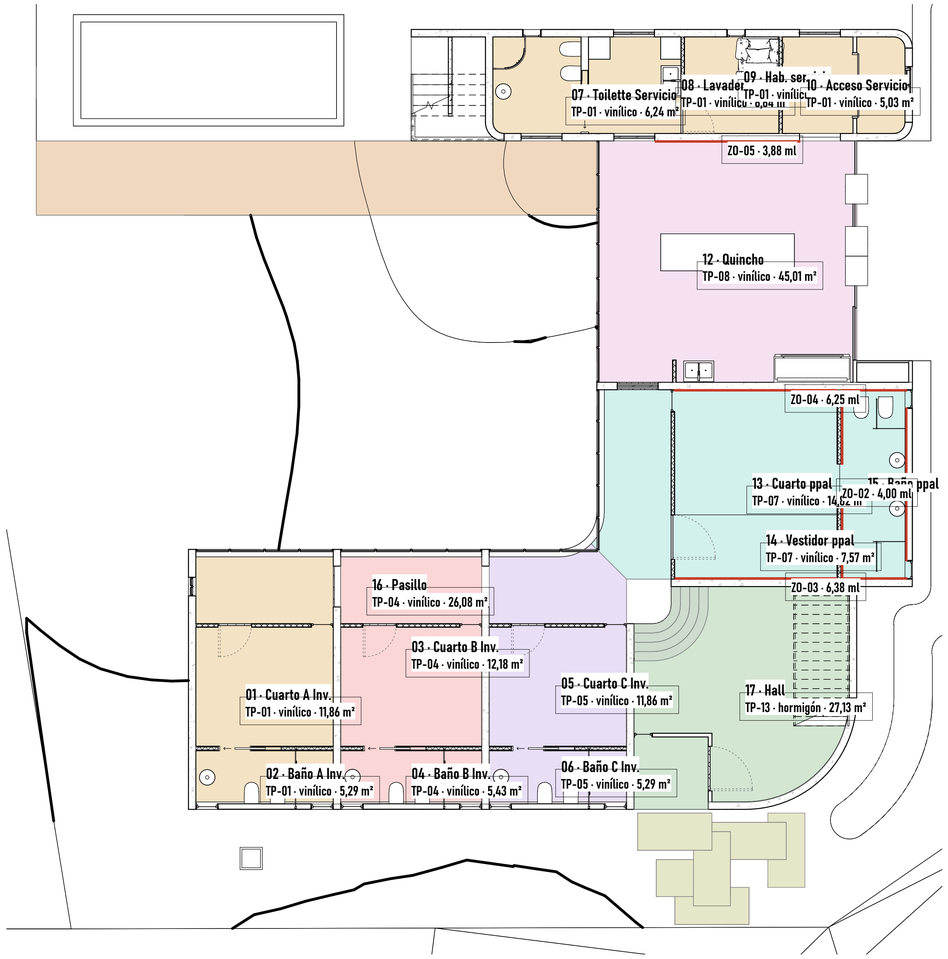

264,11 m² de pisos · TP-01 53,22 m² · TP-04 25,08 m² · TP-05 24,39 m² · TP-07 42,30 m² · TP-08 45,50 m² · TP-10 30,20 m² · TP-11 2,57 m² · TP-12 12,00 m² · TP-13 28,84 m²

Pisos: paquetes según tipo de piso del modelo; terminación = capa superior. Cotas en metros (no asociativas). Códigos TP/PI/ZO como anotación. Zócalos: solo 5 tramos modelados; el resto se computa por perímetro de local.

https://ezeader.myportfolio.com/ezequiel-ader

Consultant
Address
Address
Phone
Fax
e-mail

Consultant
Address
Address
Phone
Fax
e-mail

Consultant
Address
Address
Phone
Fax
e-mail

Consultant
Address
Address
Phone
Fax
e-mail

No.	Description	Date

Angel Luis Brusca

CASA ANGEL

PIS-PB-01

Project number	0001
Date	18 de Agosto, 2025
Drawn by	Author
Checked by	Checker

Pisos · PB

Scale 1 : 75

10/23/2026 7:35:07 PM