CASA ÁNGEL · ALBAÑILERÍA · MUROS M-PE-09 A M-PE-12 · VISTA Y CORTE

02. Planta Entrepiso · 4 muros · alzado con vanos y medidas + corte con capas 1:10

M-PE-09 · vista · H° (Estructura) 1:75

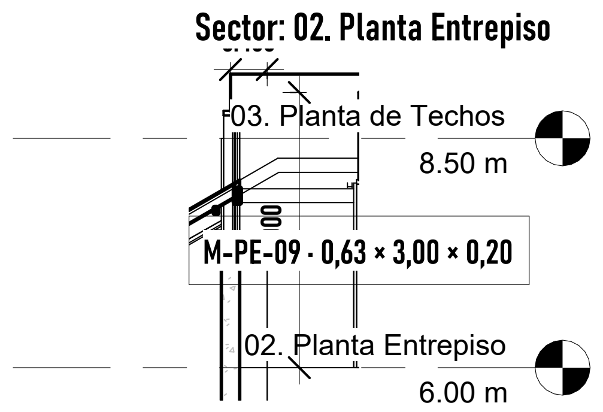
Sector: 02. Planta Entrepiso
03. Planta de Techos
8.50 m
M-PE-09 · 0,63 × 3,00 × 0,20
02. Planta Entrepiso
6.00 m

M-PE-10 · vista · H° (Estructura) 1:50

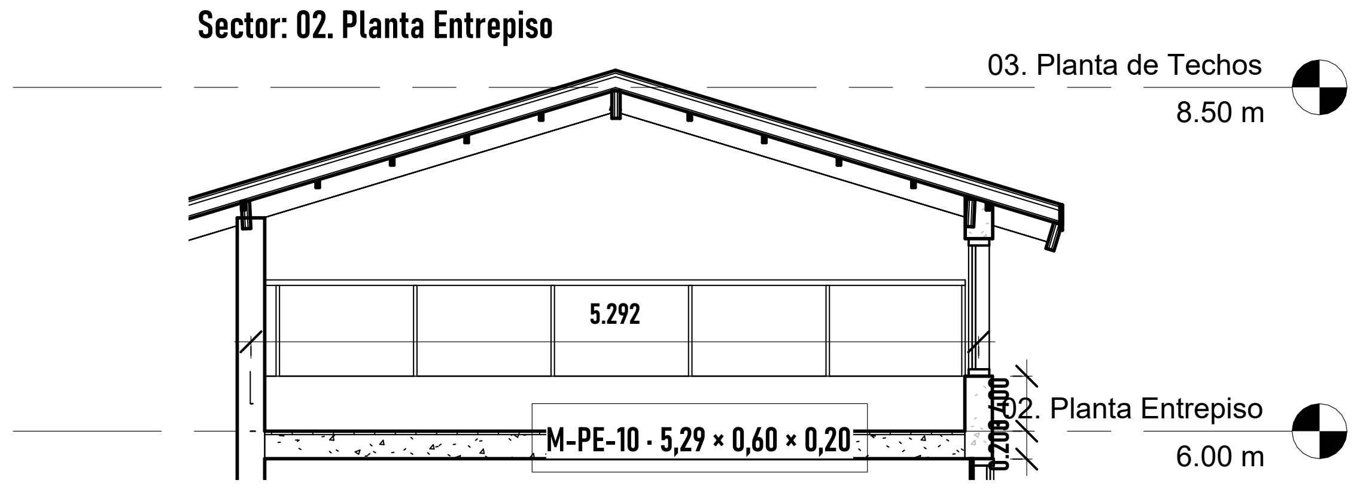
Sector: 02. Planta Entrepiso
03. Planta de Techos
8.50 m
5.292
M-PE-10 · 5,29 × 0,60 × 0,20
02. Planta Entrepiso
6.00 m

M-PE-11 · vista · H° (Estructura) 1:50

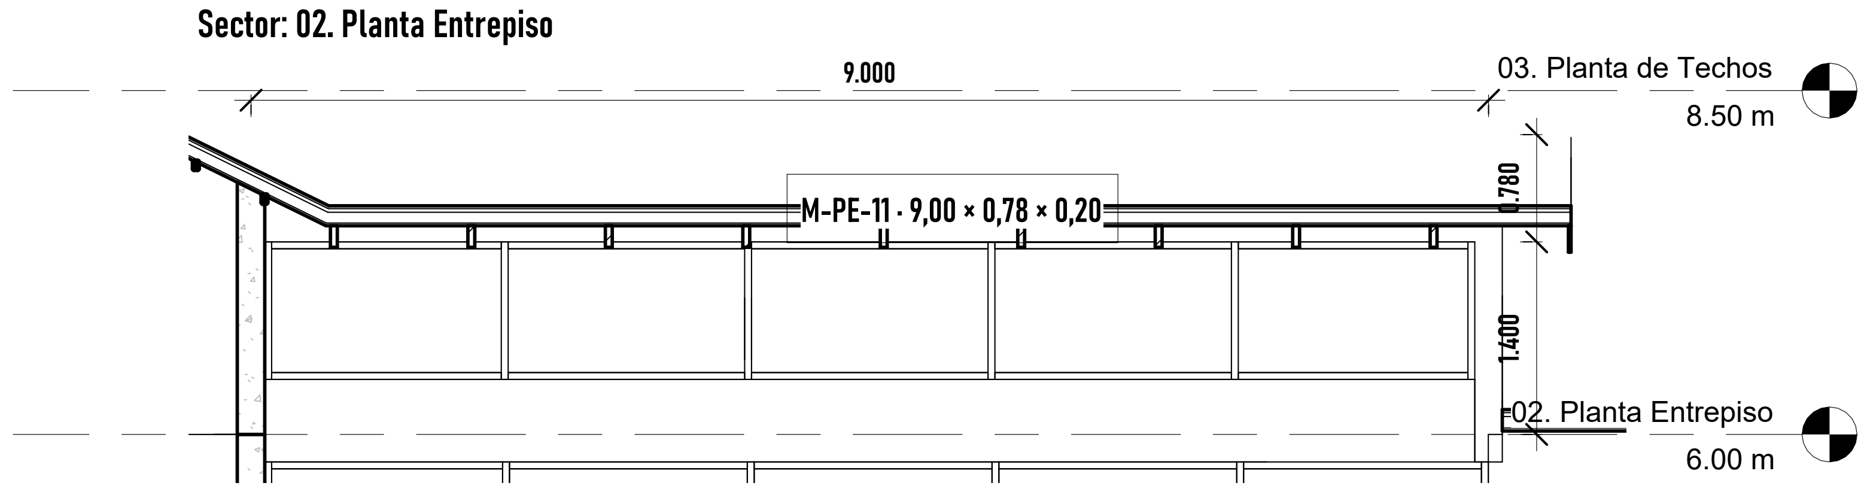
Sector: 02. Planta Entrepiso
9.000
03. Planta de Techos
8.50 m
M-PE-11 · 9,00 × 0,78 × 0,20
0.780
1.400
02. Planta Entrepiso
6.00 m

M-PE-12 · vista · H° (Estructura) 1:50

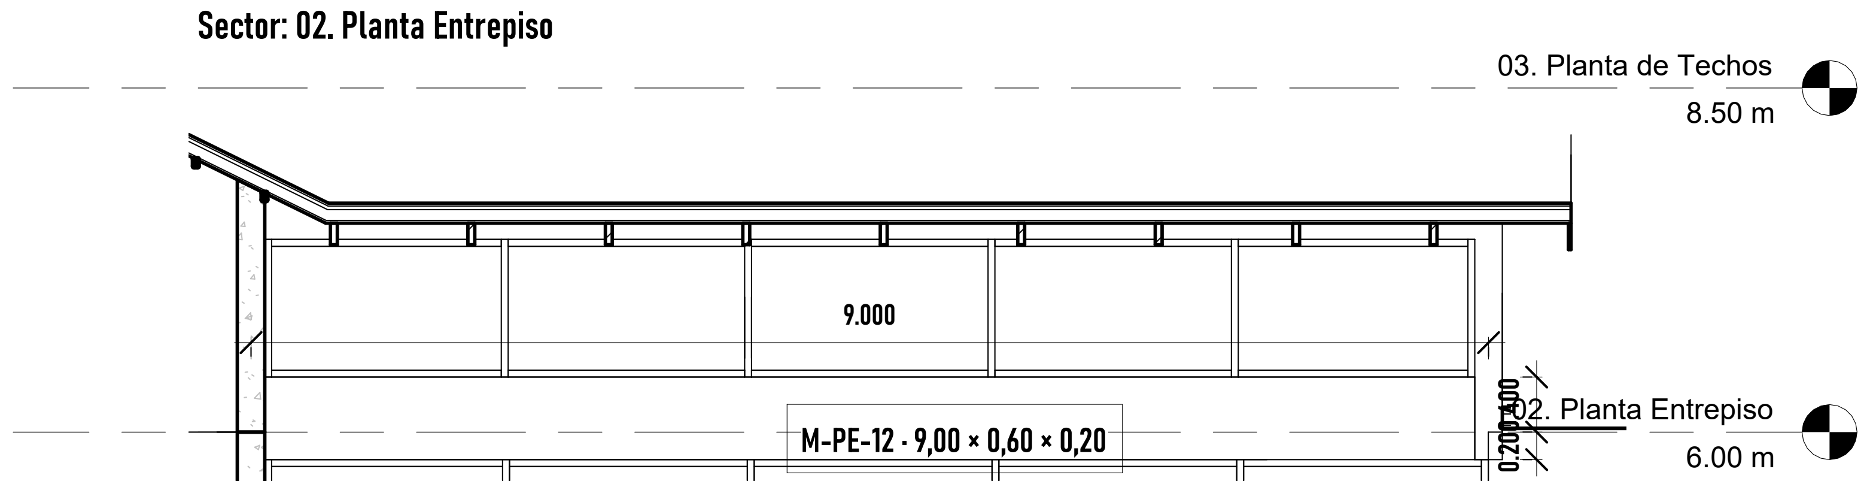
Sector: 02. Planta Entrepiso
03. Planta de Techos
8.50 m
9.000
M-PE-12 · 9,00 × 0,60 × 0,20
02. Planta Entrepiso
6.00 m

M-PE-09 · corte (capas) 1:10

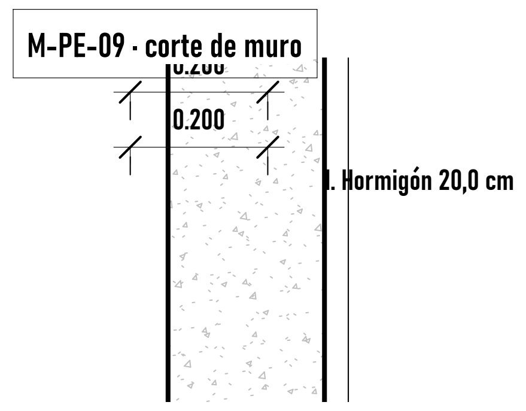
M-PE-09 · corte de muro
0.200
1. Hormigón 20,0 cm

M-PE-10 · corte (capas) 1:10

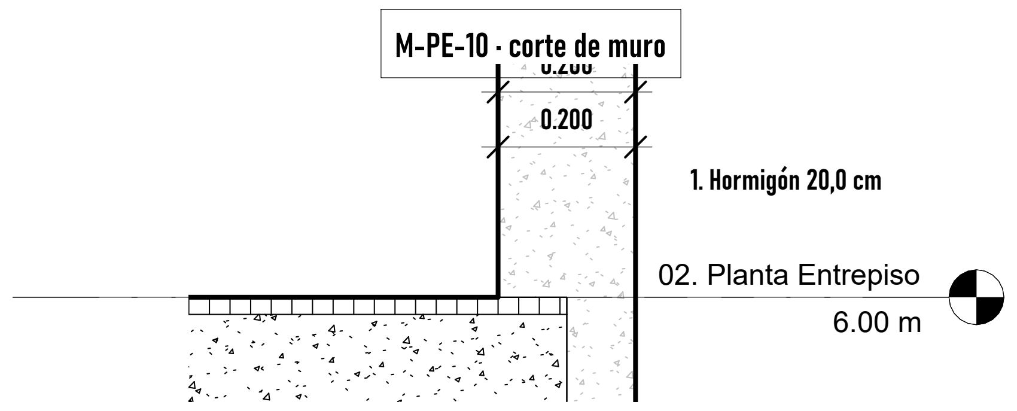
M-PE-10 · corte de muro
0.200
1. Hormigón 20,0 cm
02. Planta Entrepiso
6.00 m

M-PE-11 · corte (capas) 1:10

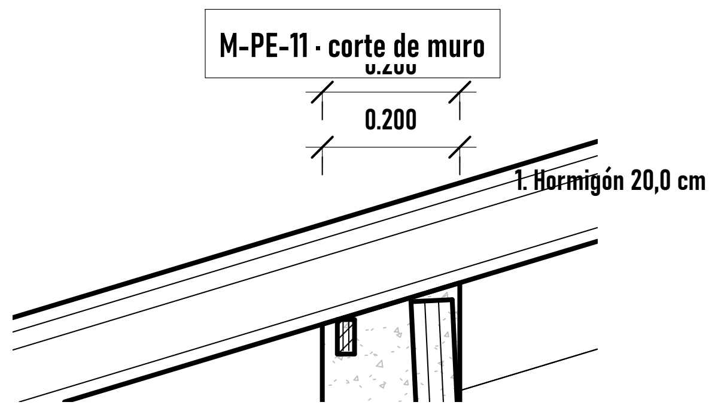
M-PE-11 · corte de muro
0.200
1. Hormigón 20,0 cm

M-PE-12 · corte (capas) 1:10

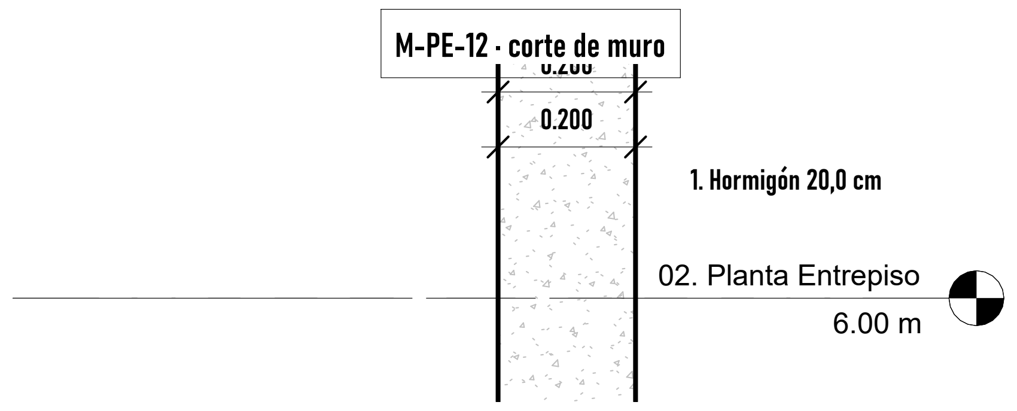
M-PE-12 · corte de muro
0.200
1. Hormigón 20,0 cm
02. Planta Entrepiso
6.00 m

Albañilería R38 (archivo de documentación con el modelo principal vinculado, sin modificarlo). Color por categoría de muro; los muros de H° se computan en Estructura. Códigos M-<nivel>-nn de izquierda a derecha y de arriba hacia abajo. Medidas en metros: largo × alto × espesor.

https://ezeader.myportfolio.com/ezequiel-ader

Consultant
Address
Address
Phone
Fax
e-mail

Consultant
Address
Address
Phone
Fax
e-mail

Consultant
Address
Address
Phone
Fax
e-mail

Consultant
Address
Address
Phone
Fax
e-mail

No.	Description	Date

Angel Luis Brusca

CASA ANGEL

ALB-PE-04

Project number 0001
Date 18 de Agosto, 2025
Drawn by Author
Checked by Checker

Albañilería · PE-04

Scale As indicated

11/2/2026 2:17:23 PM