

CASA ÁNGEL · CLIMATIZACIÓN · COLECTOR CO-N · DETALLE

CO-N · Colector Norte · SM · 02. Planta Entrepiso · 14 circuitos · planta, alzado con gabinete y esquema de salidas

CO-N · alzado frontal con gabinete 1:20

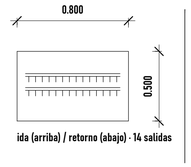


CO-N · planta 1:10

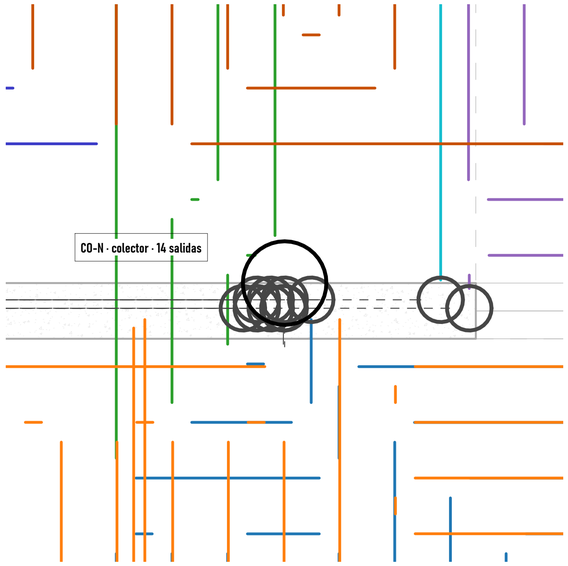

CO-N · esquema de salidas 1:25

CO-N · ida (arriba) / retorno (abajo)

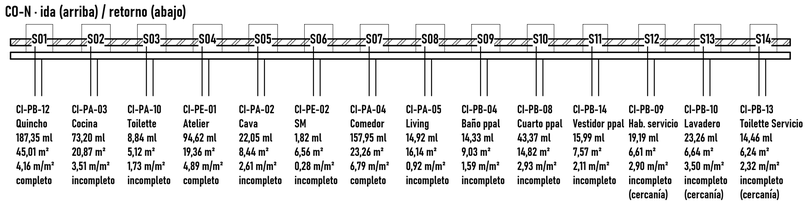

CI-PB-12	CI-PA-03	CI-PA-10	CI-PE-01	CI-PA-02	CI-PE-02	CI-PA-04	CI-PA-05	CI-PB-04	CI-PB-08	CI-PB-14	CI-PB-09	CI-PB-10	CI-PB-13
Quincho	Cocina	Toilette	Atelier	Cava	SM	Comedor	Living	Baño ppal	Cuarto ppal	Vestidor ppal	Hab. servicio	Lavadero	Toilette Servicio
187,35 ml	73,20 ml	8,84 ml	94,62 ml	22,05 ml	1,82 ml	157,95 ml	14,92 ml	14,33 ml	43,37 ml	15,99 ml	19,19 ml	23,26 ml	14,46 ml
45,01 m²	20,87 m²	5,12 m²	19,36 m²	8,44 m²	6,56 m²	23,26 m²	16,14 m²	9,03 m²	14,82 m²	7,57 m²	6,61 m²	6,64 m²	6,24 m²
4,16 m/m²	3,51 m/m²	1,73 m/m²	4,89 m/m²	2,61 m/m²	0,28 m/m²	6,79 m/m²	0,92 m/m²	1,59 m/m²	2,93 m/m²	2,11 m/m²	2,90 m/m²	3,50 m/m²	2,32 m/m²
completo	incompleto	incompleto	completo	incompleto	incompleto	completo	incompleto	incompleto	incompleto	incompleto	incompleto (cercanía)	incompleto (cercanía)	incompleto (cercanía)

Cuadro CO-N

Salidas usadas: 14
Serpentín: 691,35 ml · 195,67 m² servidos
Completos (≥ 4 m/m²): 3 de 14
Asignados por cercanía: 3

Termostatos que comanda

TE-01 · Cava
TE-02 · Lavadero
TE-03 · Quincho
TE-04 · Cuarto ppal
TE-09 · Cocina
TE-10 · Comedor

Montantes de llegada

DI-PE · 9 tramos verticales junto al colector
DI-PA · 2 tramos verticales junto al colector

Climatización R32 (archivo de documentación con el modelo principal vinculado). Piso radiante: serpentines PEX Ø20 (mando + retorno) trazados sobre el eje de cada tubo del modelo; colector de cada circuito por conectividad de tubos y accesorios. Densidad completa ≥ 4 m/m². Bomba de calor: no modelada.

https://ezeader.myportfolio.com/ezequiel-ader

Consultant
Address
Address
Phone
Fax
e-mail

Consultant
Address
Address
Phone
Fax
e-mail

Consultant
Address
Address
Phone
Fax
e-mail

Consultant
Address
Address
Phone
Fax
e-mail

No.	Description	Date

Angel Luis Brusca

CASA ANGEL

CLI-CO-N

Project number	0001
Date	18 de Agosto, 2025
Drawn by	Author
Checked by	Checker

Climatización · CO-N

Scale: As indicated

10/26/2026 10:06:17 AM