
CASA ÁNGEL · CLIMATIZACIÓN · FICHA CI-PA-02 · CAVA

01. Planta Alta · 22,05 ml · 8,44 m² · 2,61 m/m² · CO-N S05 · incompleto

CI-PA-02 · planta 1:10

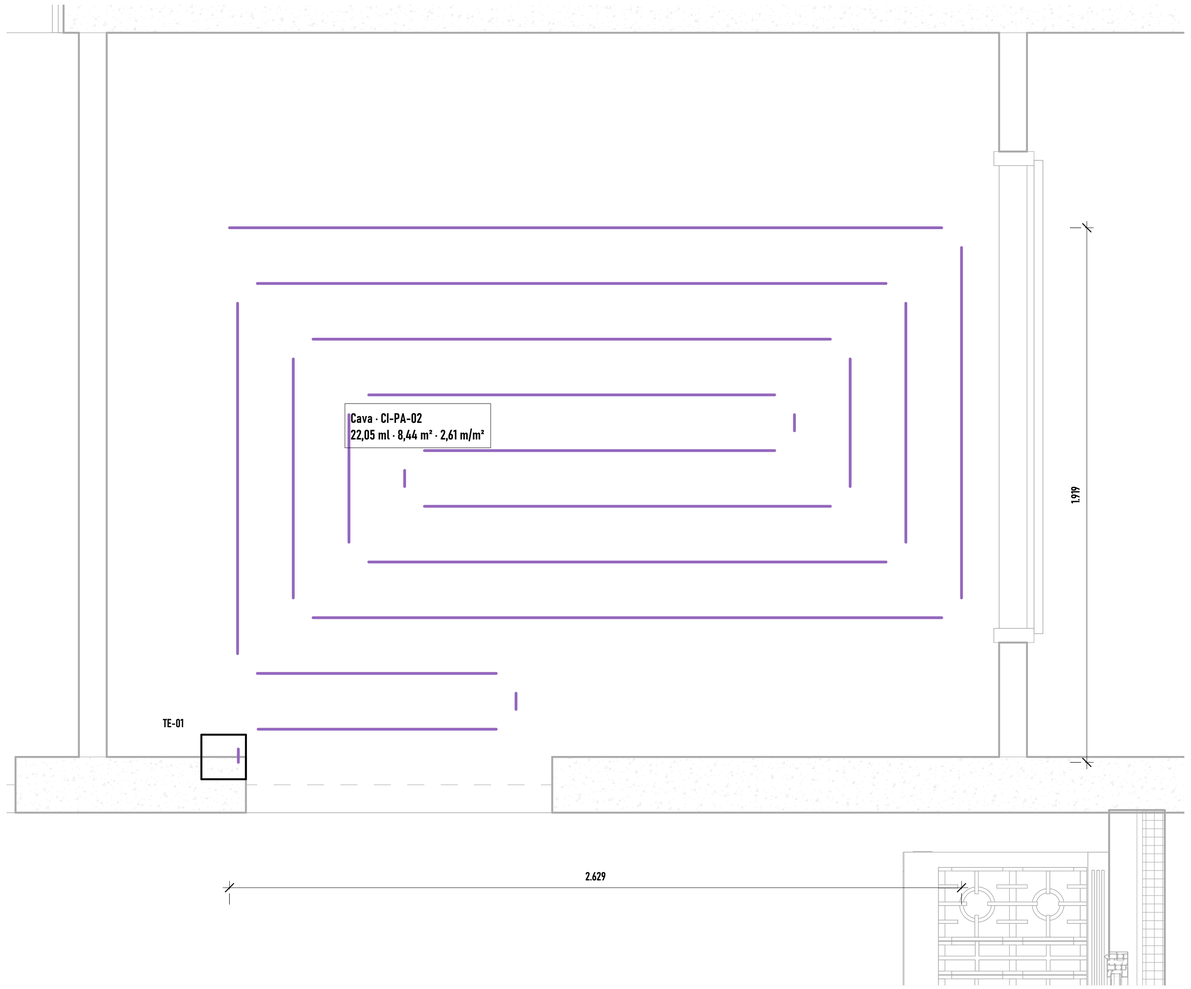

Datos del circuito 1:10

Ficha CI-PA-02

Local: Cava · 01. Planta Alta
Circuito: CI-PA-02
Tubo PEX Ø20: 22,05 ml (ida 10,03 · retorno 12,02)
Superficie servida: 8,44 m²
Densidad: 2,61 m/m² · paso equivalente 0,38 m
Colector: CO-N · salida S05
Termostato: TE-01
Estado: incompleto (completo ≥ 4 m/m²)

Referencias

Trazo de color: serpentín de este circuito sobre el eje del tubo del modelo
Cuadrado: termostato · arquitectura vinculada en medio tono
Cotas: extensión del serpentín (m)

Climatización R32 (archivo de documentación con el modelo principal vinculado). Piso radiante: serpentines PEX Ø20 (mando + retorno) trazados sobre el eje de cada tubo del modelo; colector de cada circuito por conectividad de tubos y accesorios. Densidad completa ≥ 4 m/m². Bomba de calor: no modelada.

https://ezeader.myportfolio.com/ezequiel-ader

Consultant
Address
Address
Phone
Fax
e-mail

Consultant
Address
Address
Phone
Fax
e-mail

Consultant
Address
Address
Phone
Fax
e-mail

Consultant
Address
Address
Phone
Fax
e-mail

No.	Description	Date

Angel Luis Brusca

CASA ANGEL

CLI-F-CI-PA-02

Project number	0001
Date	18 de Agosto, 2025
Drawn by	Author
Checked by	Checker

Climatiz. · CI-PA-02

Scale 1 : 10

10/26/2026 10:06:23 AM