
CASA ÁNGEL · CLIMATIZACIÓN · FICHA CI-PA-06 · PLAYROOM

01. Planta Alta · 137,87 ml · 28,94 m² · 4,76 m/m² · CO-S S02 · completo

CI-PA-06 · planta 1:25

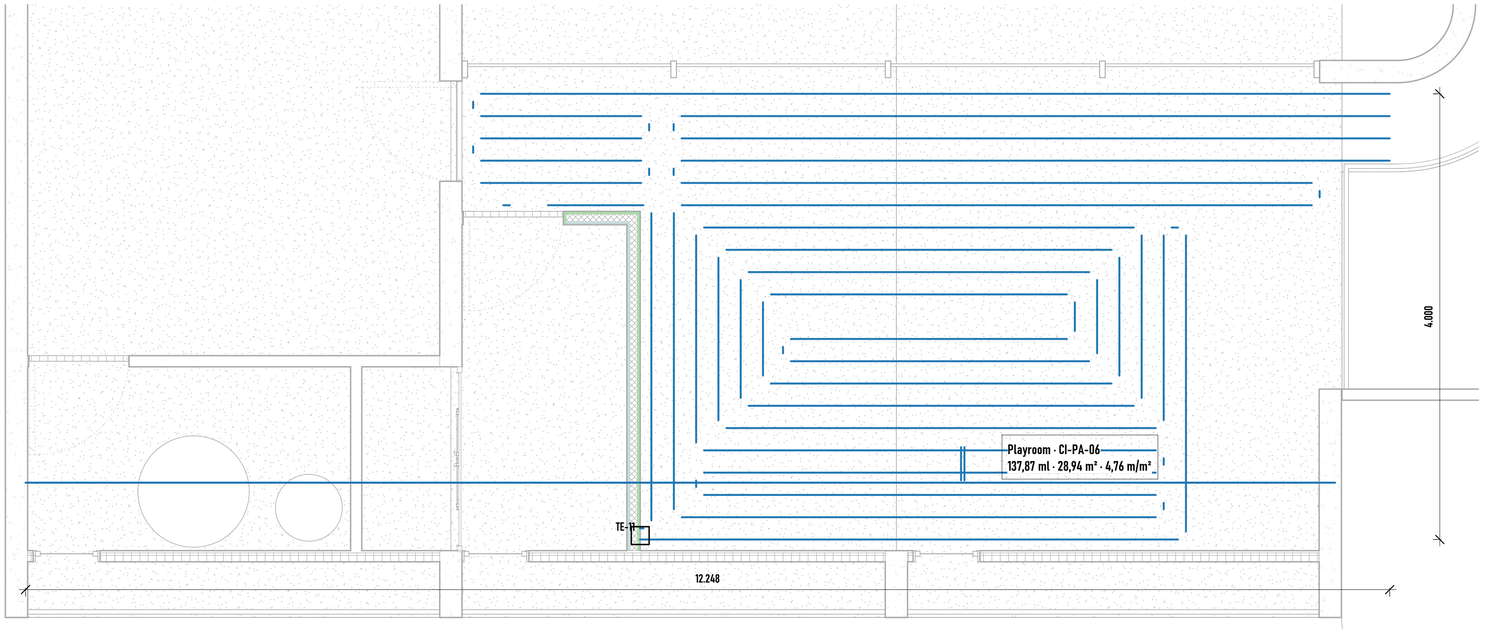

Datos del circuito 1:20

Ficha CI-PA-06

Local: Playroom · 01. Planta Alta
Circuito: CI-PA-06
Tubo PEX Ø20: 137,87 ml (ida 100,34 · retorno 37,53)
Superficie servida: 28,94 m²
Densidad: 4,76 m/m² · paso equivalente 0,21 m
Colector: CO-S · salida S02
Termostato: TE-11
Estado: completo (completo ≥ 4 m/m²)

Referencias

Trazo de color: serpentín de este circuito sobre el eje del tubo del modelo
Cuadrado: termostato · arquitectura vinculada en medio tono
Cotas: extensión del serpentín (m)

Climatización R32 (archivo de documentación con el modelo principal vinculado). Piso radiante: serpentines PEX Ø20 (mando + retorno) trazados sobre el eje de cada tubo del modelo; colector de cada circuito por conectividad de tubos y accesorios. Densidad completa ≥ 4 m/m². Bomba de calor: no modelada.

https://ezeader.myportfolio.com/ezequiel-ader

Consultant
Address
Address
Phone
Fax
e-mail

Consultant
Address
Address
Phone
Fax
e-mail

Consultant
Address
Address
Phone
Fax
e-mail

Consultant
Address
Address
Phone
Fax
e-mail

No.	Description	Date

Angel Luis Brusca

CASA ANGEL

CLI-F-CI-PA-06

Project number	0001
Date	18 de Agosto, 2025
Drawn by	Author
Checked by	Checker

Climatiz. · CI-PA-06

Scale: As indicated

10/26/2026 10:06:27 AM