
CASA ÁNGEL · CLIMATIZACIÓN · FICHA CI-PB-05 · CUARTO A INV.

00. Planta Baja · 27,41 ml · 11,86 m² · 2,31 m/m² · CO-S S09 · incompleto

CI-PB-05 · planta 1:20

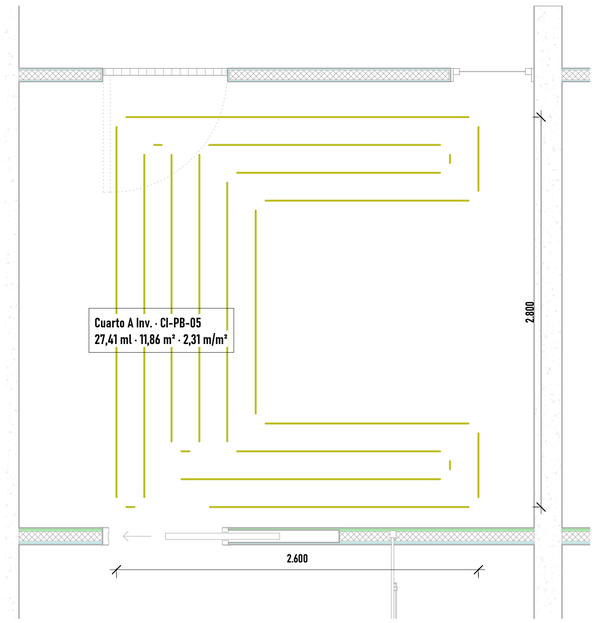

Datos del circuito 1:10

Ficha CI-PB-05

Local: Cuarto A Inv. · 00. Planta Baja
Circuito: CI-PB-05
Tubo PEX Ø20: 27,41 ml (ida 14,83 · retorno 12,58)
Superficie servida: 11,86 m²
Densidad: 2,31 m/m² · paso equivalente 0,43 m
Colector: CO-S · salida S09
Termostato: (ninguno en el modelo)
Estado: incompleto (completo ≥ 4 m/m²)

Referencias

Trazo de color: serpentín de este circuito sobre el eje del tubo del modelo
Cuadrado: termostato · arquitectura vinculada en medio tono
Cotas: extensión del serpentín (m)

Climatización R32 (archivo de documentación con el modelo principal vinculado). Piso radiante: serpentines PEX Ø20 (mando + retorno) trazados sobre el eje de cada tubo del modelo; colector de cada circuito por conectividad de tubos y accesorios. Densidad completa ≥ 4 m/m². Bomba de calor: no modelada.

https://ezeader.myportfolio.com/ezequiel-ader

Consultant
Address
Address
Phone
Fax
e-mail

Consultant
Address
Address
Phone
Fax
e-mail

Consultant
Address
Address
Phone
Fax
e-mail

Consultant
Address
Address
Phone
Fax
e-mail

No.	Description	Date

Angel Luis Brusca

CASA ANGEL

CLI-F-CI-PB-05

Project number	0001
Date	18 de Agosto, 2025
Drawn by	Author
Checked by	Checker

Climatiz. · CI-PB-05

Scale As indicated

10/26/2026 10:06:36 AM