

1 AXO - TANQUE NORTE

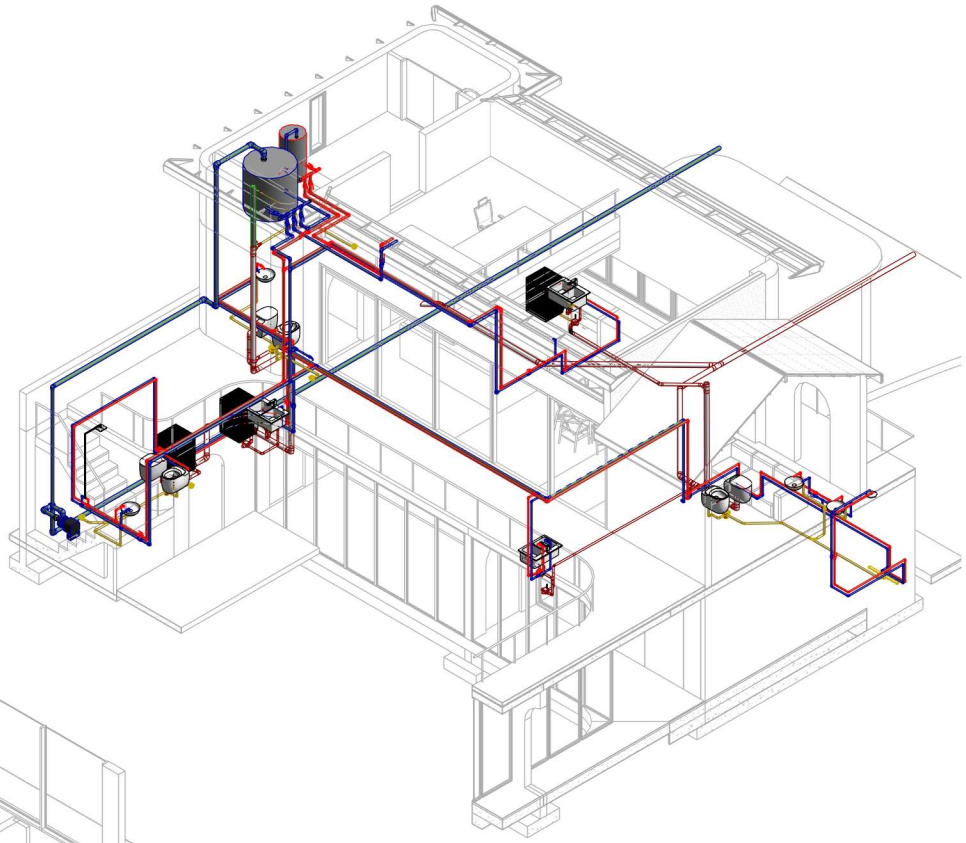

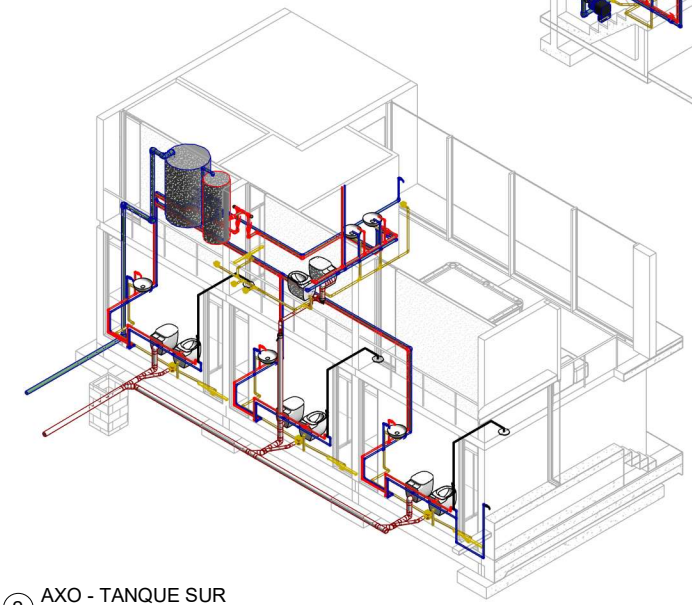

2 AXO - TANQUE SUR

https://ezeader.myportfolio.com/ezequiel-ader

Consultant
Address
Address
Phone
Fax
e-mail

Consultant
Address
Address
Phone
Fax
e-mail

Consultant
Address
Address
Phone
Fax
e-mail

Consultant
Address
Address
Phone
Fax
e-mail

No.	Description	Date

Angel Luis Brusca

CASA ANGEL


Tanques

Project number	0001
Date	18 de Agosto, 2025
Drawn by	ADER
Checked by	Checker


AFyAC

Scale

10/9/2025 12:14:30 PM

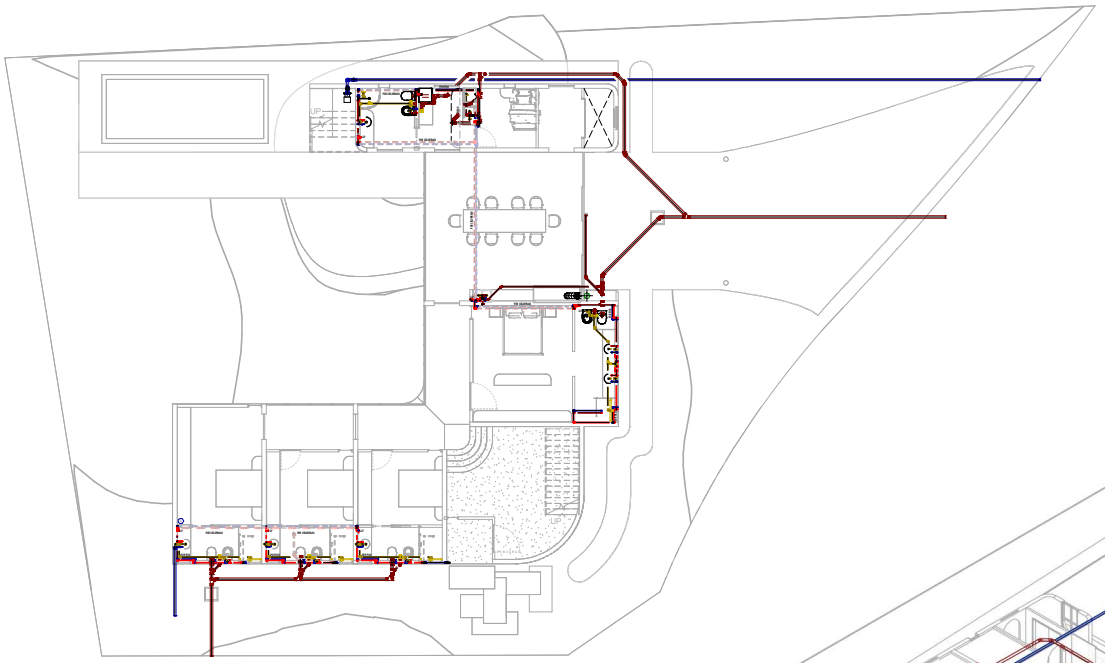

1 00 - PB
1 : 100

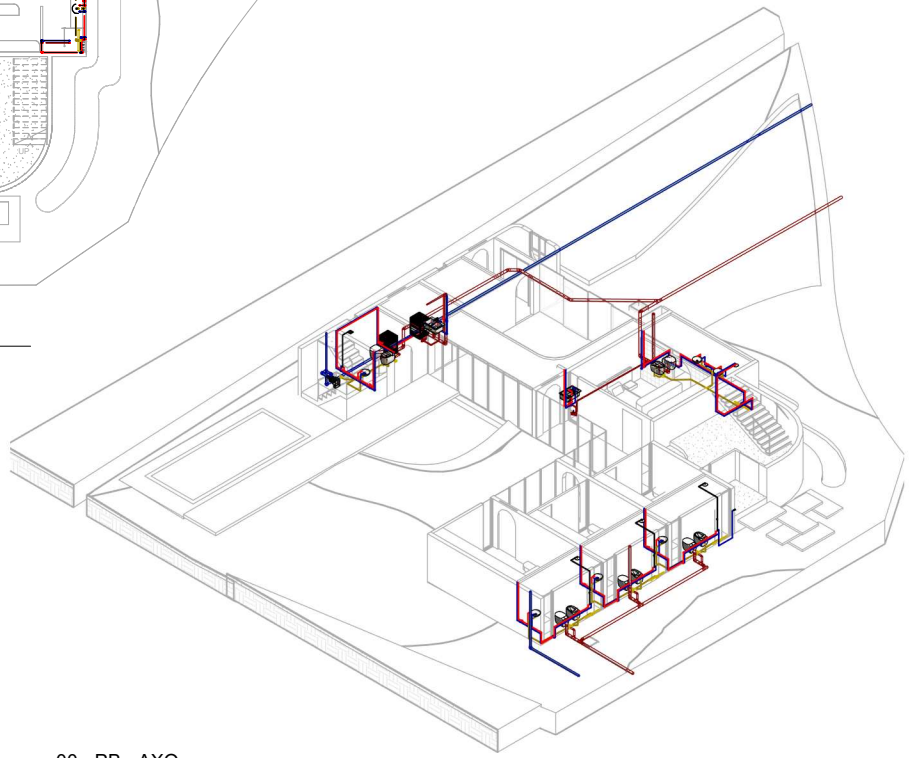

2 00 - PB - AXO

https://ezeader.myportfolio.com/ezequiel-ader

Consultant
Address
Address
Phone
Fax
e-mail

Consultant
Address
Address
Phone
Fax
e-mail

Consultant
Address
Address
Phone
Fax
e-mail

Consultant
Address
Address
Phone
Fax
e-mail

No.	Description	Date

Angel Luis Brusca

CASA ANGEL


PB

Project number	0001
Date	18 de Agosto, 2025
Drawn by	ADER
Checked by	Checker


AFyAC .00

Scale	1 : 100


10/9/2025 12:14:35 PM

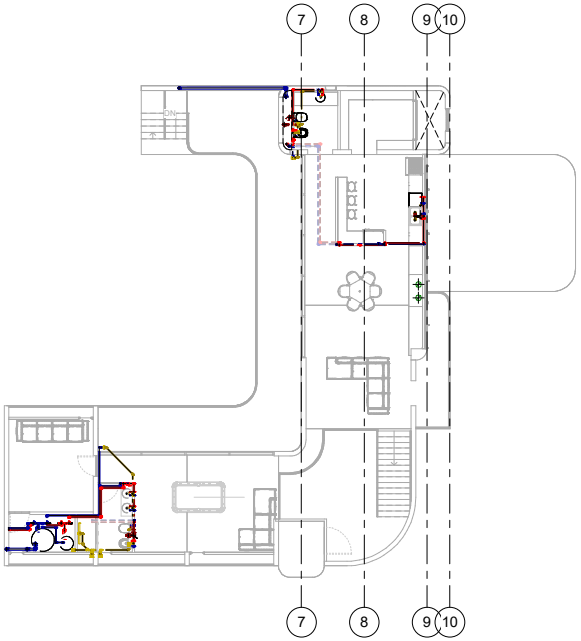


1 01 - PA
1 : 100

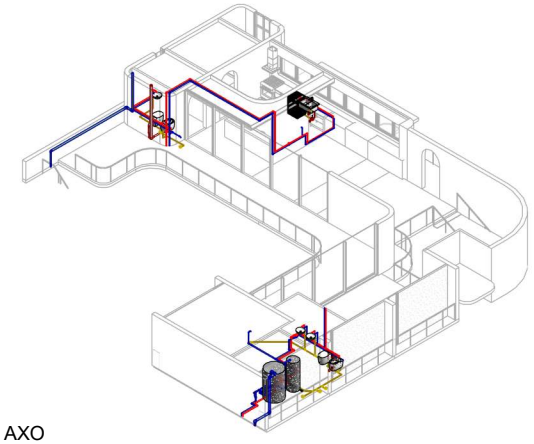

2 01 - PA - AXO

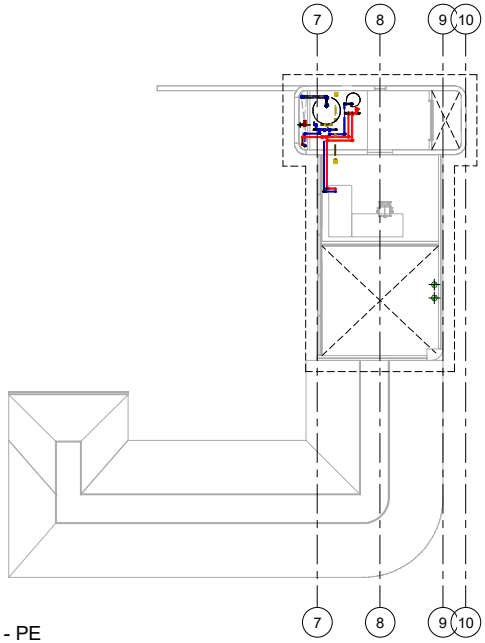

3 02 - PE
1 : 100

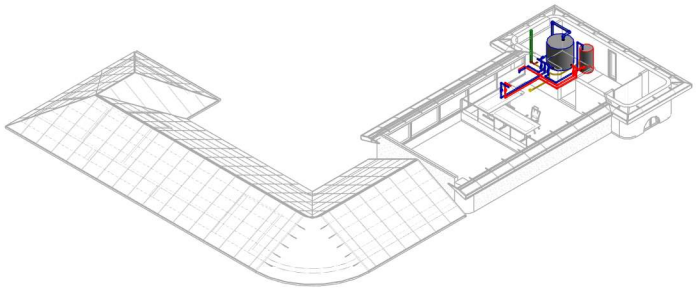

4 02 - PE - AXO

https://ezeader.myportfolio.com/ezequiel-ader

Consultant	Consultant
Address	Address
Address	Address
Phone	Phone
Fax	Fax
e-mail	e-mail

Consultant	Consultant
Address	Address
Address	Address
Phone	Phone
Fax	Fax
e-mail	e-mail

No.	Description	Date

Angel Luis Brusca

CASA ANGEL


PA y PE

Project number	0001
Date	18 de Agosto, 2025
Drawn by	ADER
Checked by	Checker


AFyAC .01 y .02

Scale	1 : 100


10/9/2025 12:14:40 PM

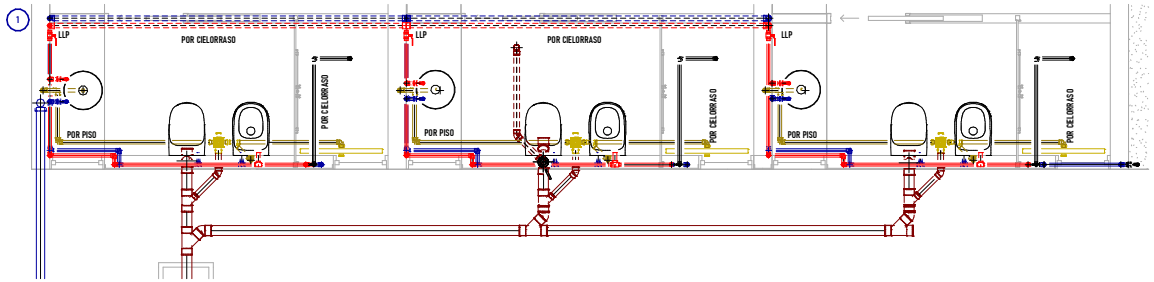


1 P.DET - 00 - BAÑO INV
1 : 25

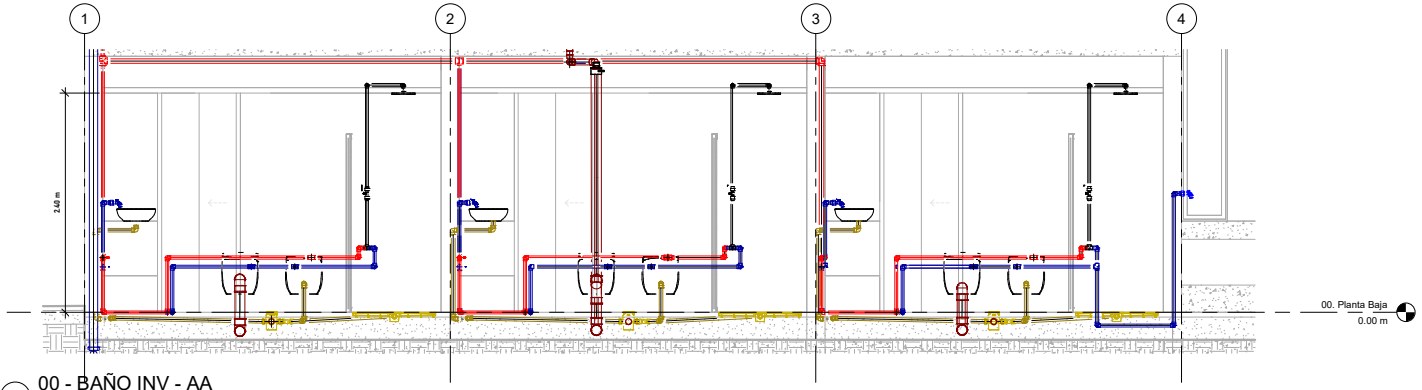


2 00 - BAÑO INV - AA
1 : 25

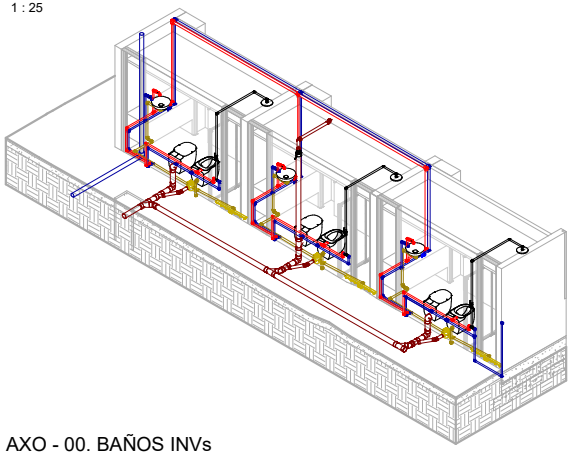

3 AXO - 00. BAÑOS INVs

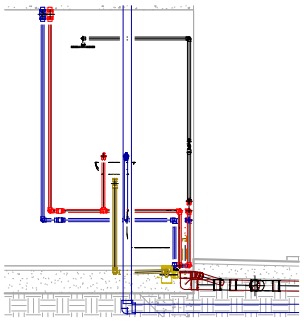

4 00 - BAÑO INV - BB
1 : 25

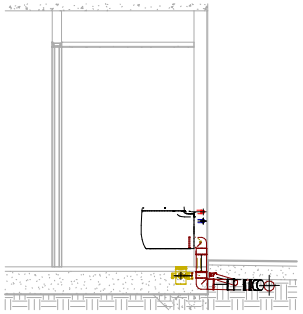

5 00 - BAÑO INV - CC
1 : 25

https://ezeader.myportfolio.com/ezequiel-ader

Consultant
Address
Address
Phone
Fax
e-mail

Consultant
Address
Address
Phone
Fax
e-mail

Consultant
Address
Address
Phone
Fax
e-mail

Consultant
Address
Address
Phone
Fax
e-mail

No.	Description	Date

Angel Luis Brusca

CASA ANGEL


Baño invitados

Project number	0001
Date	18 de Agosto, 2025
Drawn by	ADER
Checked by	Checker


IS.0001

Scale 1 : 25


10/9/2025 12:14:46 PM

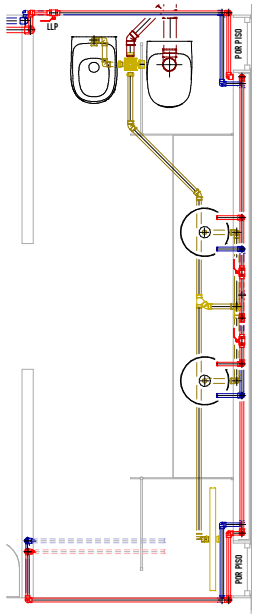


1 P.DET - 00 - BAÑO PPAL
1 : 20

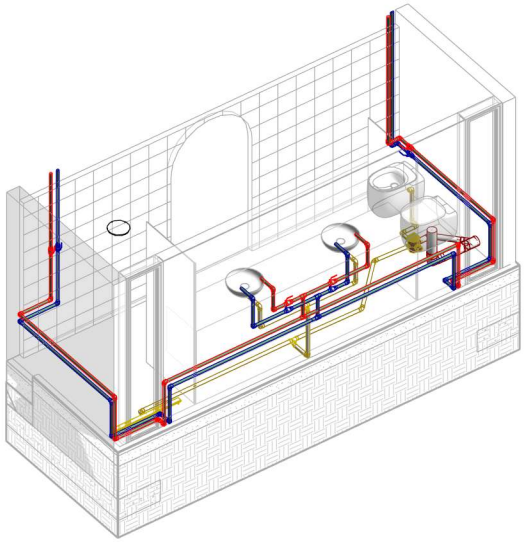


2 AXO - 00. BAÑO PPAL

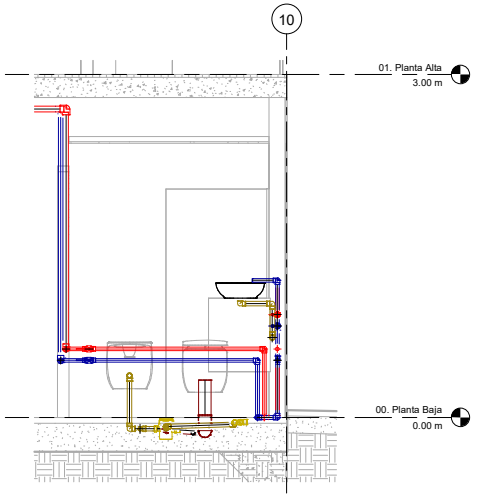

3 00 - BAÑO PPAL - BB
1 : 20

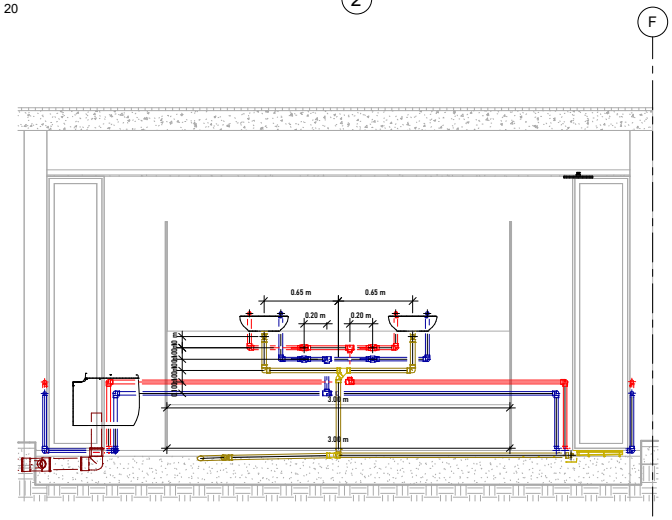

4 00 - BAÑO PPAL - AA
1 : 20

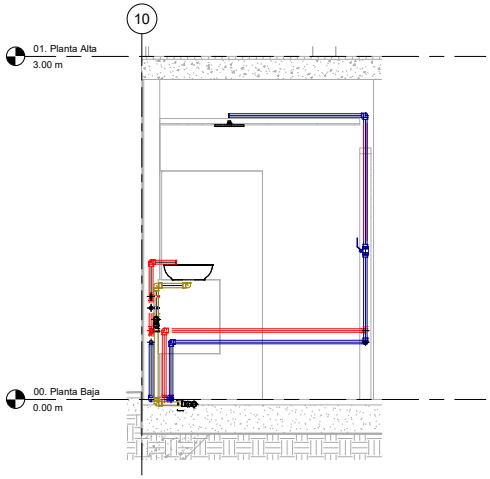

5 00 - BAÑO PPAL - CC
1 : 20

https://ezeader.myportfolio.com/ezequiel-ader

Consultant
Address
Address
Phone
Fax
e-mail

Consultant
Address
Address
Phone
Fax
e-mail

Consultant
Address
Address
Phone
Fax
e-mail

Consultant
Address
Address
Phone
Fax
e-mail

No.	Description	Date

Angel Luis Brusca

CASA ANGEL


Baño principal

Project number	0001
Date	18 de Agosto, 2025
Drawn by	ADER
Checked by	Checker


IS.0002

Scale 1 : 20


10/9/2025 12:14:49 PM

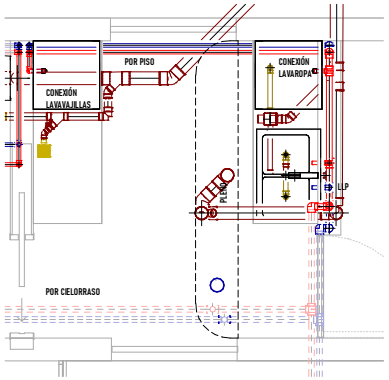


1 P.DET - 00 - LAVADERO
1 : 20

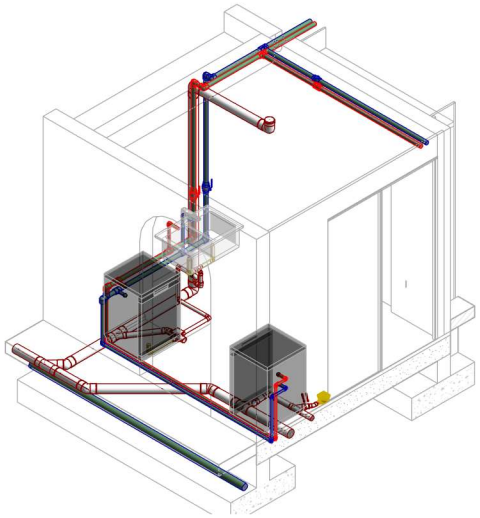


2 AXO - 00. LAVADERO

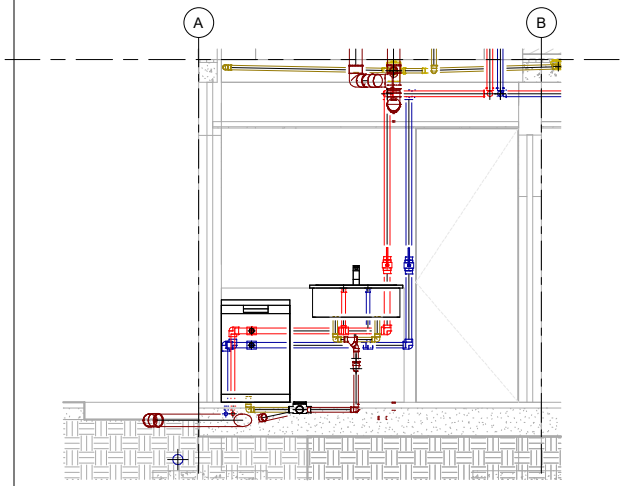

3 00 - LAVADERO - AA
1 : 20

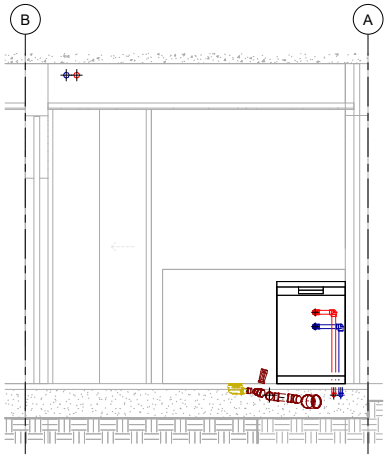

4 00 - LAVADERO - BB
1 : 20

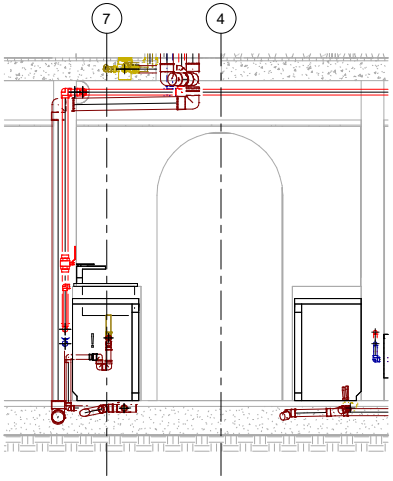

5 00 - LAVADERO - CC
1 : 20

https://ezeader.myportfolio.com/ezequiel-ader

Consultant
Address
Address
Phone
Fax
e-mail

Consultant
Address
Address
Phone
Fax
e-mail

Consultant
Address
Address
Phone
Fax
e-mail

Consultant
Address
Address
Phone
Fax
e-mail

No.	Description	Date

Angel Luis Brusca

CASA ANGEL


Lavadero

Project number	0001
Date	18 de Agosto, 2025
Drawn by	ADER
Checked by	Checker


IS.0003

Scale 1 : 20


10/9/2025 12:14:52 PM

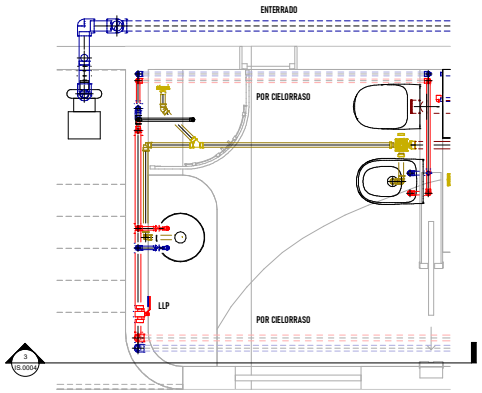


1 P.DET - 00 - TOILETTE
1 : 20

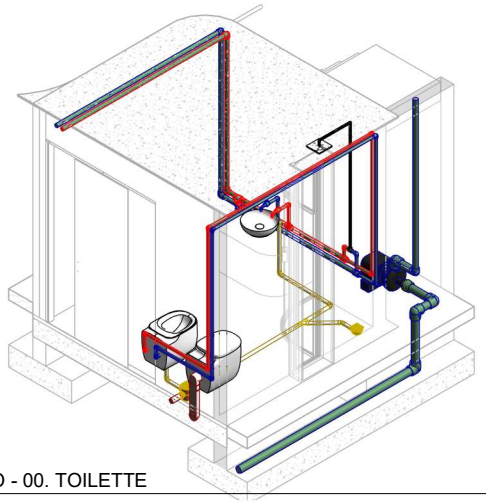


2 AXO - 00. TOILETTE

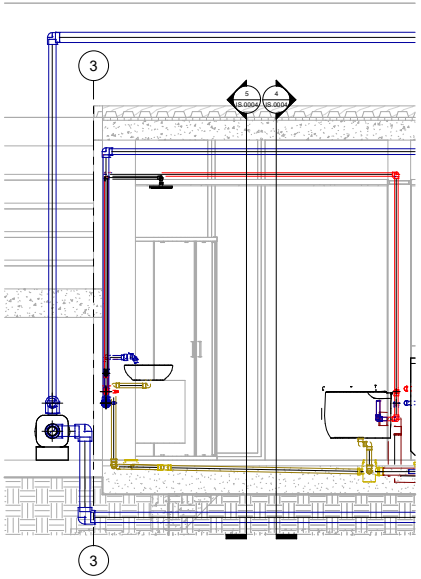

3 00 - TOILETTE - AA
1 : 20

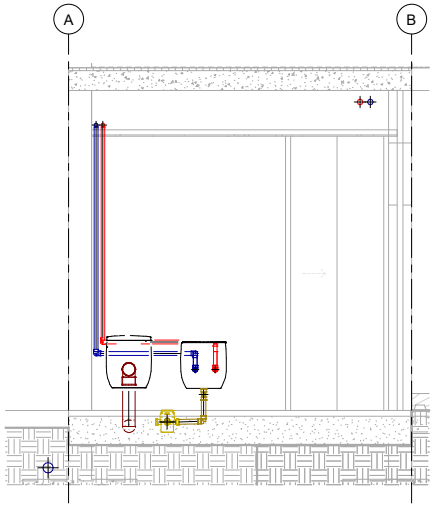

4 00 - TOILETTE - BB
1 : 20

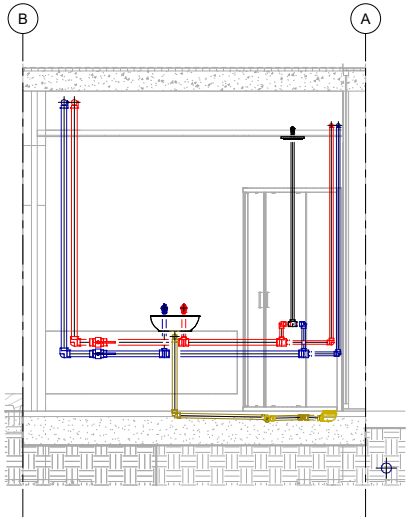

5 00 - TOILETTE - CC
1 : 20

https://ezeader.myportfolio.com/ezequiel-ader

Consultant
Address
Address
Phone
Fax
e-mail

Consultant
Address
Address
Phone
Fax
e-mail

Consultant
Address
Address
Phone
Fax
e-mail

Consultant
Address
Address
Phone
Fax
e-mail

No.	Description	Date

Angel Luis Brusca

CASA ANGEL


Toilette

Project number	0001
Date	18 de Agosto, 2025
Drawn by	ADER
Checked by	Checker


IS.0004

Scale 1 : 20

10/9/2025 12:14:55 PM

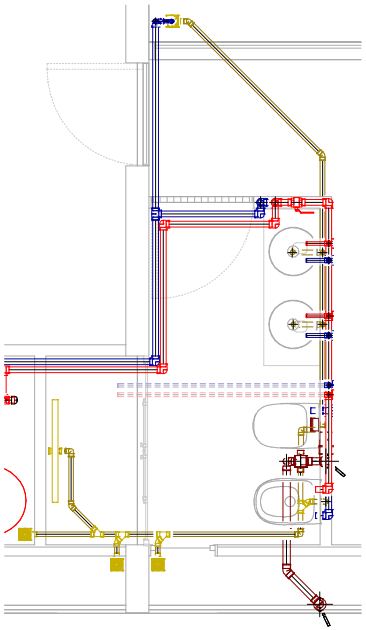


1 P.DET - 01 - BAÑO
1 : 20

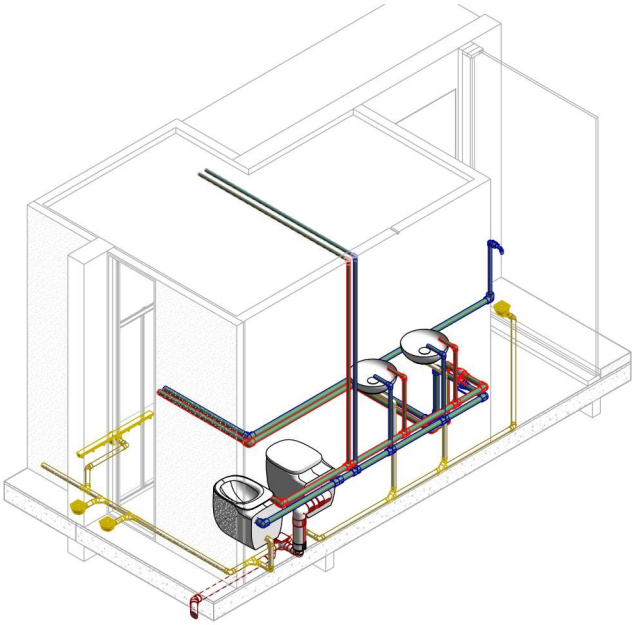

2 AXO - 01. BAÑO

3 01 - BAÑO - AA
1 : 20

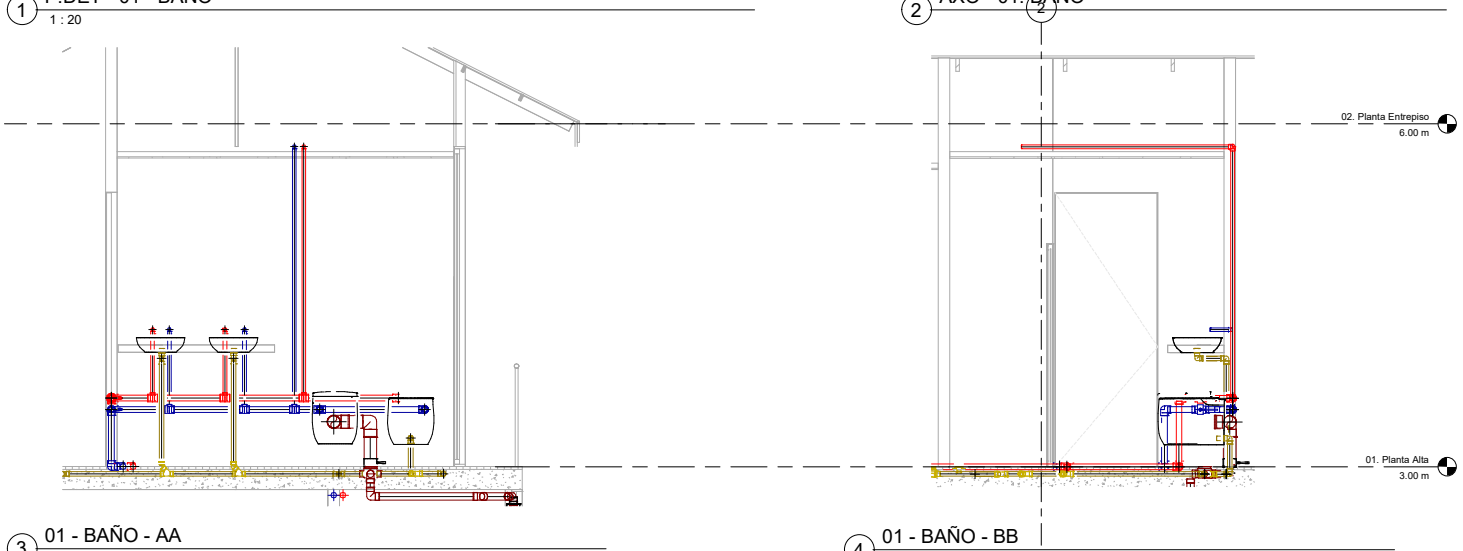

4 01 - BAÑO - BB
1 : 20

https://ezeader.myportfolio.com/ezequiel-ader

Consultant
Address
Address
Phone
Fax
e-mail

Consultant
Address
Address
Phone
Fax
e-mail

Consultant
Address
Address
Phone
Fax
e-mail

Consultant
Address
Address
Phone
Fax
e-mail

No.	Description	Date

Angel Luis Brusca

CASA ANGEL


Baño

Project number	0001
Date	18 de Agosto, 2025
Drawn by	ADER
Checked by	Checker


IS.0101

Scale 1 : 20


10/9/2025 12:14:58 PM

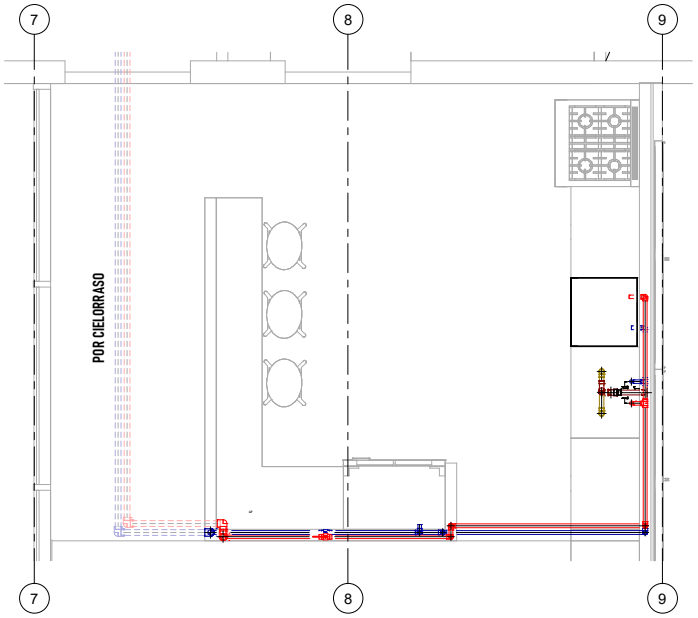


1 P.DET - 01 - COCINA
1 : 20

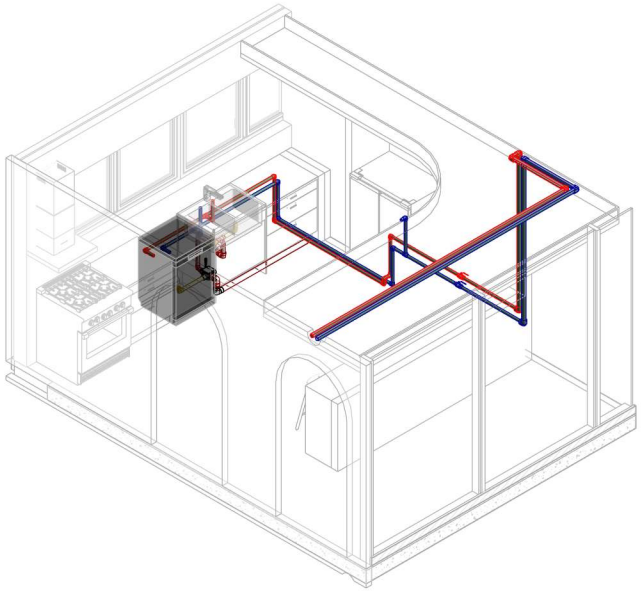

2 AXO - 01. COCINA

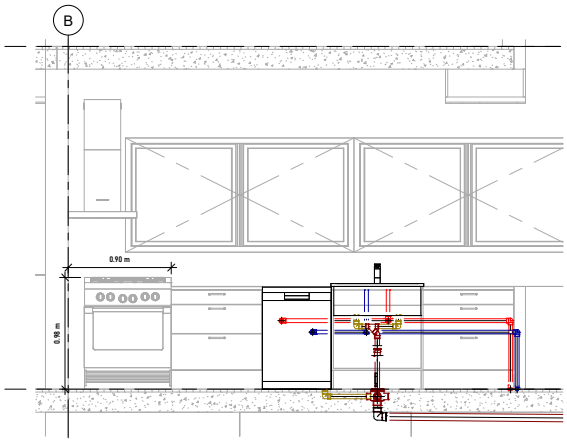

3 01 - COCINA - AA
1 : 20

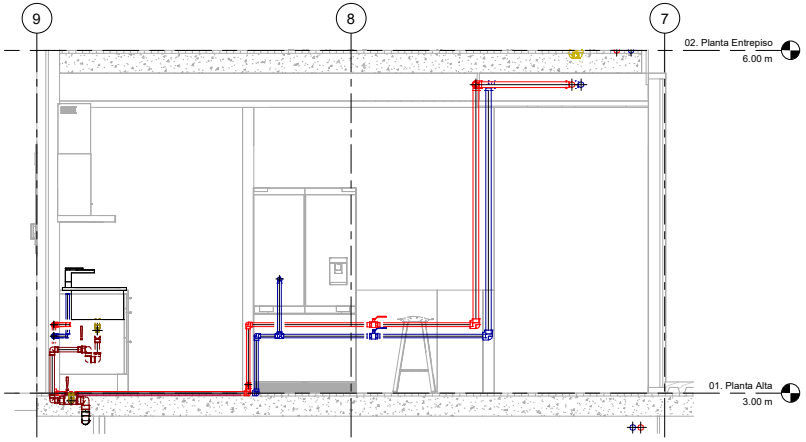

4 01 - COCINA - BB
1 : 20

https://ezeader.myportfolio.com/ezequiel-ader

Consultant
Address
Address
Phone
Fax
e-mail

Consultant
Address
Address
Phone
Fax
e-mail

Consultant
Address
Address
Phone
Fax
e-mail

Consultant
Address
Address
Phone
Fax
e-mail

No.	Description	Date

Angel Luis Brusca

CASA ANGEL


Cocina

Project number	0001
Date	18 de Agosto, 2025
Drawn by	ADER
Checked by	Checker


IS.0102

Scale	1 : 20


10/9/2025 12:15:00 PM

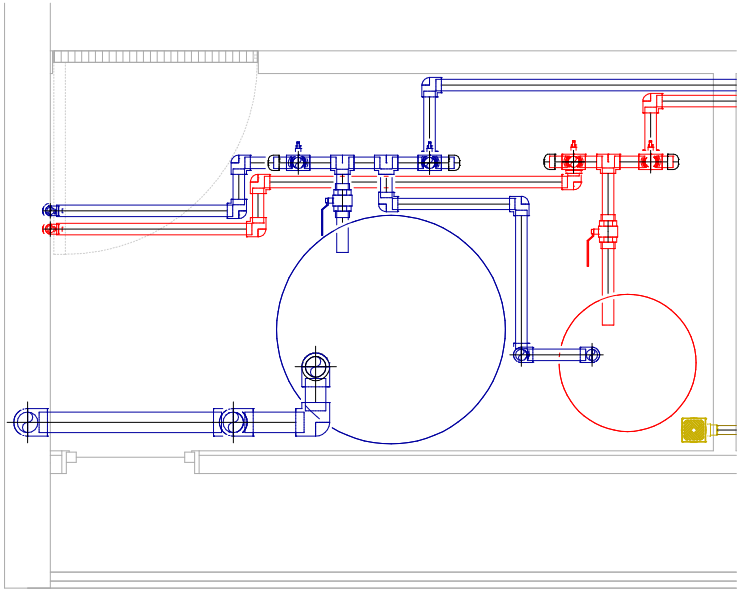

1 P.DET - 01 - SM
1 : 10

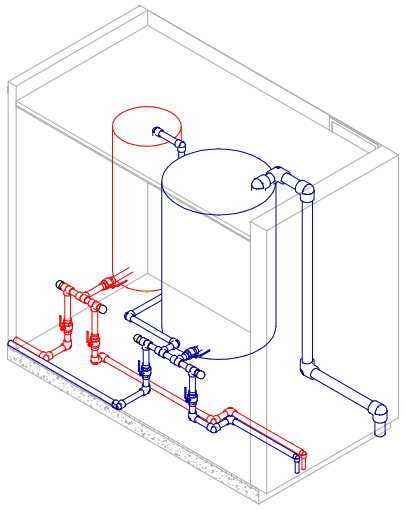

2 AXO - 01. SM. TS

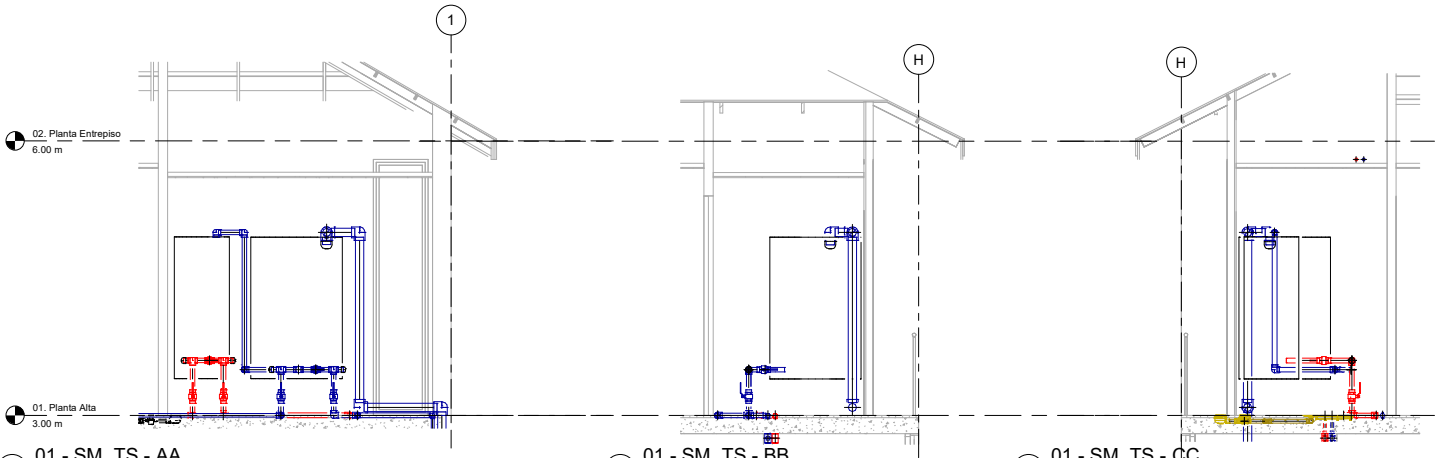

3 01 - SM. TS - AA
1 : 25

4 01 - SM. TS - BB
1 : 25

5 01 - SM. TS - CC
1 : 25

https://ezeader.myportfolio.com/ezequiel-ader

Consultant
Address
Address
Phone
Fax
e-mail

Consultant
Address
Address
Phone
Fax
e-mail

Consultant
Address
Address
Phone
Fax
e-mail

Consultant
Address
Address
Phone
Fax
e-mail

No.	Description	Date

Angel Luis Brusca

CASA ANGEL


Sala de Máquinas

Project number	0001
Date	18 de Agosto, 2025
Drawn by	ADER
Checked by	Checker


IS.0103

Scale: As indicated


10/9/2025 12:15:02 PM

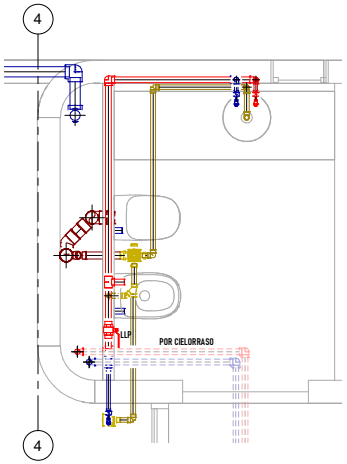


1 P.DET - 01 - TOILETTE
1 : 20

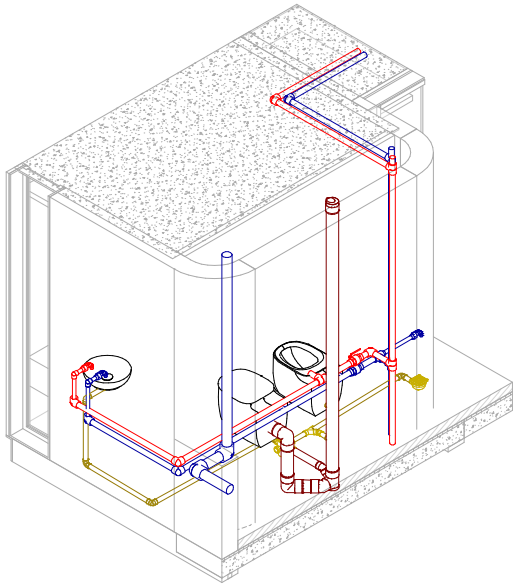

2 AXO - 01. TOILETTE

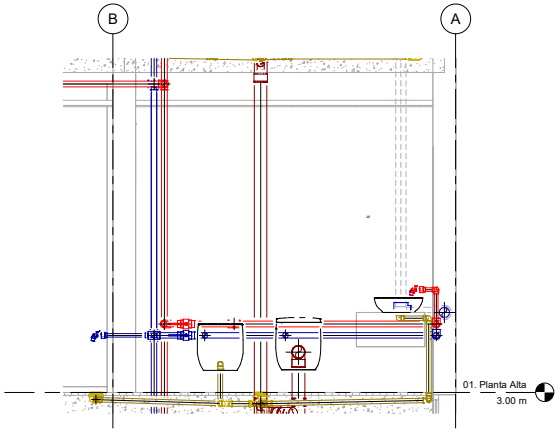

3 01 - TOILETTE - AA
1 : 20

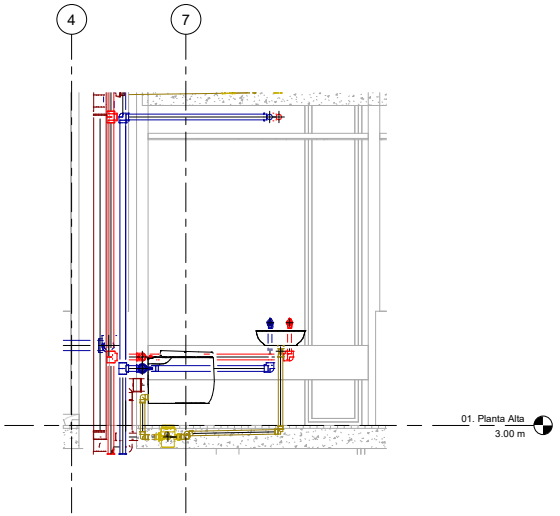

4 01 - TOILETTE - BB
1 : 20

https://ezeader.myportfolio.com/ezequiel-ader

Consultant
Address
Address
Phone
Fax
e-mail

Consultant
Address
Address
Phone
Fax
e-mail

Consultant
Address
Address
Phone
Fax
e-mail

Consultant
Address
Address
Phone
Fax
e-mail

No.	Description	Date

Angel Luis Brusca

CASA ANGEL


Toilette

Project number	0001
Date	18 de Agosto, 2025
Drawn by	ADER
Checked by	Checker


IS.0104

Scale 1 : 20


10/9/2025 12:15:05 PM

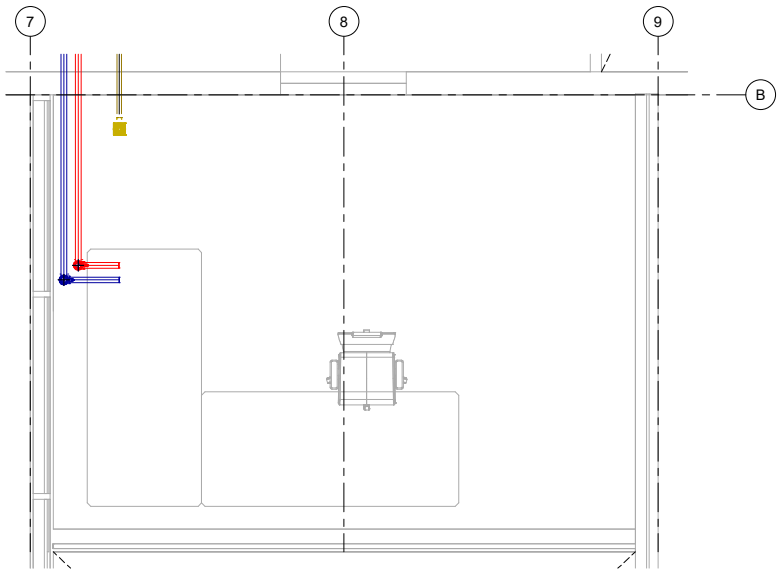

1 P.DET - 02 - ATELIER
1 : 20

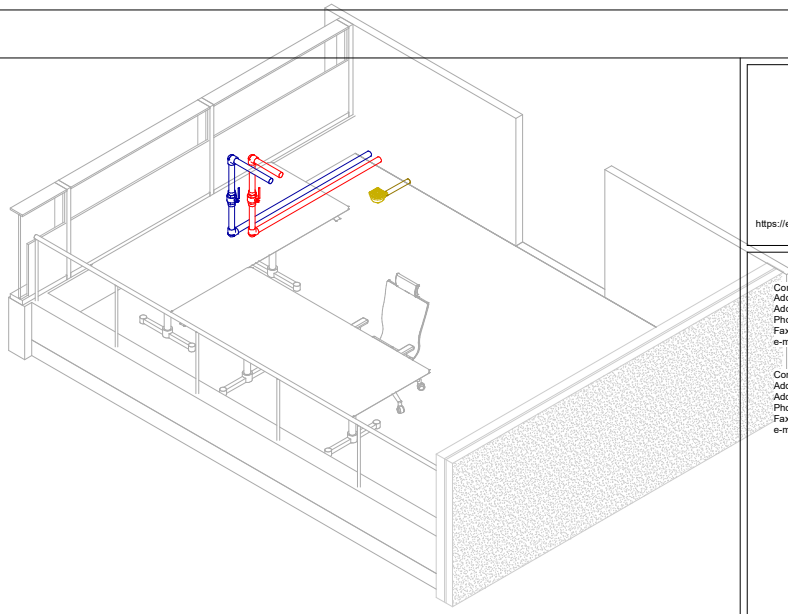

2 AXO - 02. ATELIER

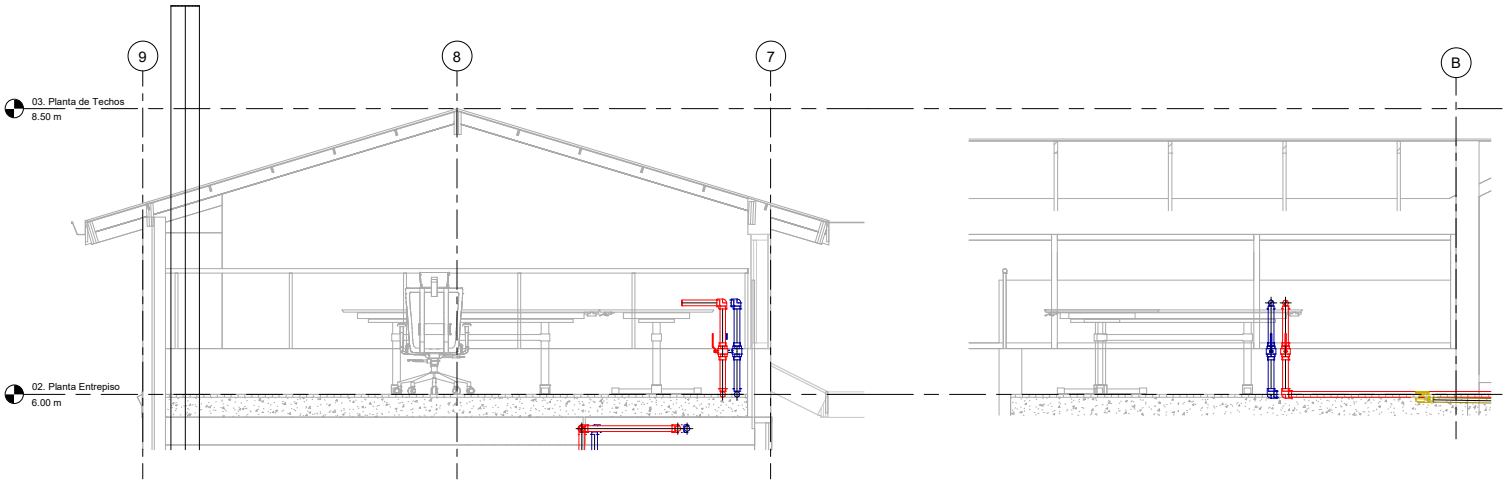

3 02 - ATELIER - AA
1 : 20

4 02 - ATELIER - BB
1 : 20

https://ezeader.myportfolio.com/ezequiel-ader

Consultant
Address
Address
Phone
Fax
e-mail

Consultant
Address
Address
Phone
Fax
e-mail

Consultant
Address
Address
Phone
Fax
e-mail

Consultant
Address
Address
Phone
Fax
e-mail

No.	Description	Date

Angel Luis Brusca

CASA ANGEL


Atelier

Project number	0001
Date	18 de Agosto, 2025
Drawn by	ADER
Checked by	Checker


IS.0201

Scale 1 : 20


10/9/2025 12:15:06 PM

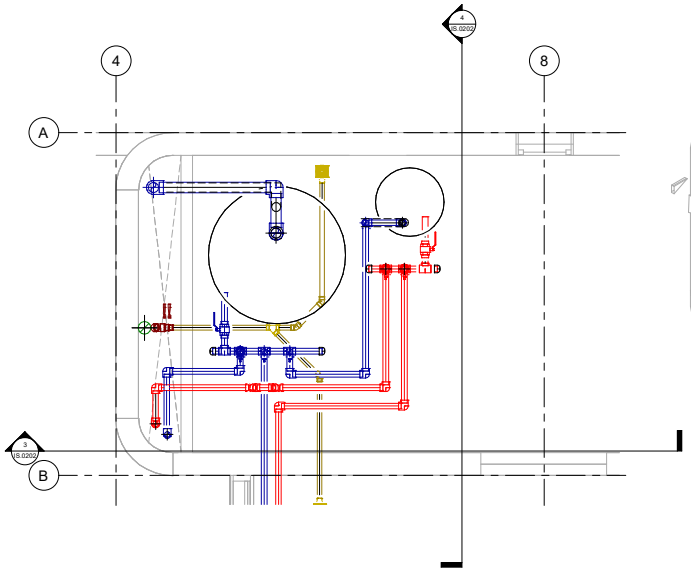

1 P.DET - 02 - SM
1 : 20

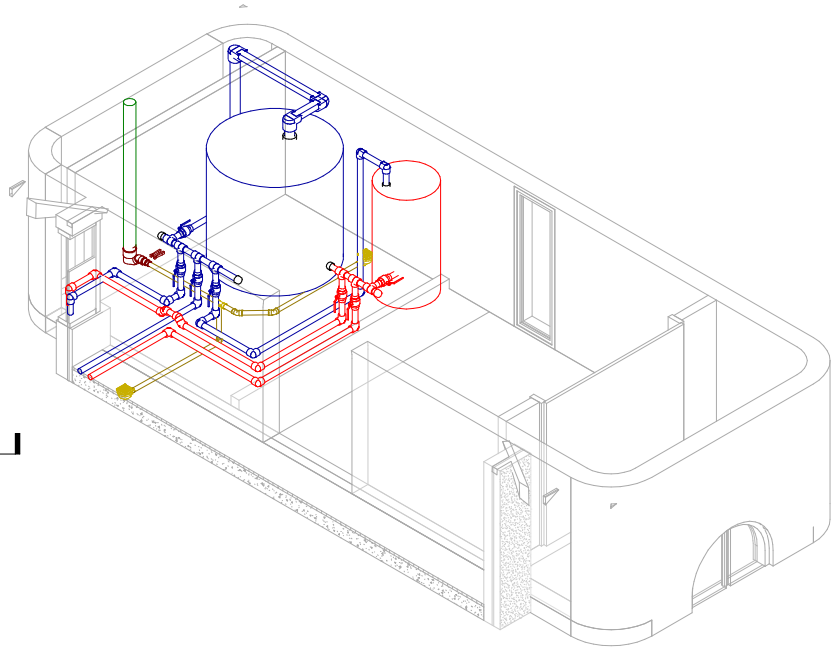

2 AXO - 02. SM. TN

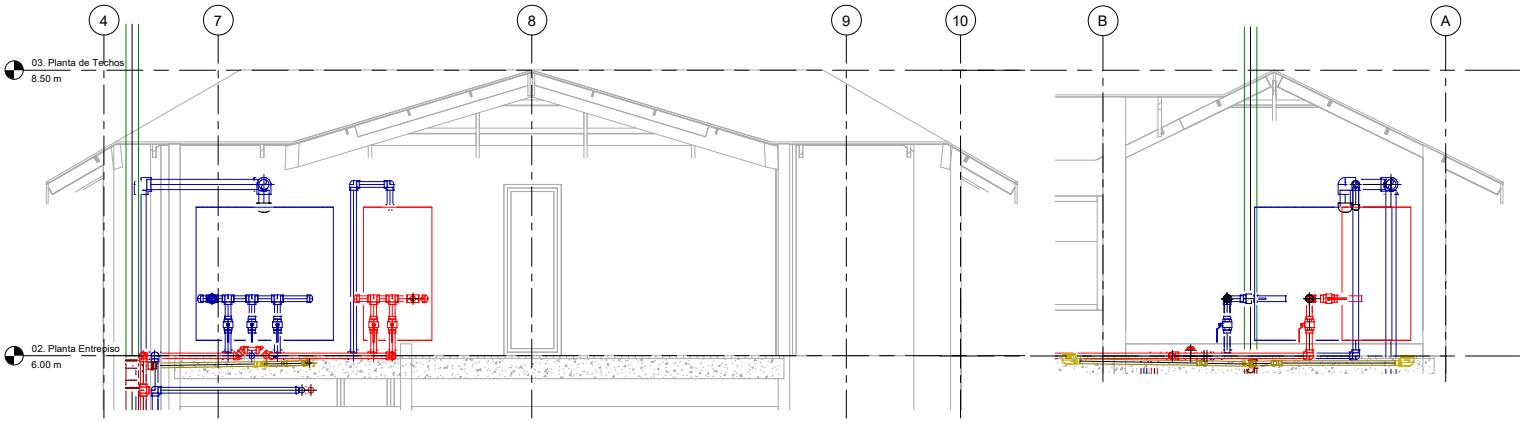

3 02 - SM. TN- AA
1 : 20

4 02 - SM. TN- BB
1 : 20

https://ezeader.myportfolio.com/ezequiel-ader

Consultant
Address
Address
Phone
Fax
e-mail

Consultant
Address
Address
Phone
Fax
e-mail

Consultant
Address
Address
Phone
Fax
e-mail

Consultant
Address
Address
Phone
Fax
e-mail

No.	Description	Date

Angel Luis Brusca

CASA ANGEL


Sala de Máquinas

Project number	0001
Date	18 de Agosto, 2025
Drawn by	ADER
Checked by	Checker

IS.0202

Scale 1 : 20

10/9/2025 12:15:08 PM

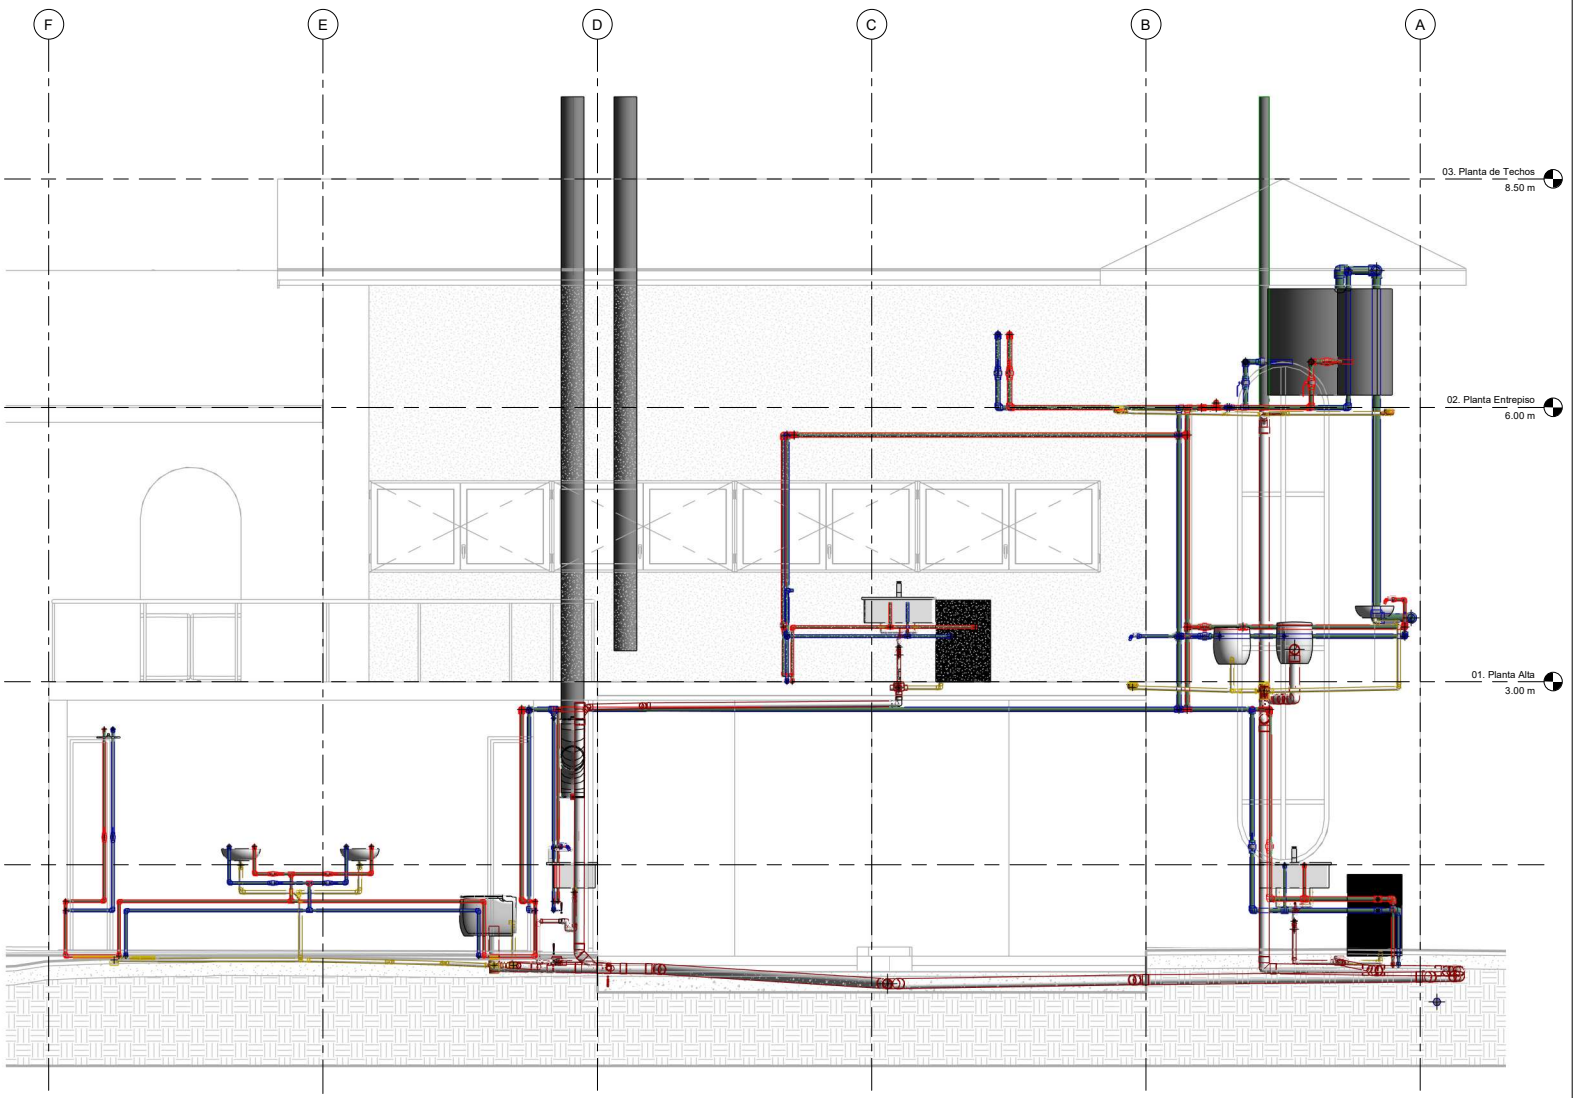

1 CORTE LONG.CC
1 : 25

https://ezeader.myportfolio.com/ezequiel-ader

Consultant
Address
Address
Phone
Fax
e-mail

Consultant
Address
Address
Phone
Fax
e-mail

Consultant
Address
Address
Phone
Fax
e-mail

Consultant
Address
Address
Phone
Fax
e-mail

No.	Description	Date

Angel Luis Brusca

CASA ANGEL


CORTE AA

Project number	0001
Date	18 de Agosto, 2025
Drawn by	ADER
Checked by	Checker

IS.0C01

Scale 1 : 25

10/9/2025 12:15:11 PM

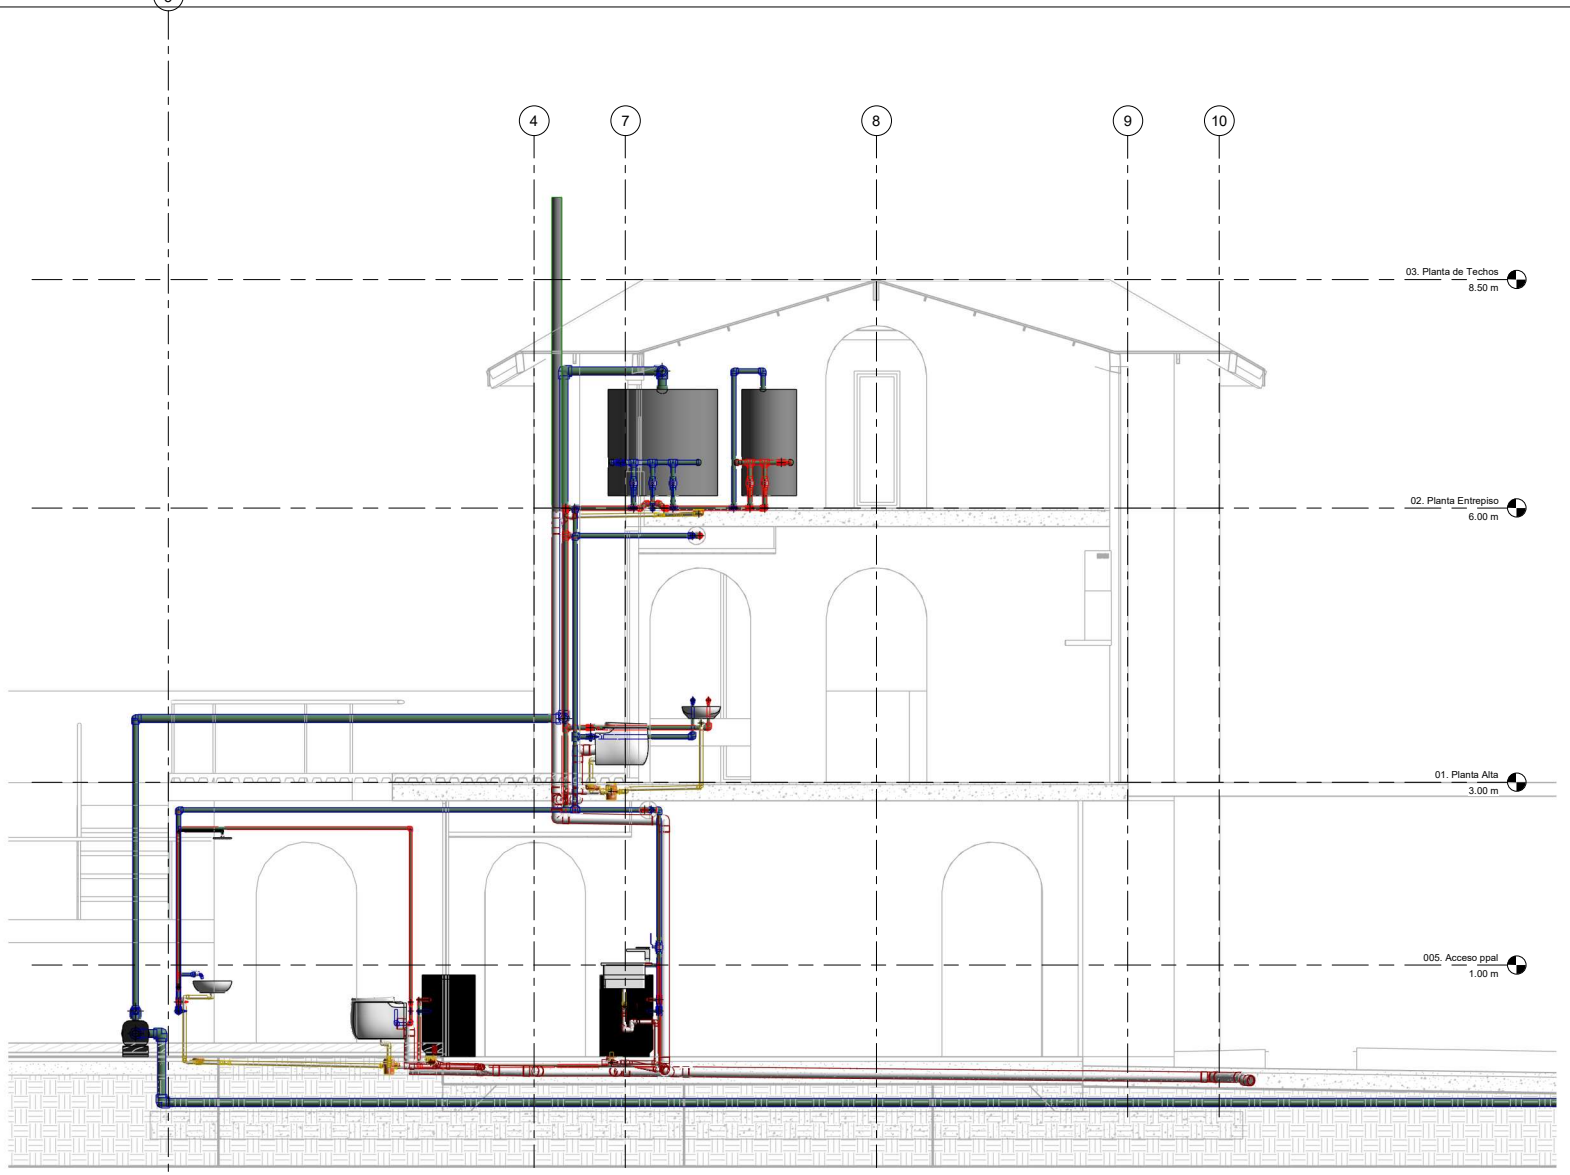

1 CORTE TRANS.AA
1 : 25

https://ezeader.myportfolio.com/ezequiel-ader

Consultant	Consultant
Address	Address
Address	Address
Phone	Phone
Fax	Fax
e-mail	e-mail

Consultant	Consultant
Address	Address
Address	Address
Phone	Phone
Fax	Fax
e-mail	e-mail

No.	Description	Date

Angel Luis Brusca

CASA ANGEL


CORTE BB

Project number	0001
Date	18 de Agosto, 2025
Drawn by	ADER
Checked by	Checker

IS.0C02

Scale	1 : 25

10/9/2025 12:15:13 PM

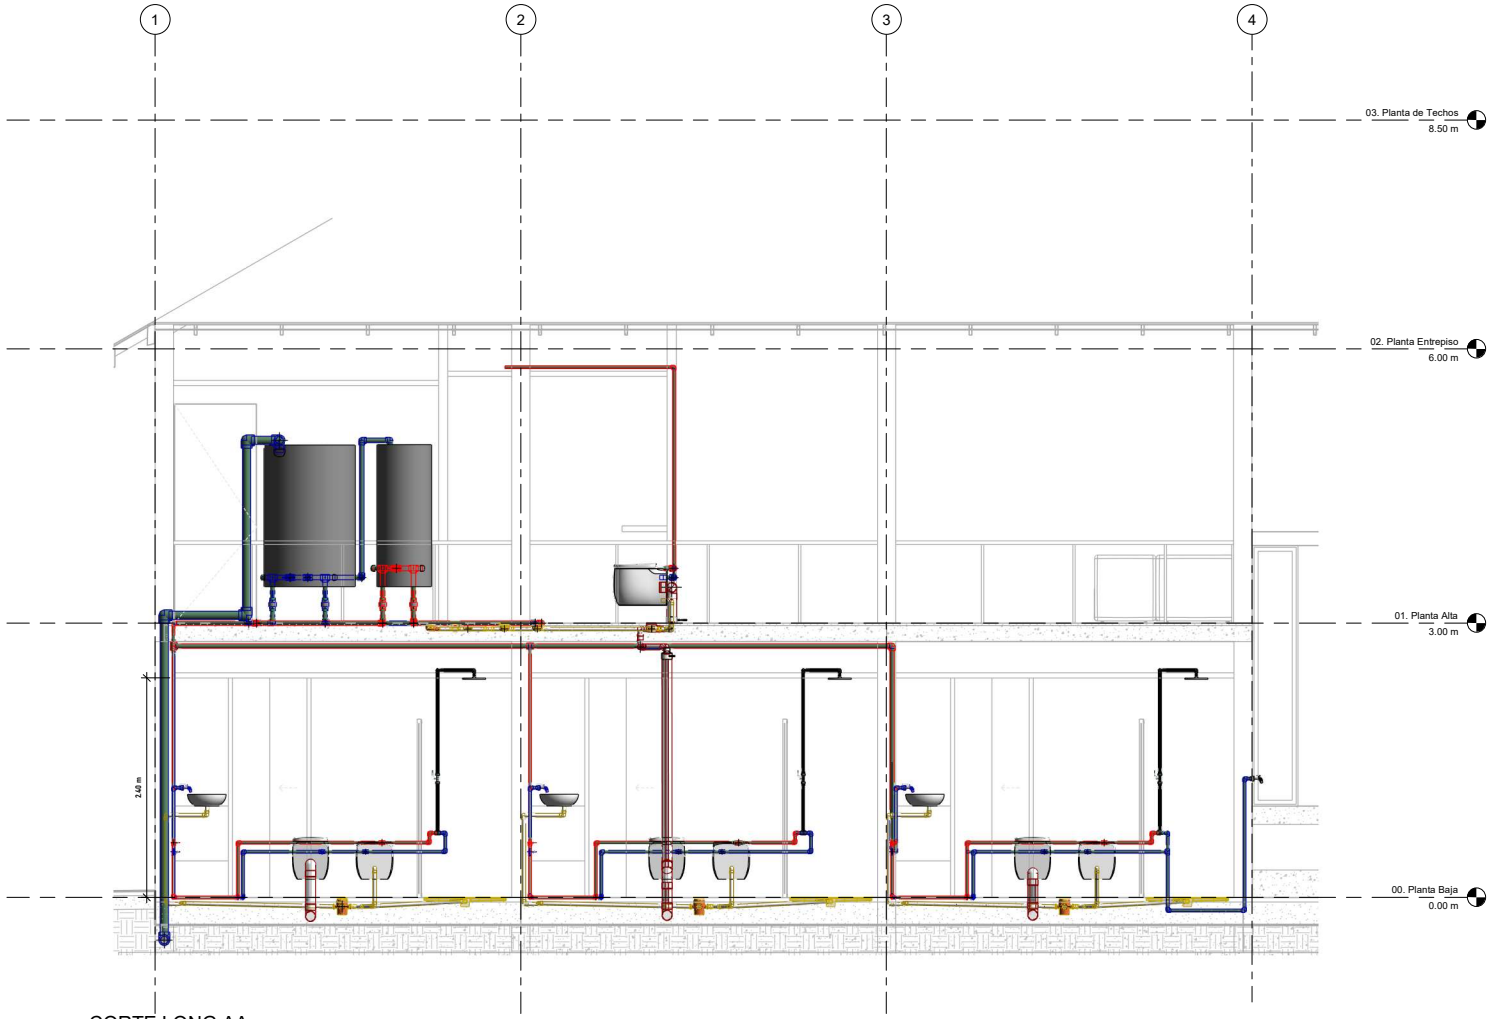

1 CORTE LONG.AA
1 : 25

https://ezeader.myportfolio.com/ezequiel-ader

Consultant	Consultant
Address	Address
Address	Address
Phone	Phone
Fax	Fax
e-mail	e-mail

Consultant	Consultant
Address	Address
Address	Address
Phone	Phone
Fax	Fax
e-mail	e-mail

No.	Description	Date

Angel Luis Brusca

CASA ANGEL

CORTE CC

Project number	0001
Date	18 de Agosto, 2025
Drawn by	ADER
Checked by	Checker

IS.0C03

Scale	1 : 25

10/9/2025 12:15:15 PM