
CASA ÁNGEL · ESTRUCTURA · FICHA LO-PA-03


LO-PA-03 · 27,30 m² · Hº e 15 · Armadura: a definir por el calculista.

LO-PA-03 · planta 1:25


Sector: 01. Planta Alta

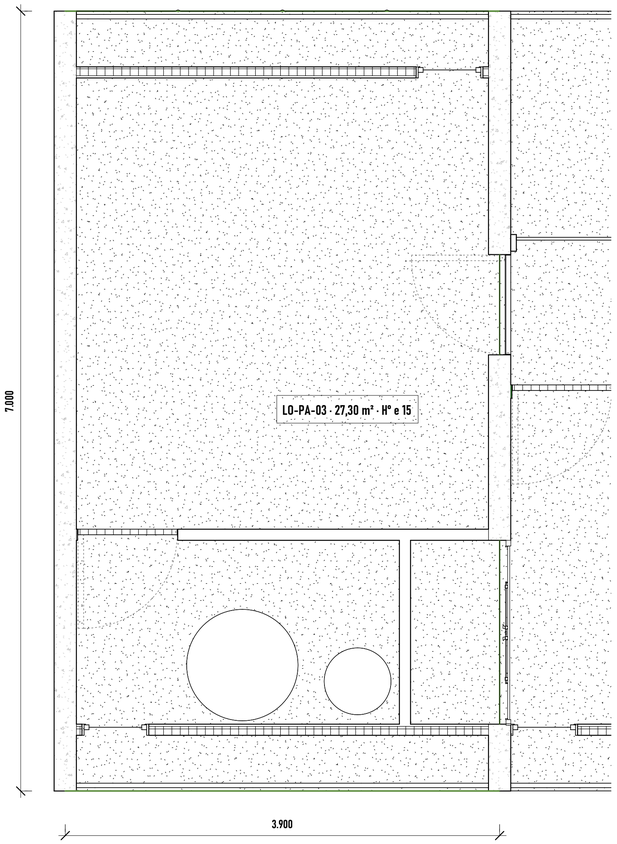


LO-PA-03 · corte A 1:25

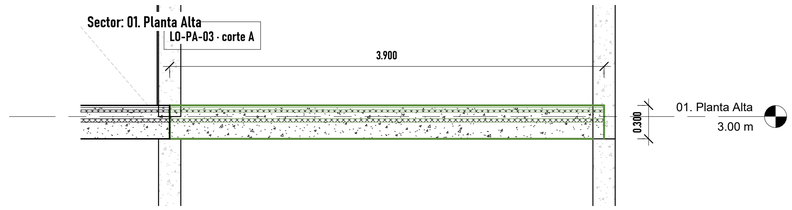

LO-PA-03 · corte B 1:30

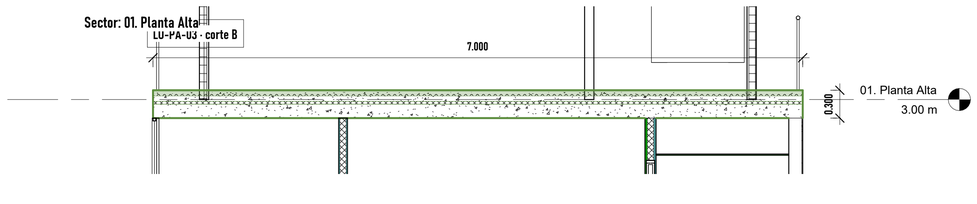

LO-PA-03 · axonométrica 1:60

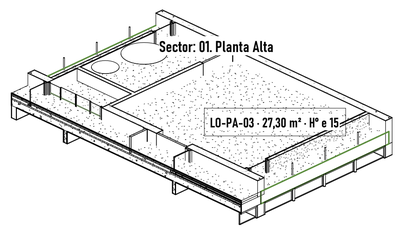

LO-PA-03 · 27,30 m² · Hº e 15
Losa con capa de hormigón 15 cm
Área 27,30 m² · Espesor total 0,30 m · Capa de Hº 0,15 m
Armadura: a definir por el calculista.

Ficha de elemento estructural: geometría nativa, cotas en metros (ancladas a extremos, no asociativas). Códigos como anotación. Armadura: a definir por el calculista.

https://ezeader.myportfolio.com/ezequiel-ader

Consultant
Address
Address
Phone
Fax
e-mail

Consultant
Address
Address
Phone
Fax
e-mail

Consultant
Address
Address
Phone
Fax
e-mail

Consultant
Address
Address
Phone
Fax
e-mail

No.	Description	Date

Angel Luis Brusca

CASA ANGEL

EST-F-LO-PA-03

Project number	0001
Date	18 de Agosto, 2025
Drawn by	Author
Checked by	Checker

Estructura · F-LO-PA-03

Scale: As indicated

10/23/2025 6:22 PM