

CASA ÁNGEL · ESTRUCTURA · FICHA VE-PA-01

VE-PA-01 · 8,51 · 20×455 · Armadura: a definir por el calculista.


VE-PA-01 · planta 1:30

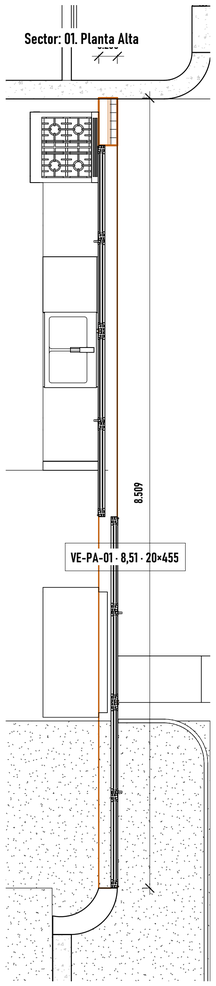


VE-PA-01 · vista (alzado) 1:40

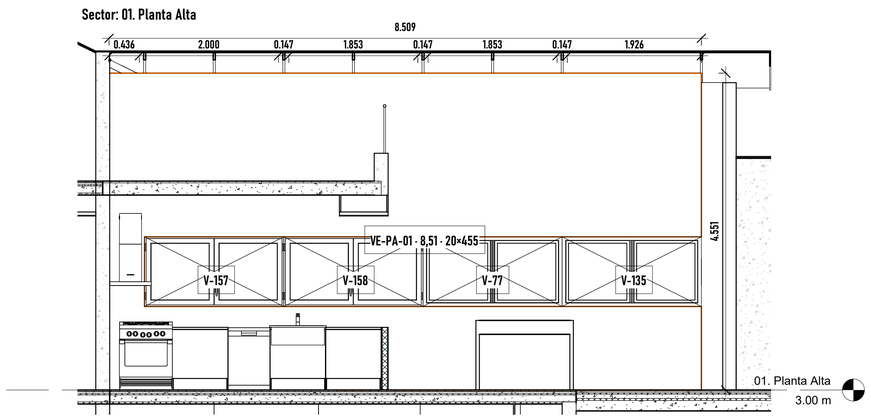

VE-PA-01 · corte 1:40

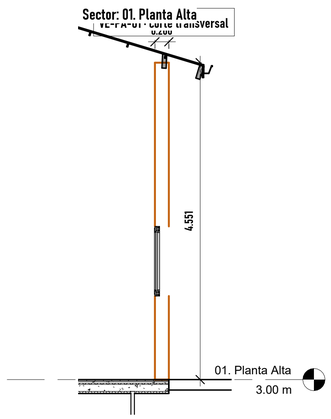

VE-PA-01 · axonométrica 1:60

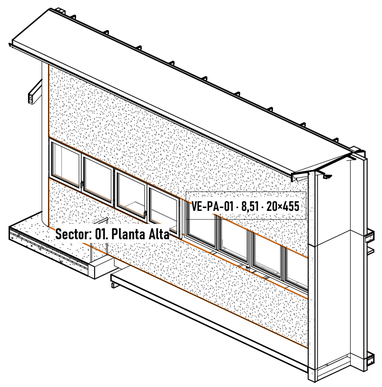

VE-PA-01 · 8,51 · 20×455
VIGA encuentro 2 techos, revestimiento fachada (modelado como muro)
Largo 8,51 m · Alto 4,55 m · Espesor 0,20 m · Área 30,73 m² · Volumen 6,68 m³
Armadura: a definir por el calculista.

Ficha de elemento estructural: geometría nativa, cotas en metros (ancladas a extremos, no asociativas). Códigos como anotación. Armadura: a definir por el calculista.

https://ezeader.myportfolio.com/ezequiel-ader

Consultant
Address
Address
Phone
Fax
e-mail

Consultant
Address
Address
Phone
Fax
e-mail

Consultant
Address
Address
Phone
Fax
e-mail

Consultant
Address
Address
Phone
Fax
e-mail

No.	Description	Date

Angel Luis Brusca

CASA ANGEL

EST-F-VE-PA-01

Project number	0001
Date	18 de Agosto, 2025
Drawn by	Author
Checked by	Checker

Estructura · F-VE-PA-01

Scale: As indicated

10/23/2026 12:55:56 PM