
CASA ÁNGEL · ESTRUCTURA · CASOS DE REVISIÓN · 7/7


Caso 25, Caso 26, Caso 27

Caso 25 · Solape / unión inconsistente en elementos estruc 1:75

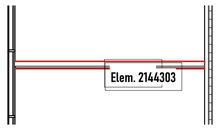


Observación: Highlighted walls overlap. One of them may be ignored when Revit finds room boundaries. Use Cut Geometry to em...
Propuesta: Revisar en planta y corte: unir o recortar (Cut/Join Geometry) solo después de validar cuál elemento manda; no...
Sin corrección geométrica (pendiente de aprobación).

Caso 26 · Solape / unión inconsistente en elementos estruc 1:75

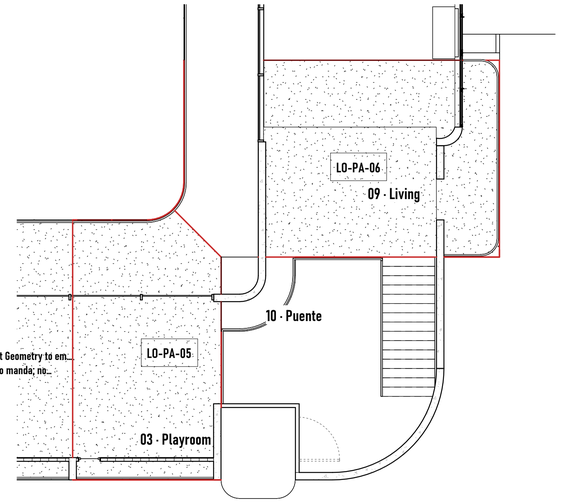

Observación: Highlighted floors overlap.
Propuesta: Revisar en planta y corte: unir o recortar (Cut/Join Geometry) solo después de validar cuál elemento manda; no...
Sin corrección geométrica (pendiente de aprobación).

Caso 27 · Solape / unión inconsistente en elementos estruc 1:75

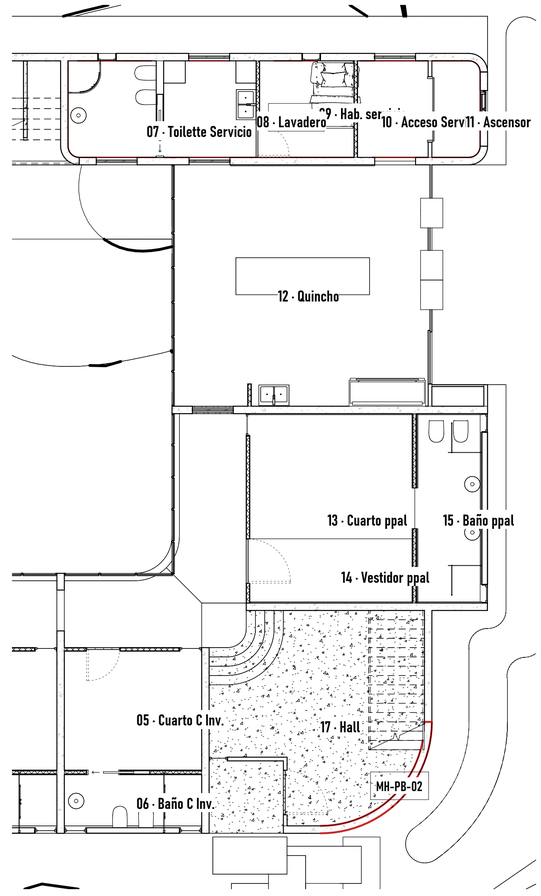

Observación: Highlighted elements are joined but do not intersect.
Propuesta: Revisar en planta y corte: unir o recortar (Cut/Join Geometry) solo después de validar cuál elemento manda; no...
Sin corrección geométrica (pendiente de aprobación).

Estructura: documentación sobre geometría nativa. Códigos MH/VE/LO/PL solo como anotación (no se escribieron en el modelo). Cotas en metros; largos y vanos anclados a extremos (no asociativos). Losas L01.00 de PA/PE: a confirmar.

https://ezeader.myportfolio.com/ezequiel-ader

Consultant
Address
Address
Phone
Fax
e-mail

Consultant
Address
Address
Phone
Fax
e-mail

Consultant
Address
Address
Phone
Fax
e-mail

Consultant
Address
Address
Phone
Fax
e-mail

No.	Description	Date

Angel Luis Brusca

CASA ANGEL

EST-REV-07

Project number	0001
Date	18 de Agosto, 2025
Drawn by	Author
Checked by	Checker

Estructura · REV-07

Scale 1 : 75

10/23/2026 6:27:04 PM