
CASA ÁNGEL · PARRILLA · PARRILLA DE OBRA A MEDIDA


Boca 1,50 · hogar +0,90 · campana de ladrillo refractario visto hasta el cielorraso · parrilla regulable + brasero · leñero

D-01a · Planta de la parrilla 1:20

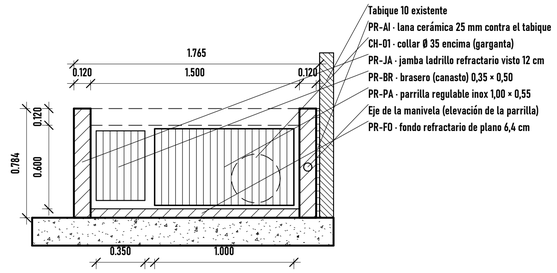


Planta cortada a +1,20 · trazo oculto: frente de campana y collar · cotas en m

D-01b · Vista frontal 1:25

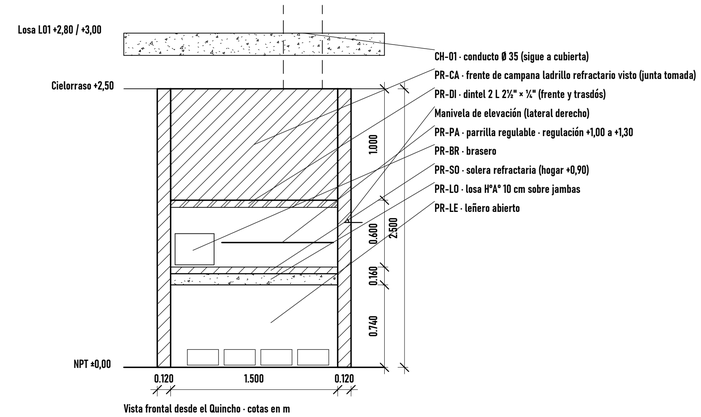

Vista frontal desde el Quincho · cotas en m

D-01c · Corte A-A 1:25

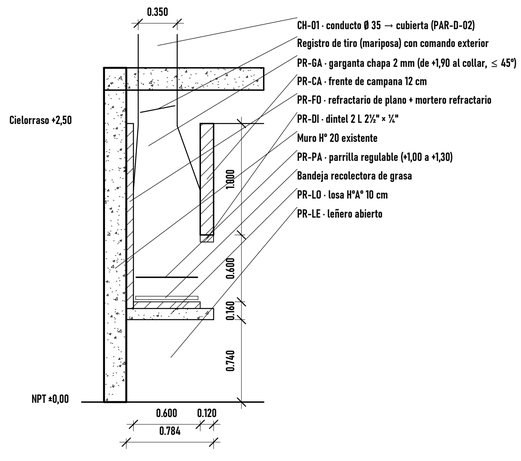

Corte A-A por el eje del conducto · cotas en m

Parrilla R34 (archivo de documentación con el modelo principal vinculado). Parrilla de obra a medida en el Quincho: boca 1,50 m, hogar a +0,90, campana refractaria hasta +2,50, conducto Ø 35 con sombrerete fijo. Modelada en el modelo principal (OK 26/10): reemplaza al K420B; cajón Durlock ampliado. Cotas en m.

https://ezeader.myportfolio.com/ezequiel-ader

Consultant
Address
Address
Phone
Fax
e-mail

Consultant
Address
Address
Phone
Fax
e-mail

Consultant
Address
Address
Phone
Fax
e-mail

Consultant
Address
Address
Phone
Fax
e-mail

No.	Description	Date

Angel Luis Brusca

CASA ANGEL

PAR-D-01

Project number	0001
Date	18 de Agosto, 2025
Drawn by	Author
Checked by	Checker

Parrilla · D-01

Scale: As indicated

10/30/2026 4:32:42 PM