# CASA ÁNGEL · CIELORRASOS · PROPUESTA DE CIELORRASOS · 02. PLANTA ENTREPISO

Cielorrasos propuestos · 02. Planta Entrepiso 1:20

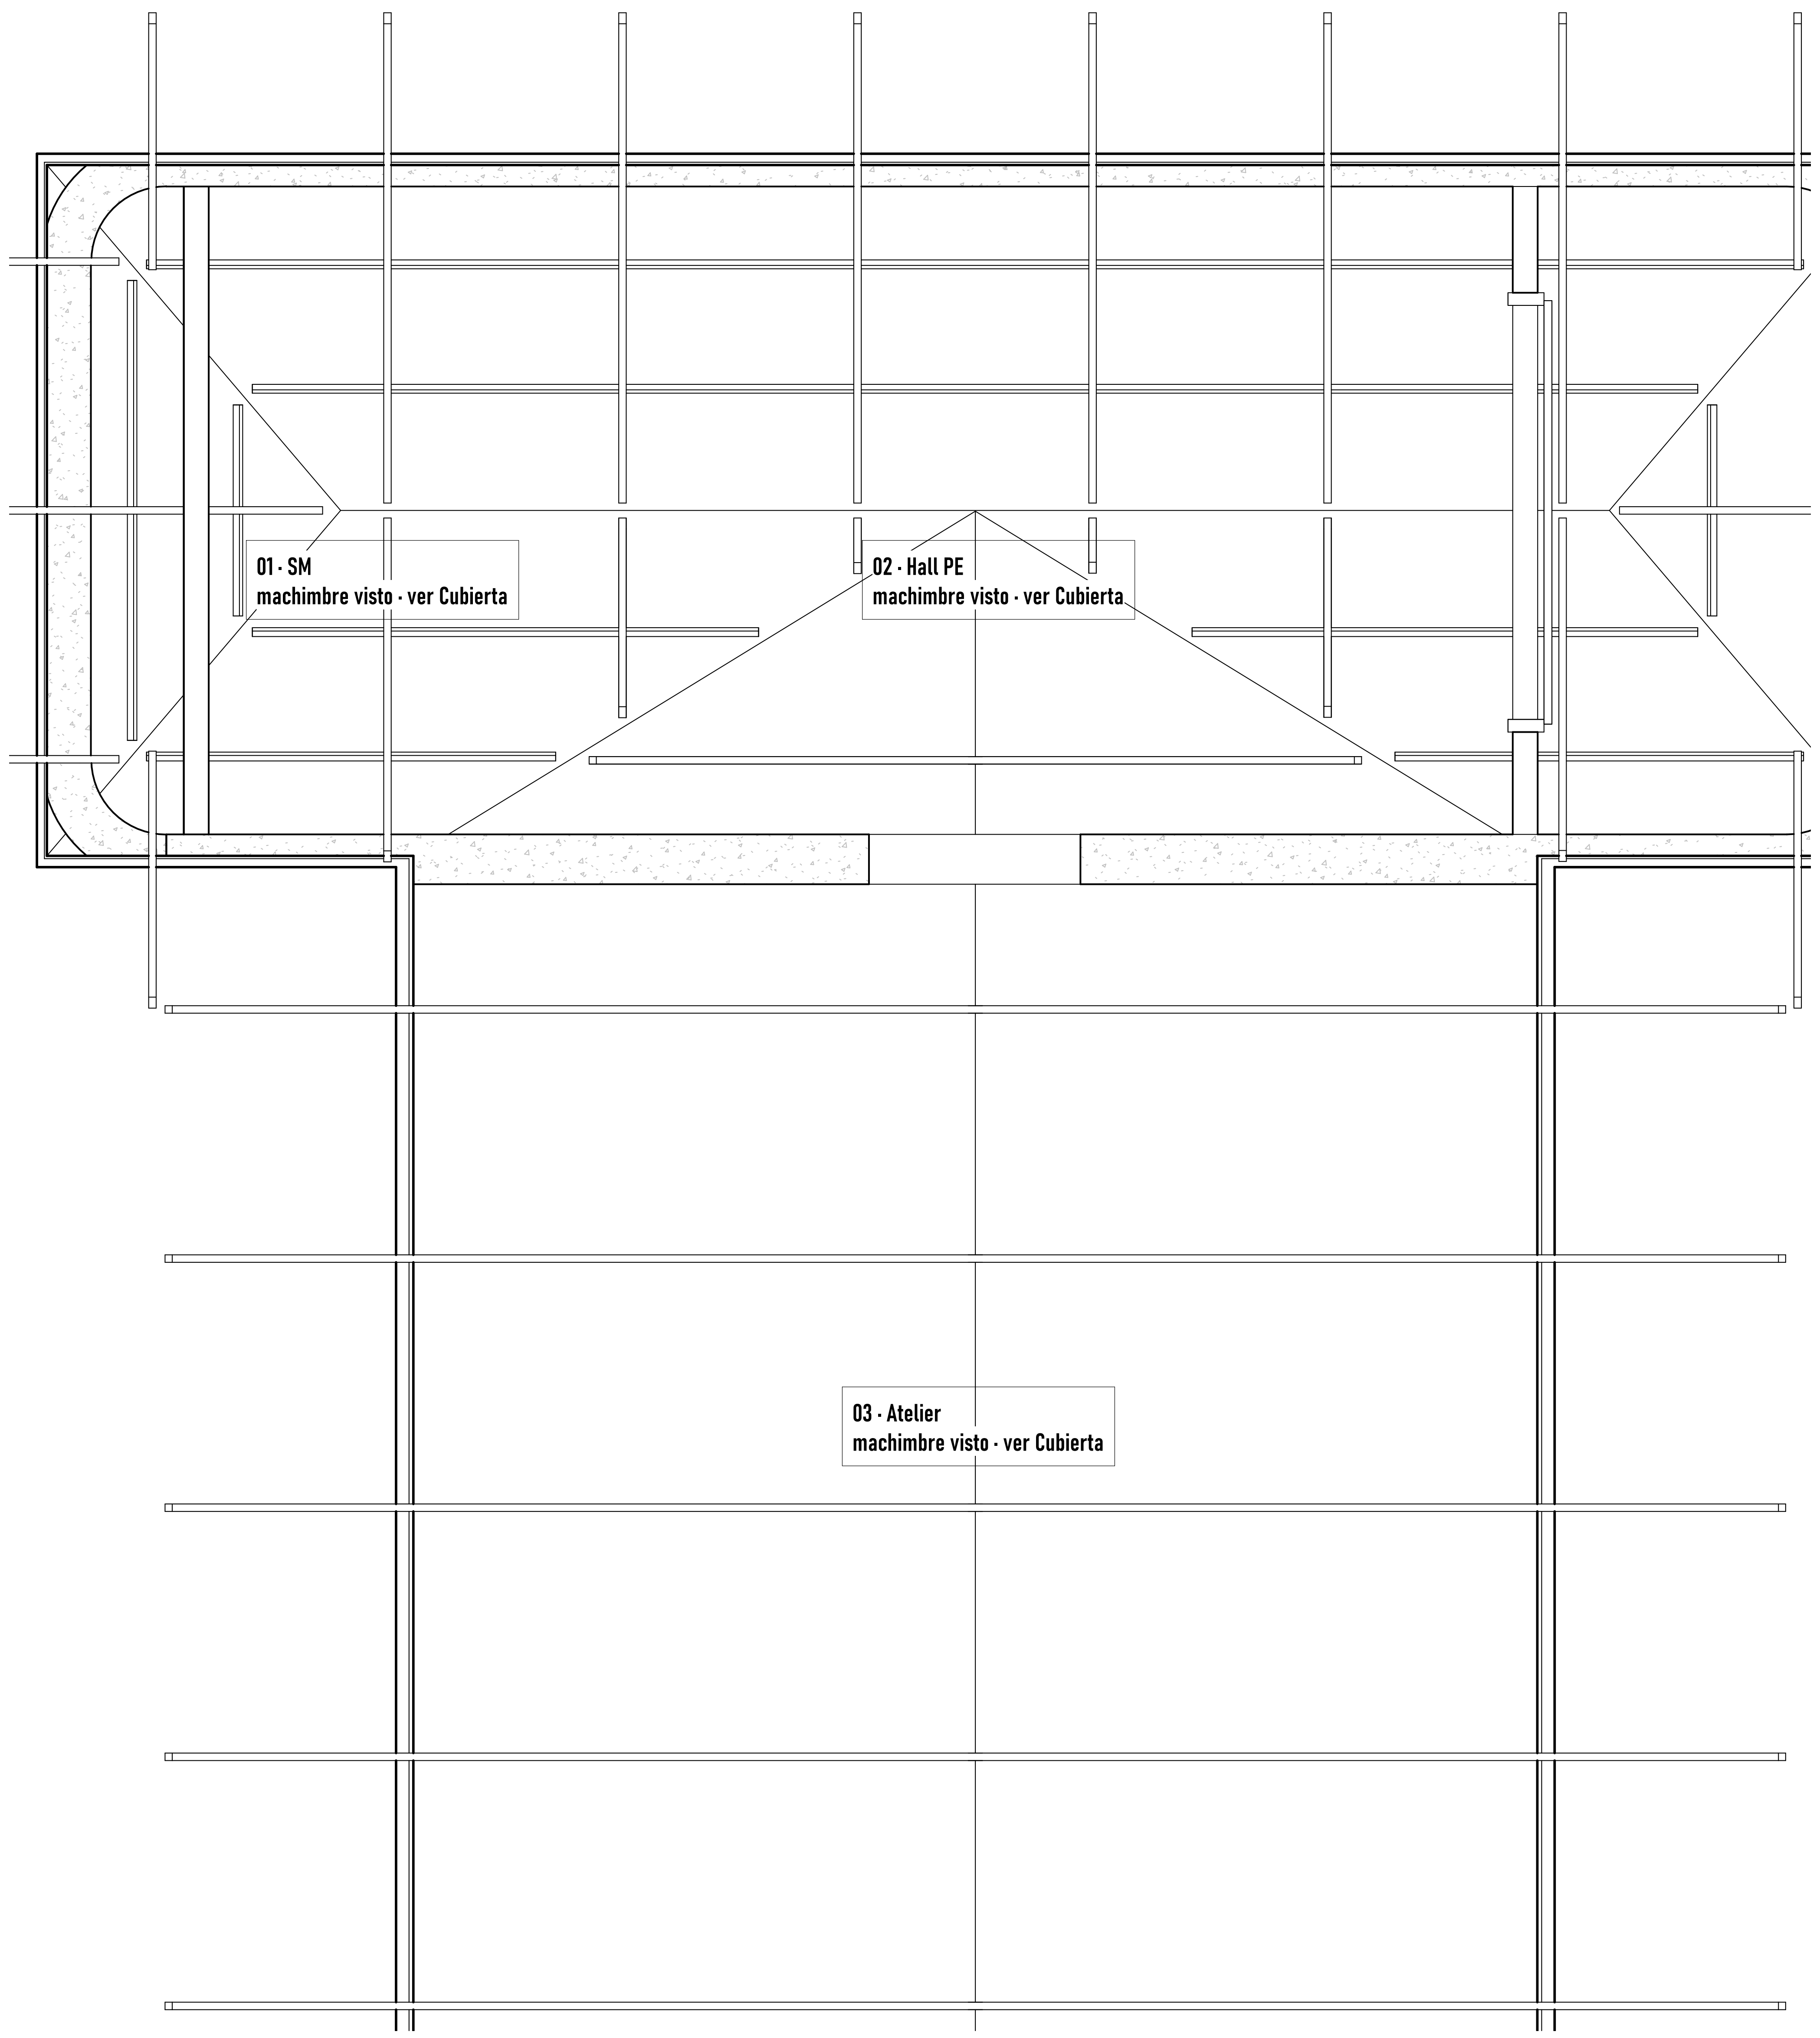
01 · SM
machimbre visto · ver Cubierta
02 · Hall PE
machimbre visto · ver Cubierta
03 · Atelier
machimbre visto · ver Cubierta

**PROPUESTA · RH 0,00 m² · ST 0,00 m² · propuesto 0,00 m² (rayado) · buña 0,00 ml**

PROPUESTA · Cielorrasos suspendidos de placa de yeso 12,5 sobre perfilería galvanizada: TC-01 RH en zonas húmedas, TC-02 ST en el resto; buña Z 15; tapas 60×60. Rayado: propuesto (CP); liso: existente. Bajo la cubierta de madera: machimbre visto (ver Cubierta). El modelo no se modificó.

https://ezeader.myportfolio.com/ezequiel-ader

Consultant
Address
Address
Phone
Fax
e-mail

Consultant
Address
Address
Phone
Fax
e-mail

Consultant
Address
Address
Phone
Fax
e-mail

Consultant
Address
Address
Phone
Fax
e-mail

| No. | Description | Date |
|---|---|---|

Angel Luis Brusca

CASA ANGEL

CIE-P-PE

| | |
|---|---|
| Project number | 0001 |
| Date | 18 de Agosto, 2025 |
| Drawn by | Author |
| Checked by | Checker |

Cielorrasos · propuesta PE

| | |
|---|---|
| Scale | 1 : 20 |

10/24/2026 10:55:16 AM