

CASA ÁNGEL · CUBIERTA · FICHA VC-13

VC-13 · 6,04 · 6×20 · Madera Kerto LVL


VC-13 · planta 1:20

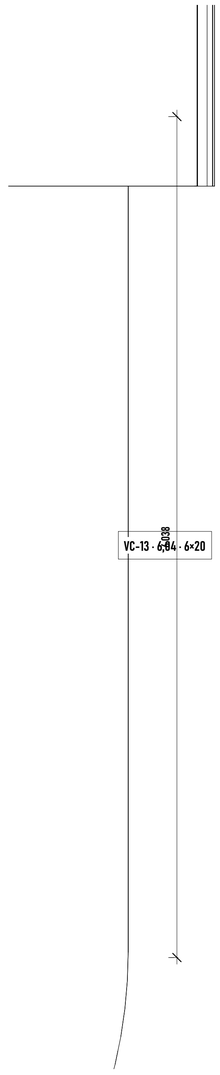


VC-13 · vista 1:20

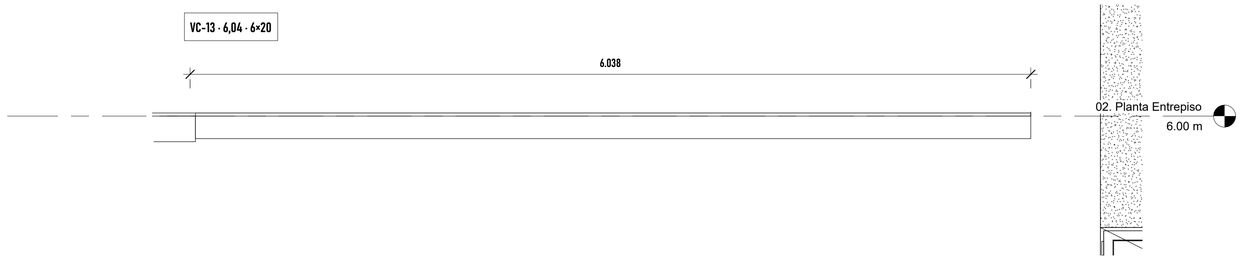

VC-13 · axonométrica 1:20

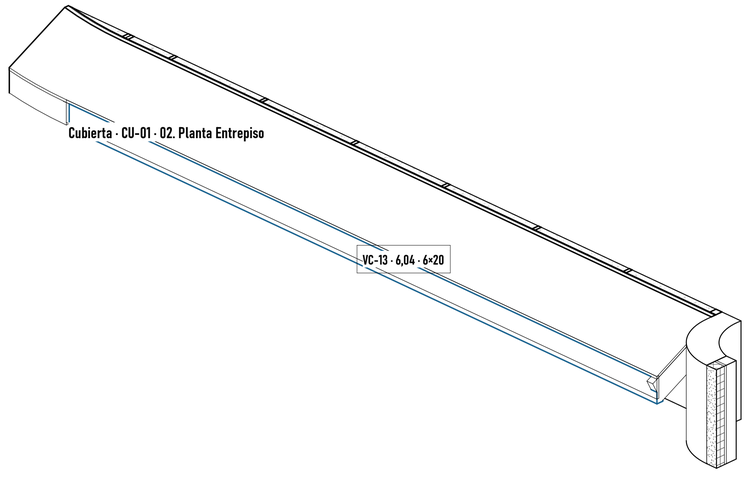

VC-13 · corte 1:20

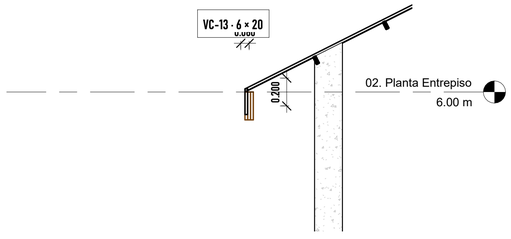

VC-13 · 6,04 · 6×20
Viga Cubierta 200mm x 60mm (Kerto LVL); sin nivel propio, nivel de referencia PE
Largo real 6,04 m · sección 6 × 20 cm · 0,071 m³ madera

Cubierta: geometría nativa; cotas en metros ancladas a extremos (no asociativas). Códigos CU/VC/VP/CR/FA/CA/AL como anotación. Membrana, aislación, cumbreras y bajadas: no modelado / a definir.

https://ezeader.myportfolio.com/ezequiel-ader

Consultant
Address
Address
Phone
Fax
e-mail

Consultant
Address
Address
Phone
Fax
e-mail

Consultant
Address
Address
Phone
Fax
e-mail

Consultant
Address
Address
Phone
Fax
e-mail

No.	Description	Date

Angel Luis Brusca

CASA ANGEL

CUB-F-VC-13

Project number	0001
Date	18 de Agosto, 2025
Drawn by	Author
Checked by	Checker

Cubierta · VC-13

Scale 1 : 20

10/23/2026 7:24:32 PM