

CASA ÁNGEL · ABERTURAS · 00. PLANTA BAJA · 14 VESTIDOR PPAL

Hoja 1 de 2 · 1 elementos: P-31

Planta del local · 14 · Vestidor ppal 1:25

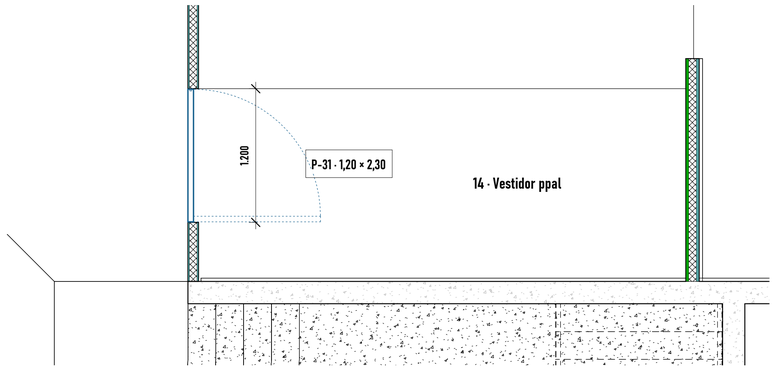

Axonométrica del local · 14 · Vestidor ppal 1:20

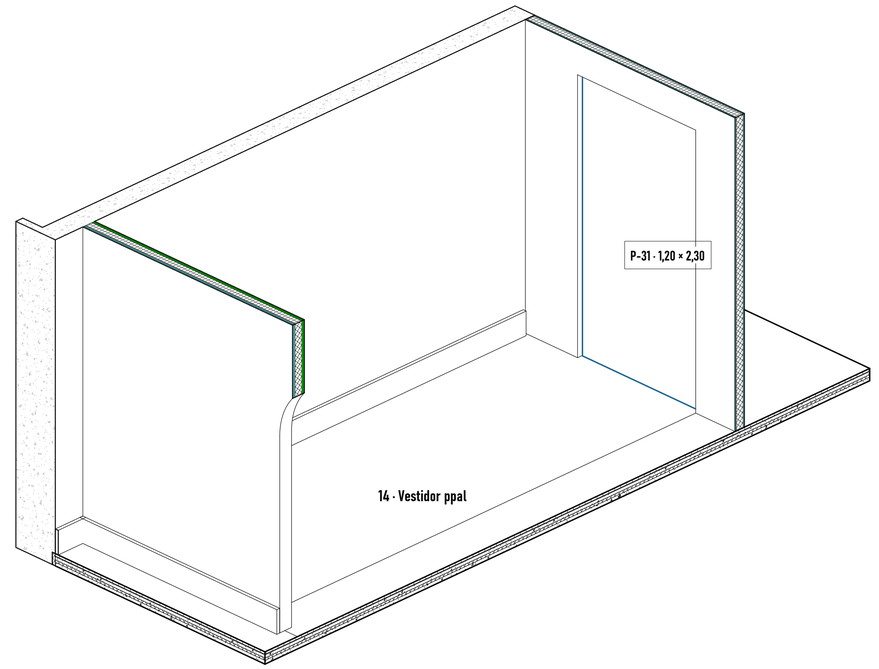

Cotas en metros (0.001 m) sobre geometría nativa. Cotas de muros cortina y cápsula del ascensor: referidas a ejes de grilla, extremos y centros de arcos (no asociativas, salvo radios). Alzados vistos desde el interior del local. Elementos compartidos entre locales: un solo cómputo por código.

https://ezeader.myportfolio.com/ezequiel-ader

Consultant Address Address Phone Fax e-mail	Consultant Address Address Phone Fax e-mail
Consultant Address Address Phone Fax e-mail	Consultant Address Address Phone Fax e-mail

No.	Description	Date

Angel Luis Brusca

CASA ANGEL

ABR-R4-PB-14

Project number	0001
Date	18 de Agosto, 2025
Drawn by	Author
Checked by	Checker

Vestidor ppal · ABR 1/2

Scale 1 : 25


10/23/2025 6:50 PM

CASA ÁNGEL · ABERTURAS · 00. PLANTA BAJA · 14 VESTIDOR PPAL

Hoja 2 de 2 · 1 elementos: P-31

P-31 · alzado interior 1:10

14 · Vestidor ppal

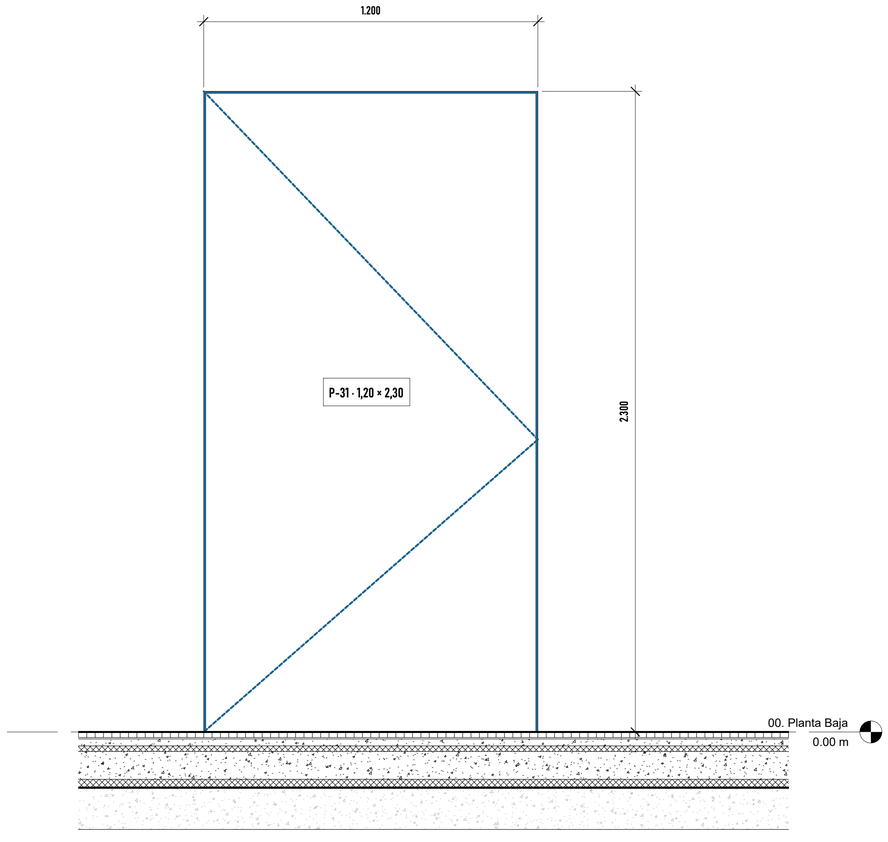

1.20 M · JALO_PUERTA ABATIBLE
Ancho 1.200 · Alto 2.300 · Antepecho 0.000 · Dintel 2.300 m
Muro 0.095 m
Compartida con: Pasillo (computar una vez)

Cotas en metros (0.001 m) sobre geometría nativa. Cotas de muros cortina y cápsula del ascensor: referidas a ejes de grilla, extremos y centros de arcos (no asociativas, salvo radios). Alzados vistos desde el interior del local. Elementos compartidos entre locales: un solo cómputo por código.

https://ezeader.myportfolio.com/ezequiel-ader

Consultant
Address
Address
Phone
Fax
e-mail

Consultant
Address
Address
Phone
Fax
e-mail

Consultant
Address
Address
Phone
Fax
e-mail

Consultant
Address
Address
Phone
Fax
e-mail

No.	Description	Date

Angel Luis Brusca

CASA ANGEL

ABR-R4-PB-14-2

Project number	0001
Date	18 de Agosto, 2025
Drawn by	Author
Checked by	Checker

Vestidor ppal · ABR 2/2

Scale 1 : 10

10/23/2025 6:50 PM