

CASA ÁNGEL · ABERTURAS · 00. PLANTA BAJA · 02 BAÑO A INV.

Hoja 1 de 2 · 3 elementos: V-127, V-132, P-60

Planta del local · 02 · Baño A Inv. 1:15

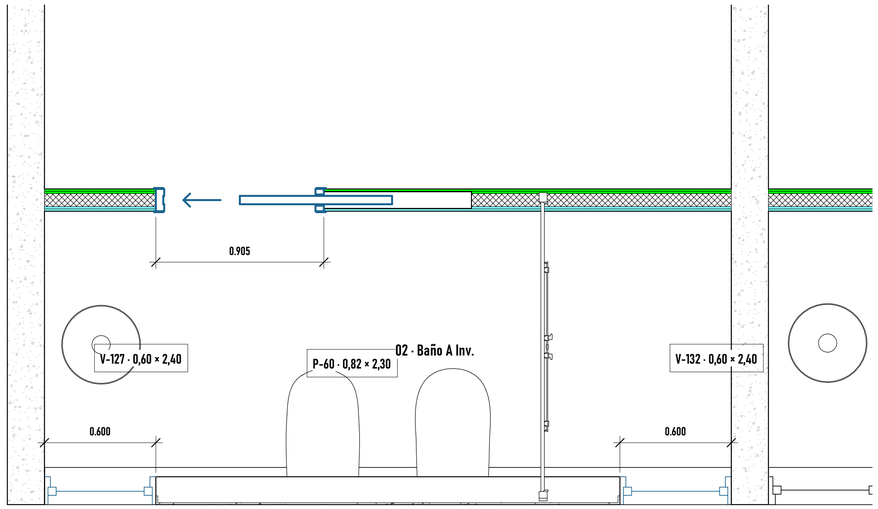

Axonométrica del local · 02 · Baño A Inv. 1:25

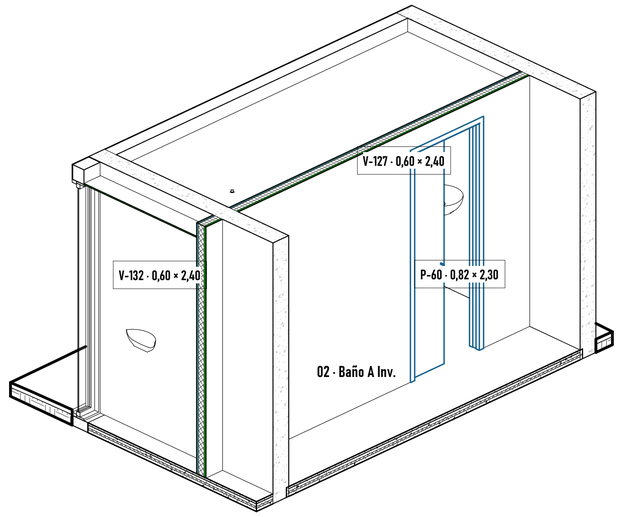

Cotas en metros (0.001 m) sobre geometría nativa. Cotas de muros cortina y cápsula del ascensor: referidas a ejes de grilla, extremos y centros de arcos (no asociativas, salvo radios). Alzados vistos desde el interior del local. Elementos compartidos entre locales: un solo cómputo por código.

https://ezeader.myportfolio.com/ezequiel-ader

Consultant
Address
Address
Phone
Fax
e-mail

Consultant
Address
Address
Phone
Fax
e-mail

Consultant
Address
Address
Phone
Fax
e-mail

Consultant
Address
Address
Phone
Fax
e-mail

No.	Description	Date

Angel Luis Brusca

CASA ANGEL

ABR-R4-PB-02

Project number	0001
Date	18 de Agosto, 2025
Drawn by	Author
Checked by	Checker

Baño A Inv. · ABR 1/2


Scale 1 : 15

10/23/2025 6:03 PM

CASA ÁNGEL · ABERTURAS · 00. PLANTA BAJA · 02 BAÑO A INV.


Hoja 2 de 2 · 3 elementos: V-127, V-132, P-60

V-127 · alzado interior 1:15

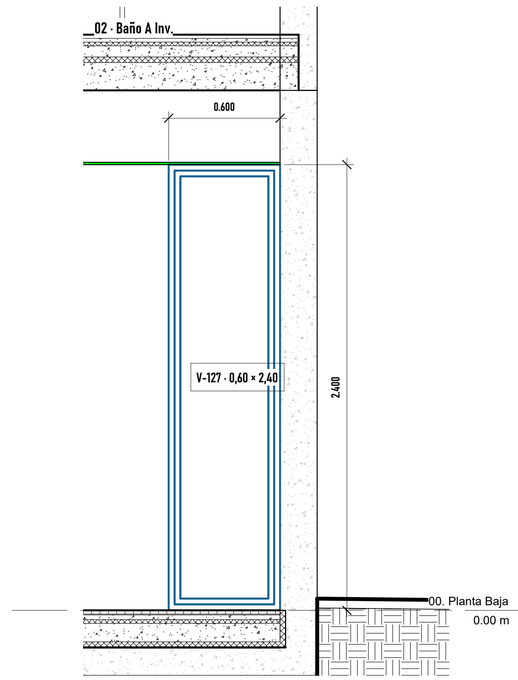


Ventana Cuartos (Muro a techo) · M_Fixed
Ancho 0.600 · Alto 2.400 · Antepecho 0.000 · Dintel 2.400 m
Tipo muro a techo: piso terminado a dintel 2.400 m (verificar con cielorraso)
Muro 0.150 m · Materiales: Glass, Sash

V-132 · alzado interior 1:15

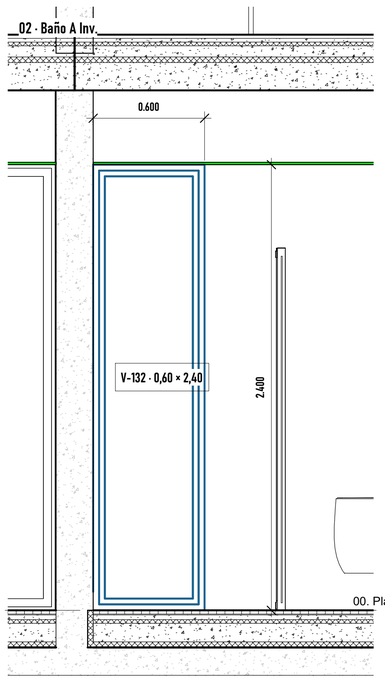

Ventana Cuartos (Muro a techo) · M_Fixed
Ancho 0.600 · Alto 2.400 · Antepecho 0.000 · Dintel 2.400 m
Tipo muro a techo: piso terminado a dintel 2.400 m (verificar con cielorraso)
Muro 0.150 m · Materiales: Glass, Sash

P-60 · alzado interior 1:15

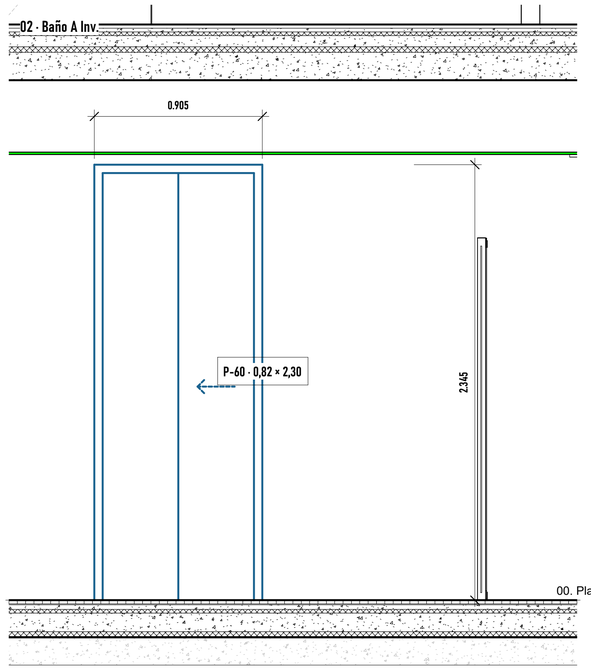

820 x 2000 mm · Puerta interior corredera
Hoja 0.820 × 2.300 · Vano 0.905 × 2.345 m
Muro 0.120 m · Materiales: Acero galvanizado, Acero inoxidable bruñido, Madera (roble), Premarco de pino
Compartida con: Cuarto A Inv. (computar una vez)

Cotas en metros (0.001 m) sobre geometría nativa. Cotas de muros cortina y cápsula del ascensor: referidas a ejes de grilla, extremos y centros de arcos (no asociativas, salvo radios). Alzados vistos desde el interior del local. Elementos compartidos entre locales: un solo cómputo por código.

https://ezeader.myportfolio.com/ezequiel-ader

Consultant
Address
Address
Phone
Fax
e-mail

Consultant
Address
Address
Phone
Fax
e-mail

Consultant
Address
Address
Phone
Fax
e-mail

Consultant
Address
Address
Phone
Fax
e-mail

No.	Description	Date

Angel Luis Brusca

CASA ANGEL

ABR-R4-PB-02-2

Project number	0001
Date	18 de Agosto, 2025
Drawn by	Author
Checked by	Checker

Baño A Inv. · ABR 2/2

Scale 1 : 15

10/23/2025 3:06:05 PM