

CASA ÁNGEL · ABERTURAS · 00. PLANTA BAJA · 15 BAÑO PPAL

Hoja 1 de 1 · 2 elementos: V-35, V-69


Planta del local · 15 · Baño ppal 1:20

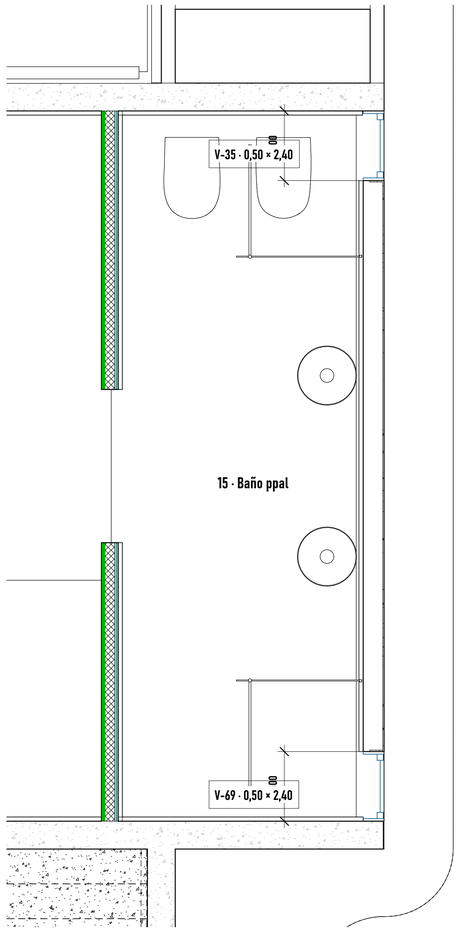

Axonométrica del local · 15 · Baño ppal 1:50

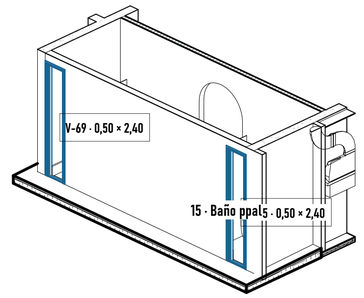


V-35 · alzado interior 1:20

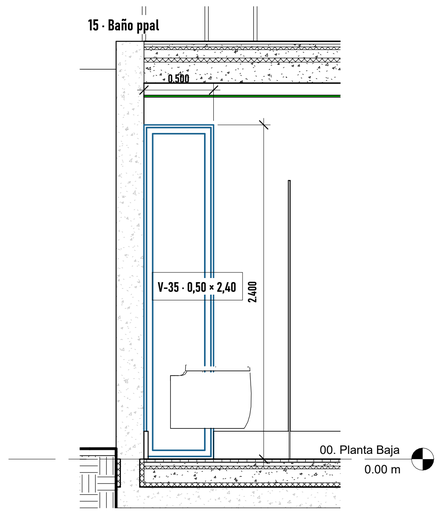

Ventana Baños (Muro a techo) · M_Fixed
Ancho 0.500 · Alto 2.400 · Antepecho 0.000 · Dintel 2.400 m
Tipo muro a techo: piso terminado a dintel 2.400 m (verificar con cielorraso)
Muro 0.150 m · Materiales: Glass, Sash

V-69 · alzado interior 1:20

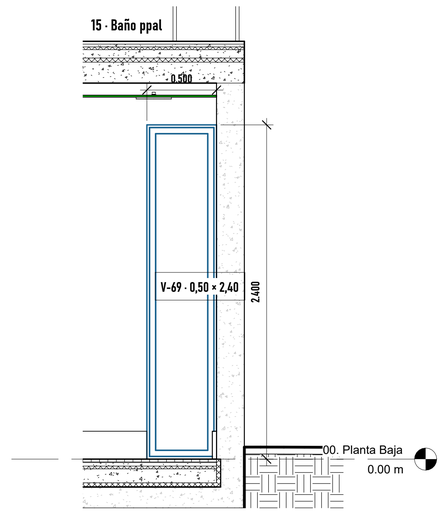

Ventana Baños (Muro a techo) · M_Fixed
Ancho 0.500 · Alto 2.400 · Antepecho 0.000 · Dintel 2.400 m
Tipo muro a techo: piso terminado a dintel 2.400 m (verificar con cielorraso)
Muro 0.150 m · Materiales: Glass, Sash

Cotas en metros (0.001 m) sobre geometría nativa. Cotas de muros cortina y cápsula del ascensor: referidas a ejes de grilla, extremos y centros de arcos (no asociativas, salvo radios). Alzados vistos desde el interior del local. Elementos compartidos entre locales: un solo cómputo por código.

https://ezeader.myportfolio.com/ezequiel-ader

Consultant
Address
Address
Phone
Fax
e-mail

Consultant
Address
Address
Phone
Fax
e-mail

Consultant
Address
Address
Phone
Fax
e-mail

Consultant
Address
Address
Phone
Fax
e-mail

No.	Description	Date

Angel Luis Brusca

CASA ANGEL

ABR-R4-PB-15

Project number	0001
Date	18 de Agosto, 2025
Drawn by	Author
Checked by	Checker

Baño ppal · ABR

Scale 1 : 20

10/23/2026 3:38:49 PM