

CASA ÁNGEL · ABERTURAS · 00. PLANTA BAJA · 07 TOILETTE SERVICIO

Hoja 1 de 2 · 2 elementos: V-150, P-93

Planta del local · 07 · Toilette Servicio 1:15

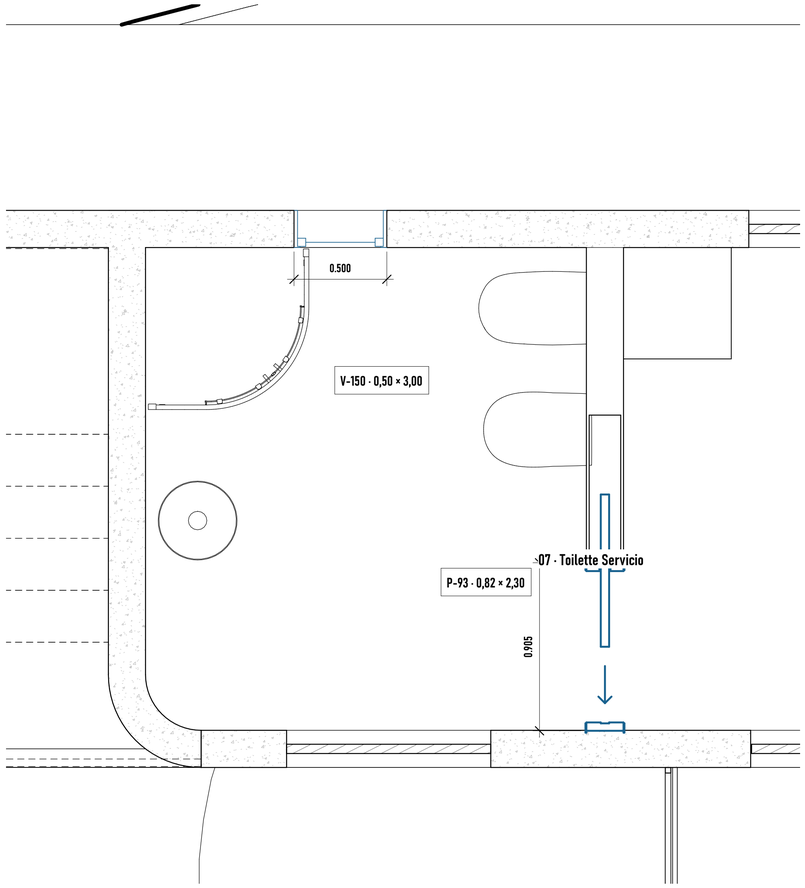

Axonométrica del local · 07 · Toilette Servicio 1:20

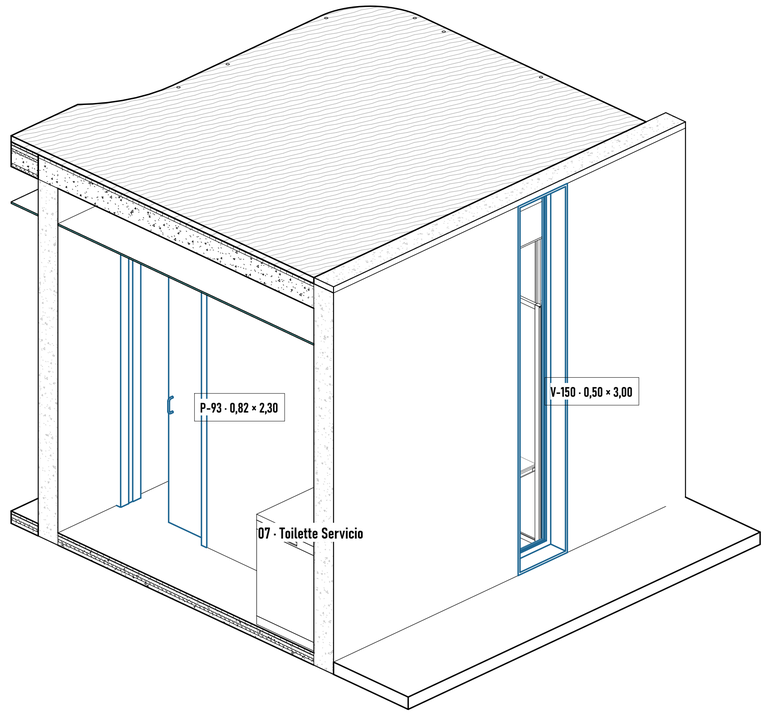

Cotas en metros (0.001 m) sobre geometría nativa. Cotas de muros cortina y cápsula del ascensor: referidas a ejes de grilla, extremos y centros de arcos (no asociativas, salvo radios). Alzados vistos desde el interior del local. Elementos compartidos entre locales: un solo cómputo por código.

https://ezeader.myportfolio.com/ezequiel-ader

Consultant
Address
Address
Phone
Fax
e-mail

Consultant
Address
Address
Phone
Fax
e-mail

Consultant
Address
Address
Phone
Fax
e-mail

Consultant
Address
Address
Phone
Fax
e-mail

No.	Description	Date

Angel Luis Brusca

CASA ANGEL

ABR-R4-PB-07

Project number	0001
Date	18 de Agosto, 2025
Drawn by	Author
Checked by	Checker

Toilette Servicio · ABR 1/2

Scale 1 : 15


10/23/2025 4:29 PM

CASA ÁNGEL · ABERTURAS · 00. PLANTA BAJA · 07 TOILETTE SERVICIO

Hoja 2 de 2 · 2 elementos: V-150, P-93


V-150 · alzado interior 1:15

07 · Toilette Servicio

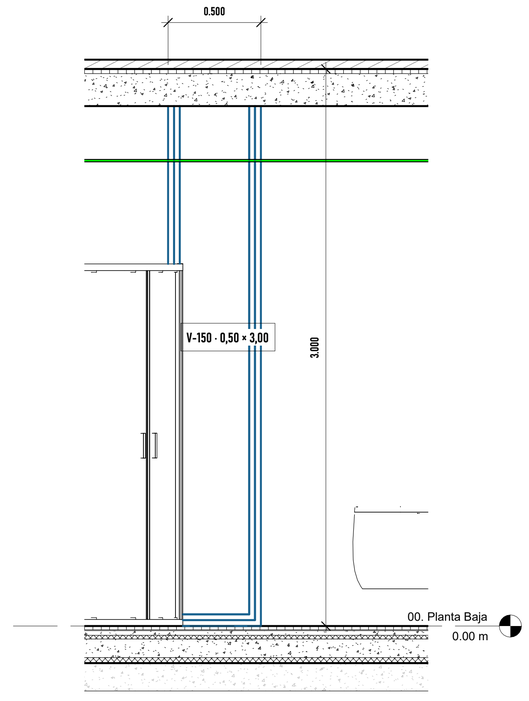

Ventanas Servicios · M_Fixed
Ancho 0.500 · Alto 3.000 · Antepecho 0.000 · Dintel 3.000 m
Muro 0.200 m · Materiales: Glass, Sash

P-93 · alzado interior 1:15

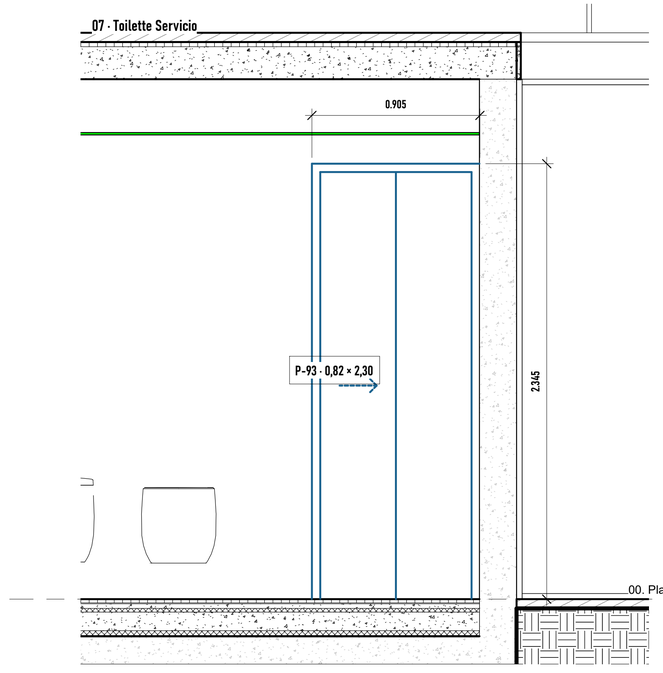

820 x 2000 mm · Puerta interior corredera
Hoja 0.820 × 2.300 · Vano 0.905 × 2.345 m
Muro 0.200 m · Materiales: Acero galvanizado, Acero inoxidable bruñido, Madera (roble), Premarco de pino
Compartida con: Lavadero (computar una vez)

Cotas en metros (0.001 m) sobre geometría nativa. Cotas de muros cortina y cápsula del ascensor: referidas a ejes de grilla, extremos y centros de arcos (no asociativas, salvo radios). Alzados vistos desde el interior del local. Elementos compartidos entre locales: un solo cómputo por código.

https://ezeader.myportfolio.com/ezequiel-ader

Consultant
Address
Address
Phone
Fax
e-mail

Consultant
Address
Address
Phone
Fax
e-mail

Consultant
Address
Address
Phone
Fax
e-mail

Consultant
Address
Address
Phone
Fax
e-mail

No.	Description	Date

Angel Luis Brusca

CASA ANGEL

ABR-R4-PB-07-2

Project number	0001
Date	18 de Agosto, 2025
Drawn by	Author
Checked by	Checker

Toilette Servicio · ABR-2/2

Scale 1 : 15

10/23/2025 4:30 PM