

CASA ÁNGEL · ABERTURAS · 01. PLANTA ALTA · 09 LIVING

Hoja 1 de 2 · 1 elementos: MC-612302

Planta del local · 09 · Living 1:40

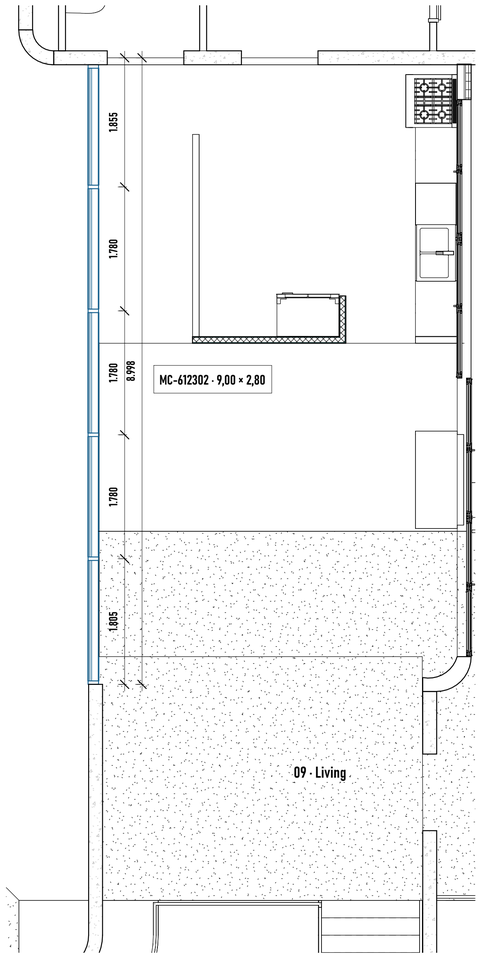

Axonométrica del local · 09 · Living 1:40

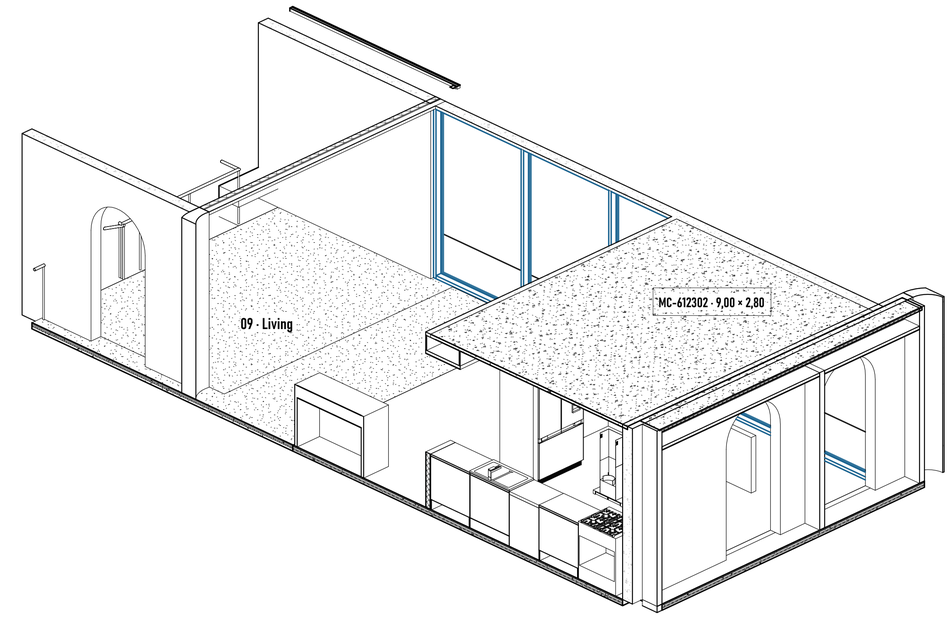

Cotas en metros (0.001 m) sobre geometría nativa. Cotas de muros cortina y cápsula del ascensor: referidas a ejes de grilla, extremos y centros de arcos (no asociativas, salvo radios). Alzados vistos desde el interior del local. Elementos compartidos entre locales: un solo cómputo por código.

https://ezeader.myportfolio.com/ezequiel-ader

Consultant Address Address Phone Fax e-mail	Consultant Address Address Phone Fax e-mail
Consultant Address Address Phone Fax e-mail	Consultant Address Address Phone Fax e-mail

No.	Description	Date

Angel Luis Brusca

CASA ANGEL

ABR-R4-PA-09

Project number	0001
Date	18 de Agosto, 2025
Drawn by	Author
Checked by	Checker

Living · ABR 1/2


Scale 1 : 40

10/23/2026 3:46:01 PM

CASA ÁNGEL · ABERTURAS · 01. PLANTA ALTA · 09 LIVING

Hoja 2 de 2 · 1 elementos: MC-612302

MC-612302 · alzado interior 1:20

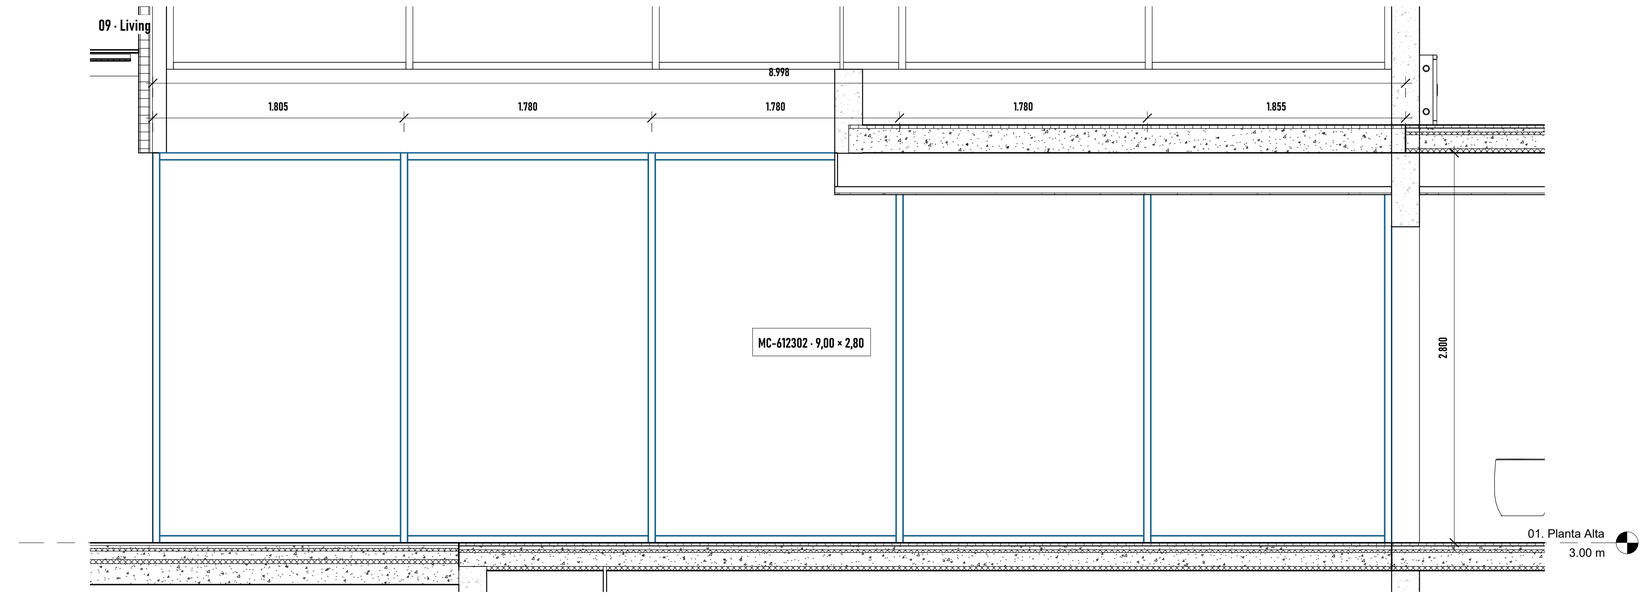

Muro cortina · Ventanales Patio · 5 paneles / 16 montantes
Largo 8.998 · Alto 2.800 · Arranque +0.000 · Superior +2.800 m
Muro 0.025 m
Compartida con: Cocina (computar una vez)

Cotas en metros (0.001 m) sobre geometría nativa. Cotas de muros cortina y cápsula del ascensor: referidas a ejes de grilla, extremos y centros de arcos (no asociativas, salvo radios). Alzados vistos desde el interior del local. Elementos compartidos entre locales: un solo cómputo por código.

https://ezeader.myportfolio.com/ezequiel-ader

Consultant
Address
Address
Phone
Fax
e-mail

Consultant
Address
Address
Phone
Fax
e-mail

Consultant
Address
Address
Phone
Fax
e-mail

Consultant
Address
Address
Phone
Fax
e-mail

No.	Description	Date

Angel Luis Brusca

CASA ANGEL

ABR-R4-PA-09-2

Project number	0001
Date	18 de Agosto, 2025
Drawn by	Author
Checked by	Checker

Living · ABR 2/2

Scale 1 : 20

10/23/2026 3:46:01 PM