
CASA ÁNGEL · EQUIPAMIENTO FIJO · PLANTA · 00. PLANTA BAJA

Equipamiento fijo · 00. Planta Baja 1:60

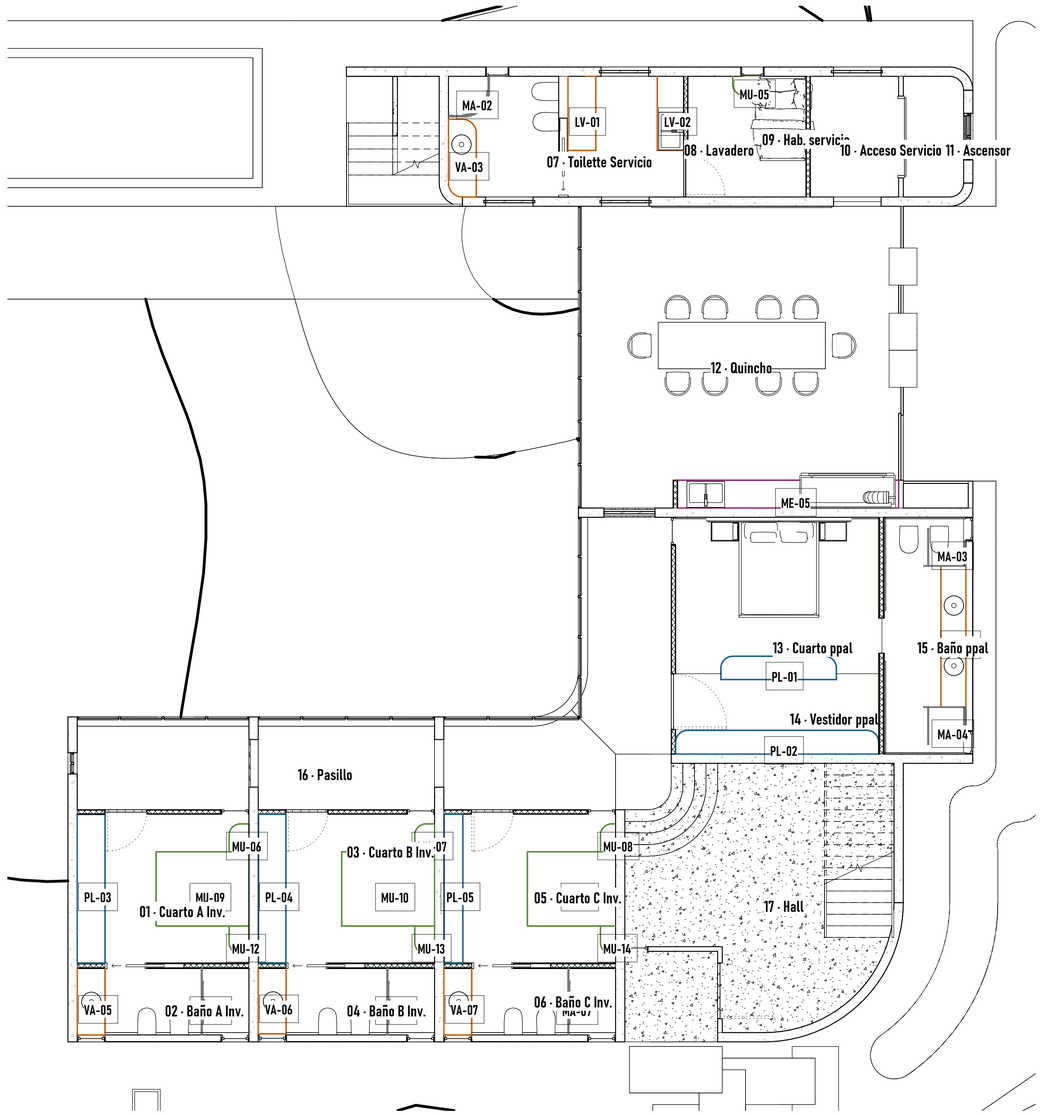

29 elementos fijos · PL 5 · MU 10 · VA 5 · ME 1 · LV 2 · MA 6

Equipamiento fijo: geometría nativa (familias in situ de carpintería, mamparas y equipos). Medidas de caja envolvente del modelo; cotas en metros (no asociativas). Herrajes, materiales de fabricación y despiece: a definir con el carpintero.

https://ezeader.myportfolio.com/ezequiel-ader

Consultant
Address
Address
Phone
Fax
e-mail

Consultant
Address
Address
Phone
Fax
e-mail

Consultant
Address
Address
Phone
Fax
e-mail

Consultant
Address
Address
Phone
Fax
e-mail

No.	Description	Date

Angel Luis Brusca

CASA ANGEL

EQ-01

Project number	0001
Date	18 de Agosto, 2025
Drawn by	Author
Checked by	Checker

Equipamiento · 01

Scale 1 : 60

10/23/2026 11:19:17 PM