

CASA ÁNGEL · ALBAÑILERÍA · FICHA TM-05 · MURO FACHADA EJE

TM-05 · muro de fachada (eje) · 34,59 m²


TM-05 · corte de muro 1:5

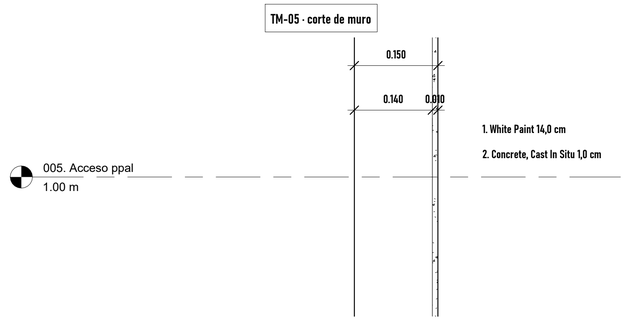


TM-05 · planta (00. Planta Baja) 1:150

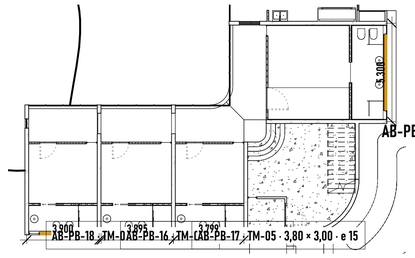

AB-PB-15 · axonométrica 1:30

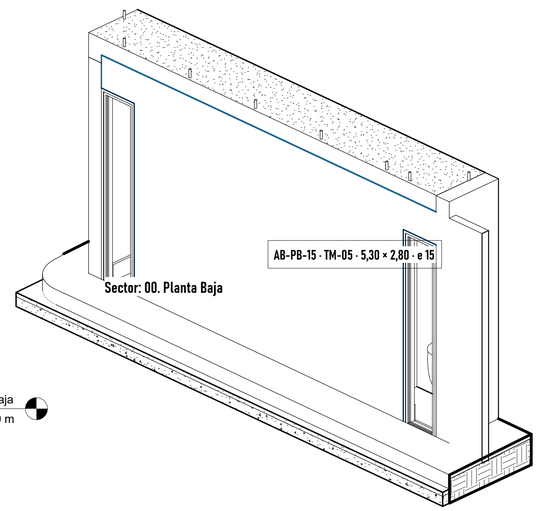

AB-PB-15 · vista 1:30

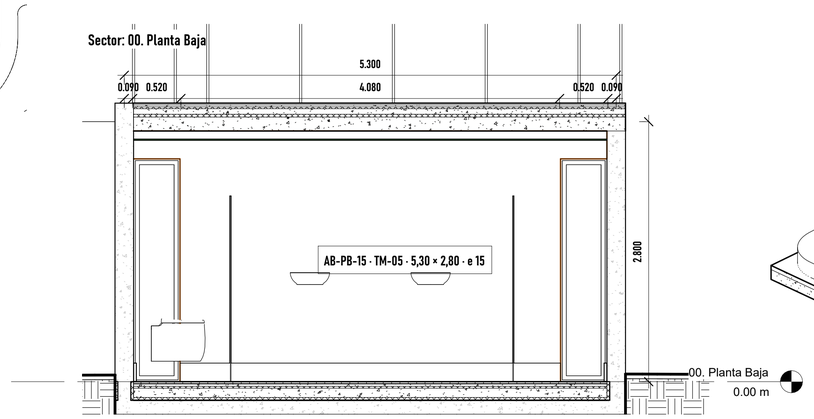

TM-05 · muro de fachada (eje) · 34,59 m²
Capas: pintura (genérico) 14 / hormigón 1 cm · espesor 15,00 cm
4 muros · 16,89 ml · 34,59 m² · 5,11 m³
Muros: AB-PB-15, AB-PB-18, AB-PB-16, AB-PB-17

Albañilería: muros y tabiques no estructurales del modelo (los de hormigón están en Estructura). Cotas en metros (no asociativas). Códigos TM/AB como anotación. Composición genérica en mampostería: a definir.

https://ezeader.myportfolio.com/ezequiel-ader

Consultant
Address
Address
Phone
Fax
e-mail

Consultant
Address
Address
Phone
Fax
e-mail

Consultant
Address
Address
Phone
Fax
e-mail

Consultant
Address
Address
Phone
Fax
e-mail

No.	Description	Date

Angel Luis Brusca

CASA ANGEL

ALB-F-TM-05

Project number	0001
Date	18 de Agosto, 2025
Drawn by	Author
Checked by	Checker

Albañilería · TM-05

Scale: As indicated

10/23/2026 8:11:12 PM