
CASA ÁNGEL · ALBAÑILERÍA · FICHA TM-08 · W112.AR 70.400 ST.RH 12.5


TM-08 · Durlock W112: 2 placas por cara (ST / RH), montante 70 · 52,72 m²

TM-08 · planta (00. Planta Baja) 1:75

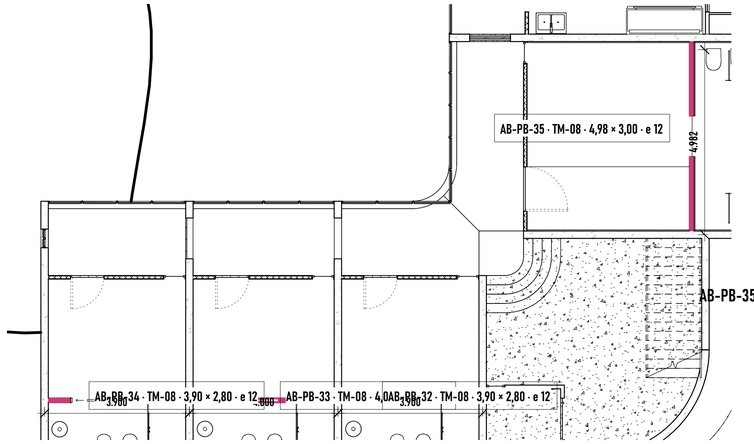


TM-08 · Durlock W112: 2 placas por cara (ST / RH), montante 70 · 52,72 m²
Capas: placa Knauf ST 12,5 1,2 / placa Knauf ST 12,5 1,2 / montantes y soleras 70 7 / placa Knauf RH 12,5 1,2 / placa Knauf RH 12,5 1,2 cm · espesor 12,00 cm
6 muros · 21,46 ml · 52,72 m² · 5,82 m³
Muros: AB-PB-35, AB-PB-33, AB-PB-32, AB-PB-34, AB-PA-23, AB-PA-22


TM-08 · corte de muro 1:5

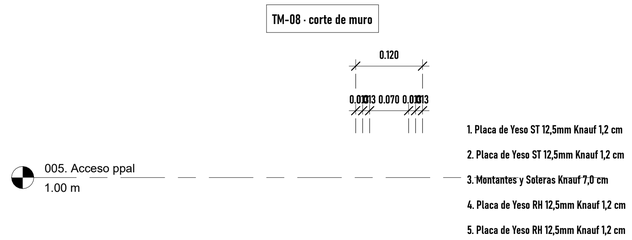

AB-PB-35 · vista 1:40

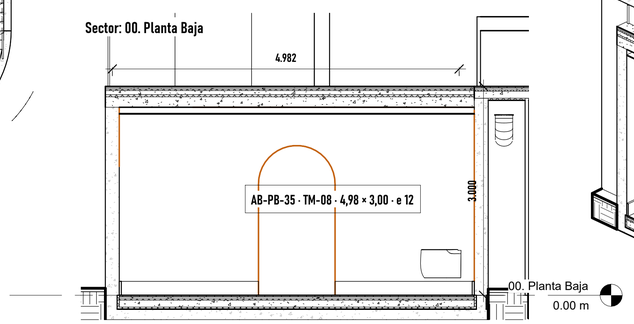

AB-PB-35 · axonométrica 1:40

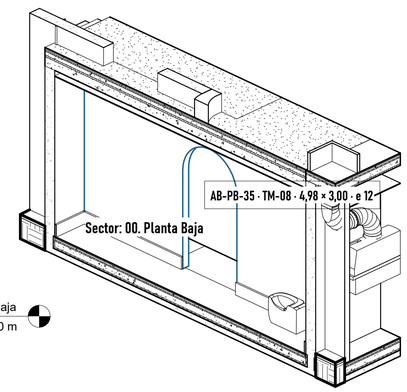

Albañilería: muros y tabiques no estructurales del modelo (los de hormigón están en Estructura). Cotas en metros (no asociativas). Códigos TM/AB como anotación. Composición genérica en mampostería: a definir.

https://ezeader.myportfolio.com/ezequiel-ader

Consultant
Address
Address
Phone
Fax
e-mail

Consultant
Address
Address
Phone
Fax
e-mail

Consultant
Address
Address
Phone
Fax
e-mail

Consultant
Address
Address
Phone
Fax
e-mail

No.	Description	Date

Angel Luis Brusca

CASA ANGEL

ALB-F-TM-08

Project number	0001
Date	18 de Agosto, 2025
Drawn by	Author
Checked by	Checker

Albañilería · TM-08

Scale: As indicated

10/23/2026 8:11:30 PM