
CASA ÁNGEL · REVESTIMIENTOS · PLANTA · 02. PLANTA ENTREPISO

Revestimientos · 02. Planta Entrepiso 1:25

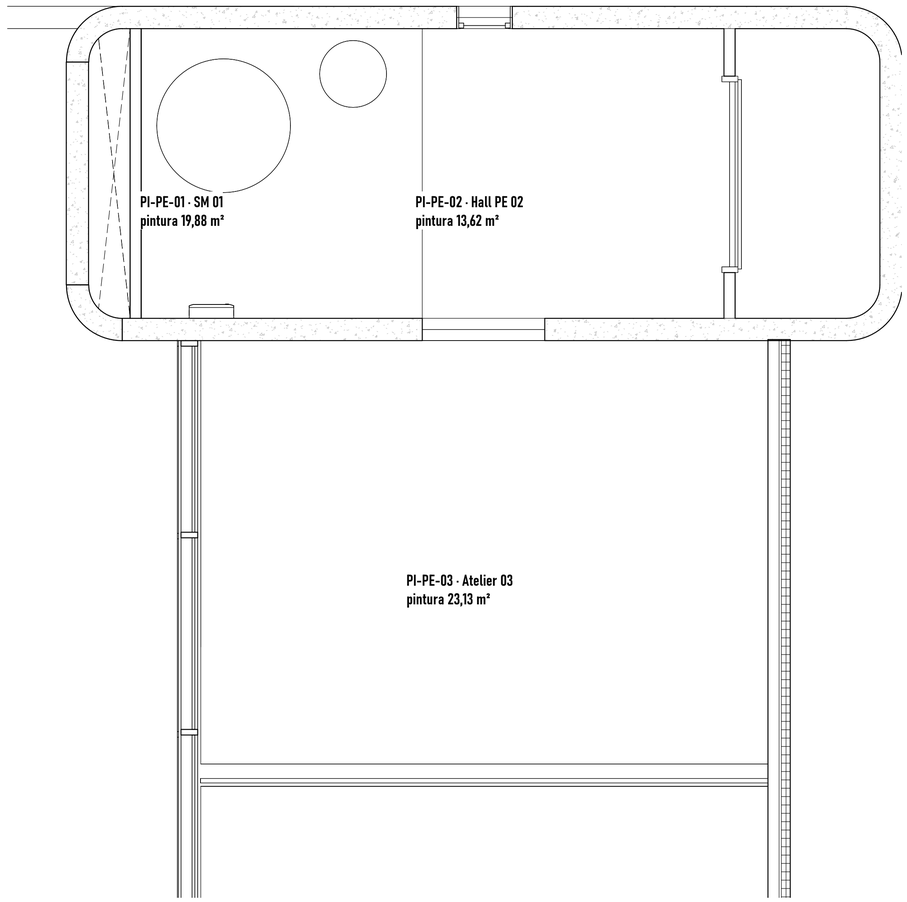

PROPUESTA A CONFIRMAR · revestimiento 0,00 m² en 0 locales · franjas 0,00 m² · pintura 56,63 m² · vanos descontados

PROPUESTA A CONFIRMAR · Revestimientos: baños y toilettes revestidos de 0,00 a 2,40 m; cocina y lavadero franja de 0,60 m sobre mesada (0,90 a 1,50 m); resto de muros pintado hasta 2,60 m; fachada de hormigón visto sin revestimiento. Superficies por cara terminada del local con vanos descontados. Material y formato a definir. El modelo no se modificó.

https://ezeader.myportfolio.com/ezequiel-ader

Consultant
Address
Address
Phone
Fax
e-mail

Consultant
Address
Address
Phone
Fax
e-mail

Consultant
Address
Address
Phone
Fax
e-mail

Consultant
Address
Address
Phone
Fax
e-mail

No.	Description	Date

Angel Luis Brusca

CASA ANGEL

RV-03

Project number	0001
Date	18 de Agosto, 2025
Drawn by	Author
Checked by	Checker

Revestimientos · 03

Scale 1 : 25

10/24/2026 2:17:16 AM