CASA ÁNGEL · REVESTIMIENTOS · FICHA · RV-PB-04 TOILETTE SERVICIO 07

Revestimiento 15,73 m² netos · h 2,40 · propuesta a confirmar

RV-PB-04 · planta de caras 1:15

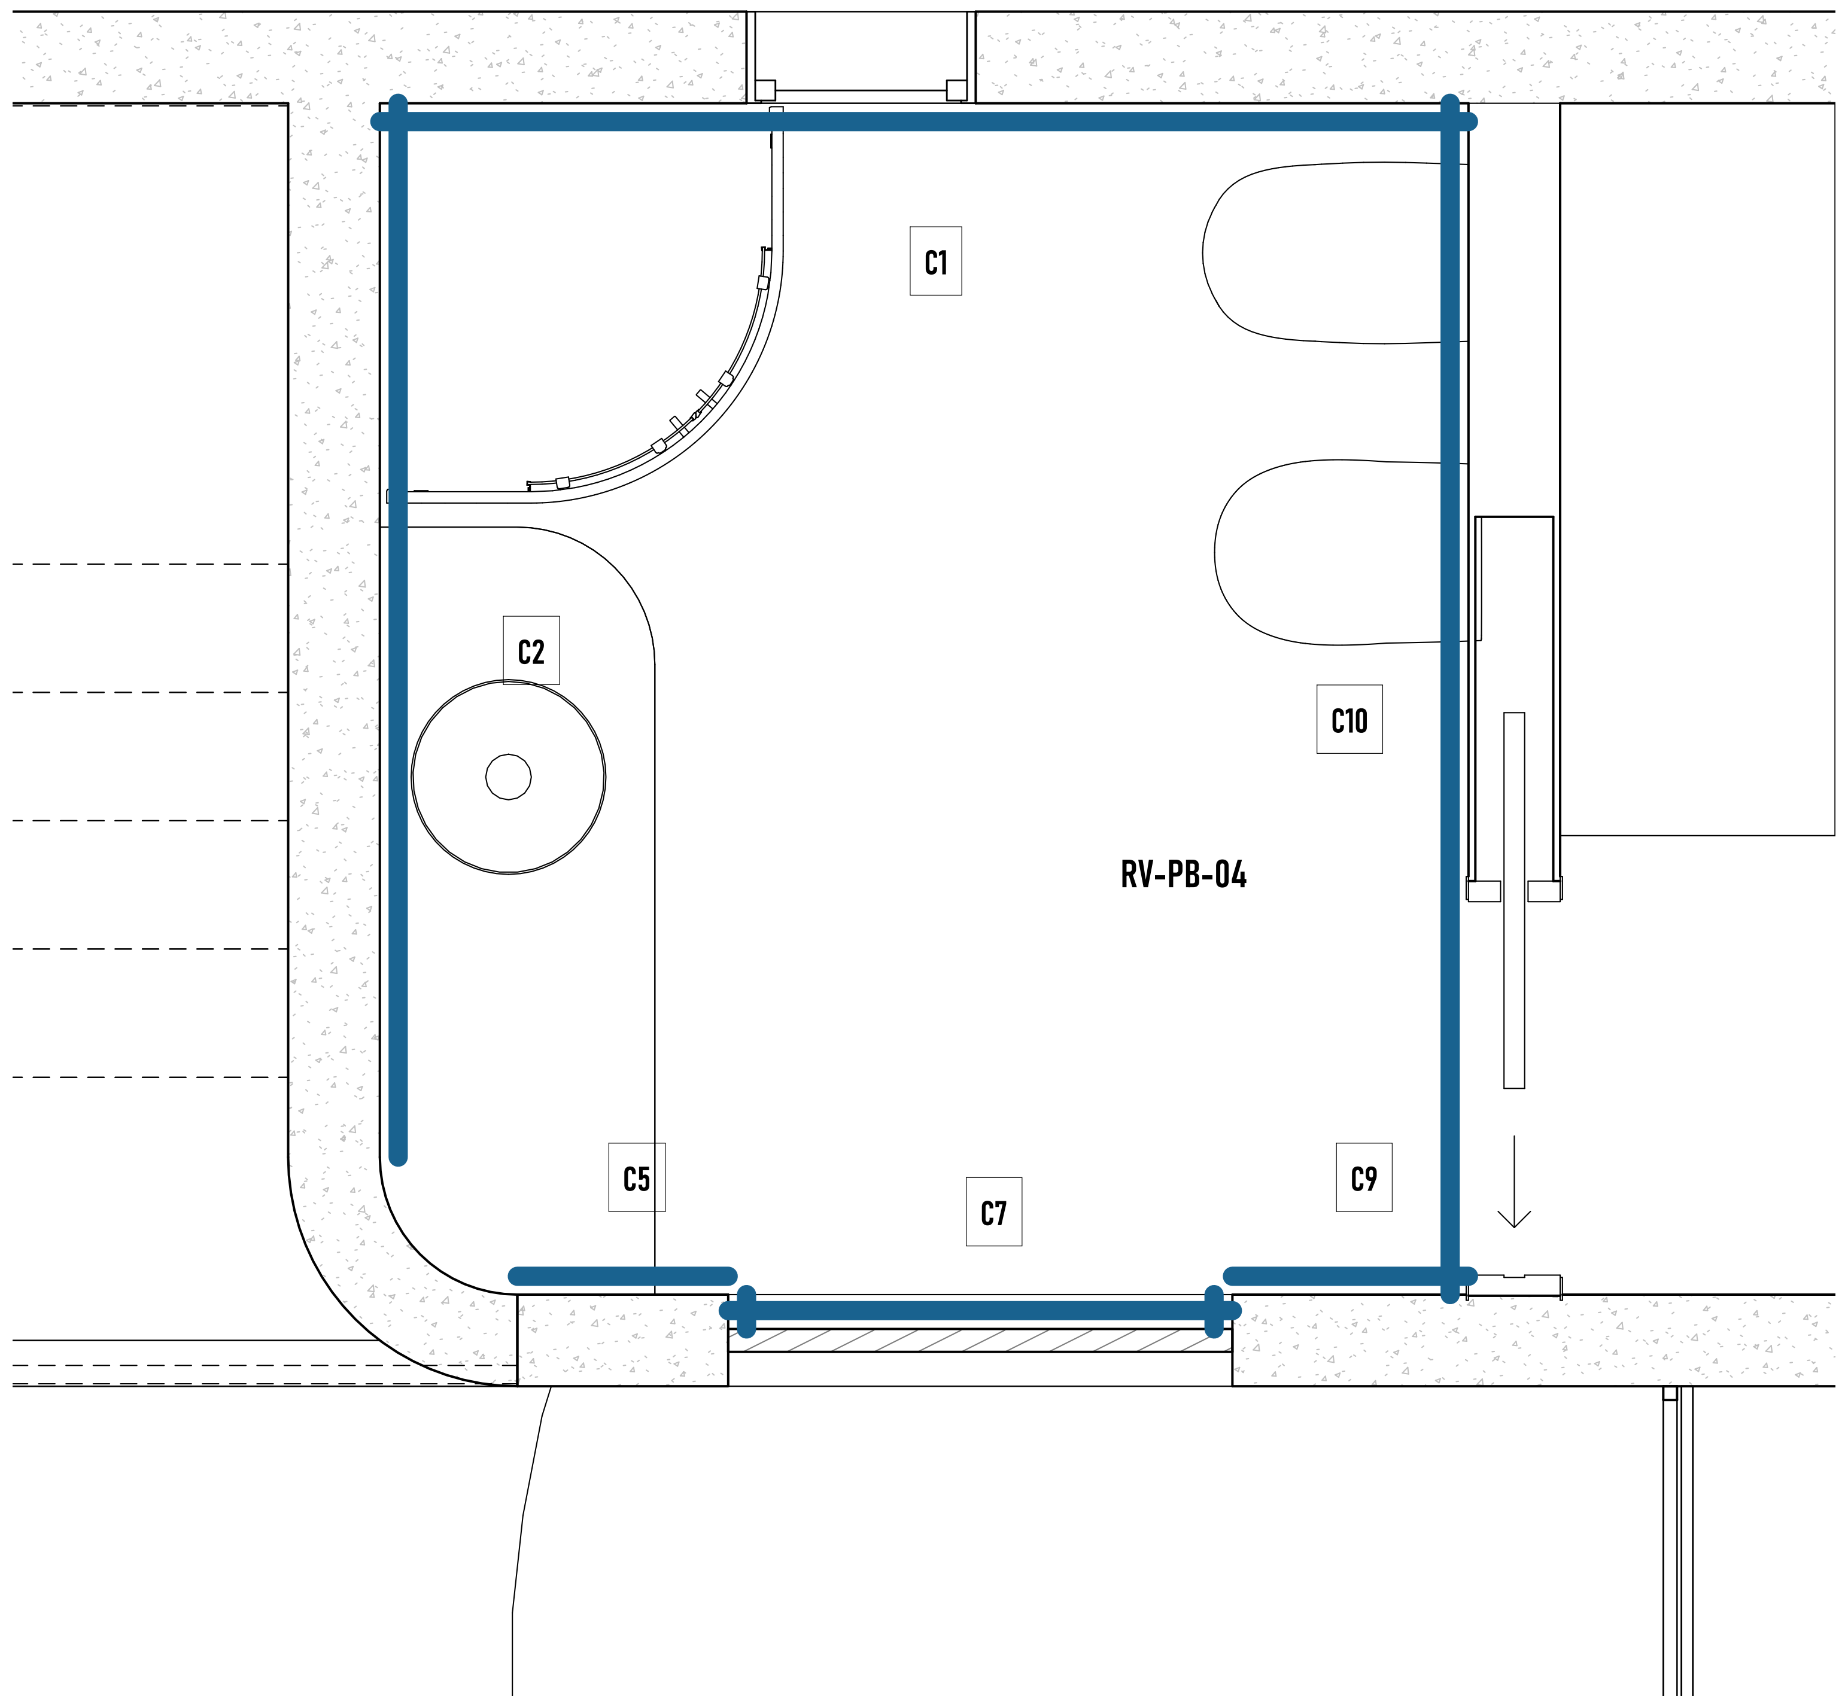

RV-PB-04 · 07 · Toilette Servicio 07 · PB
Revestimiento 0,00–2,40: 15,73 m² netos (vanos 8,20 m²)
Pintura 2,40–2,60: 1,64 m²
Material y formato: a definir (propuesta a confirmar).

RV-PB-04 · cara C1 1:20

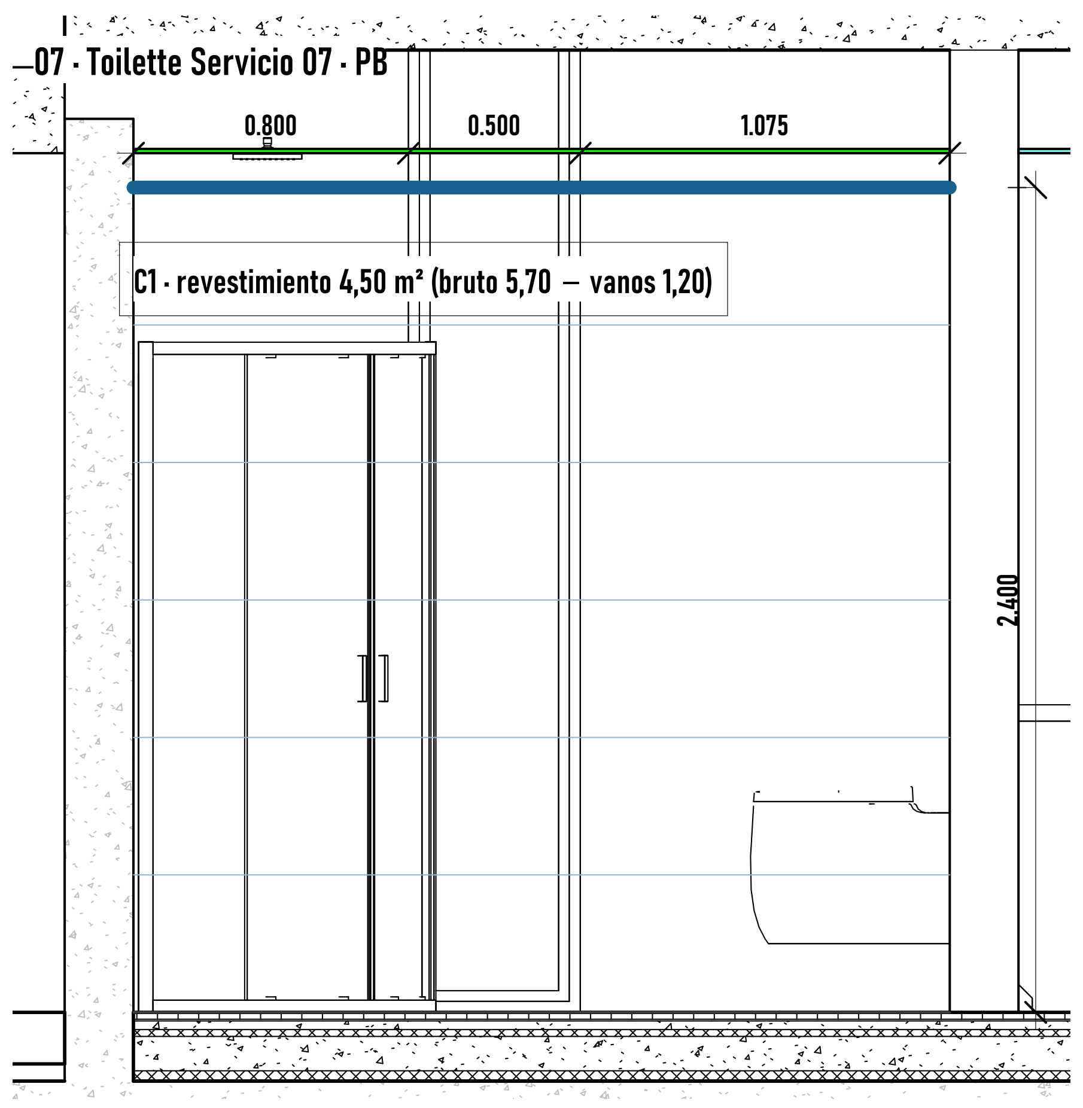
07 · Toilette Servicio 07 · PB
0.800
0.500
1.075
C1 · revestimiento 4,50 m² (bruto 5,70 — vanos 1,20)
2.400

RV-PB-04 · cara C2 1:20

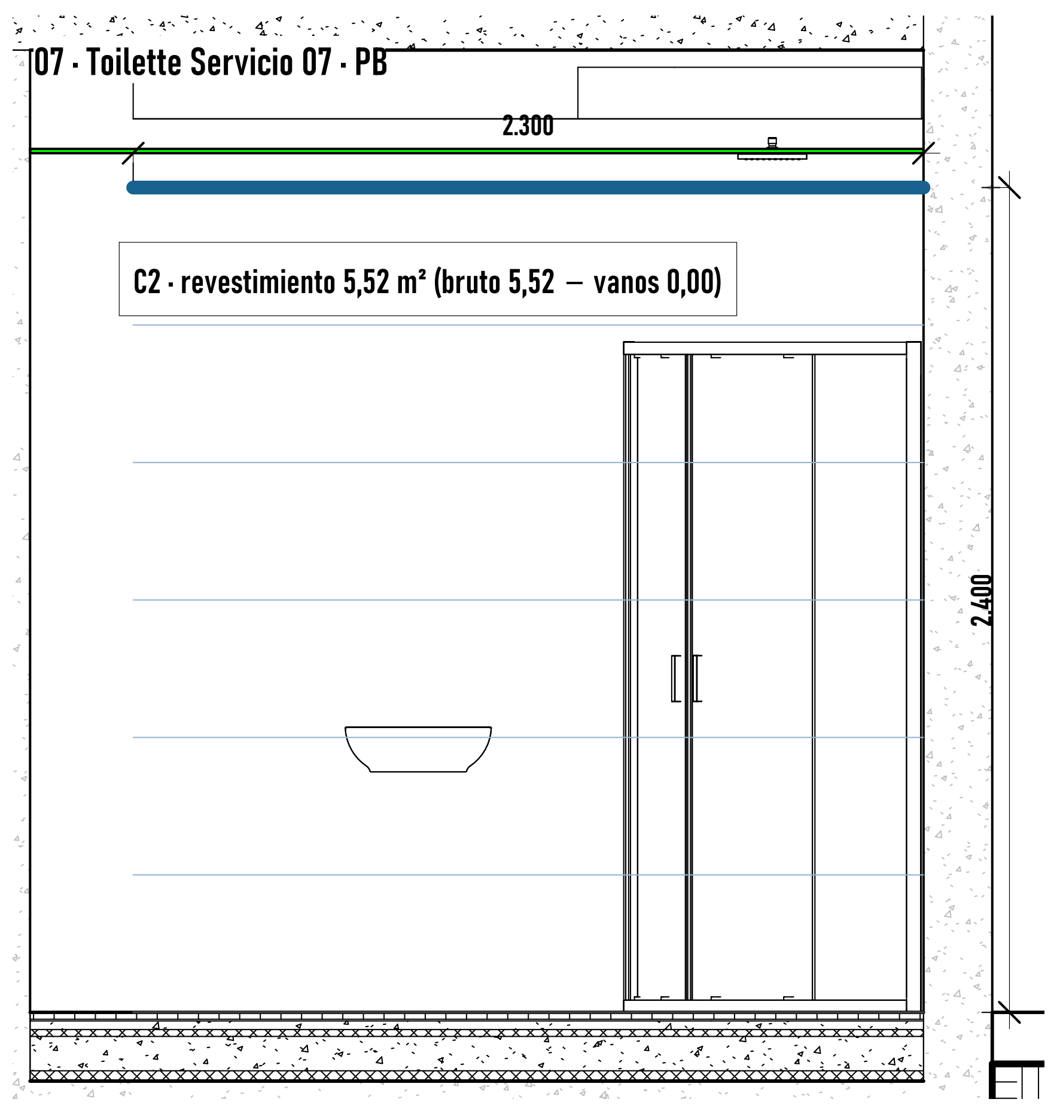
07 · Toilette Servicio 07 · PB
2.300
C2 · revestimiento 5,52 m² (bruto 5,52 — vanos 0,00)
2.400

RV-PB-04 · cara C9 1:25

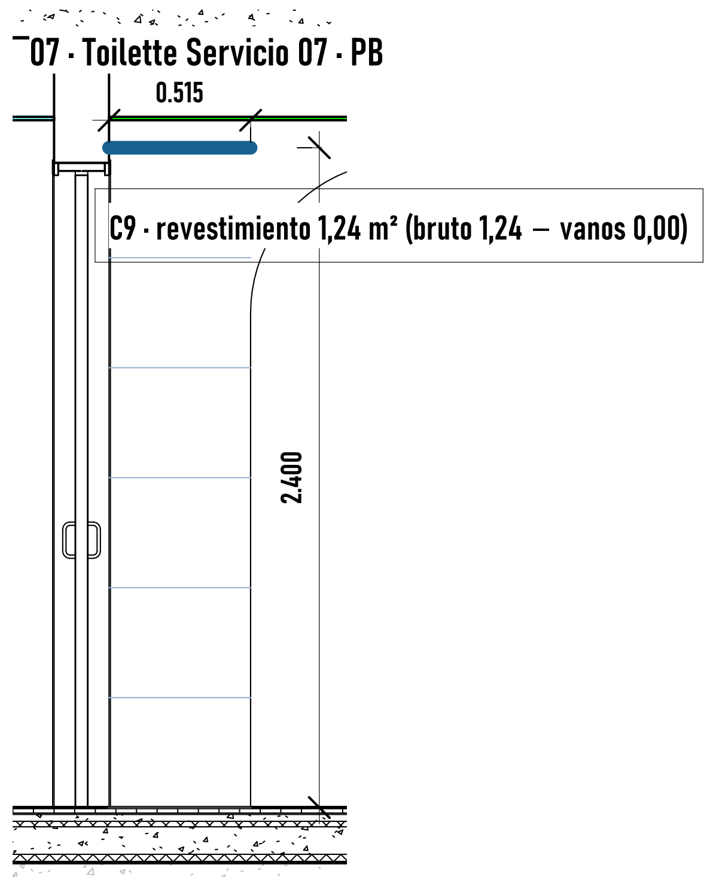
07 · Toilette Servicio 07 · PB
0.515
C9 · revestimiento 1,24 m² (bruto 1,24 — vanos 0,00)
2.400

RV-PB-04 · cara C10 1:25

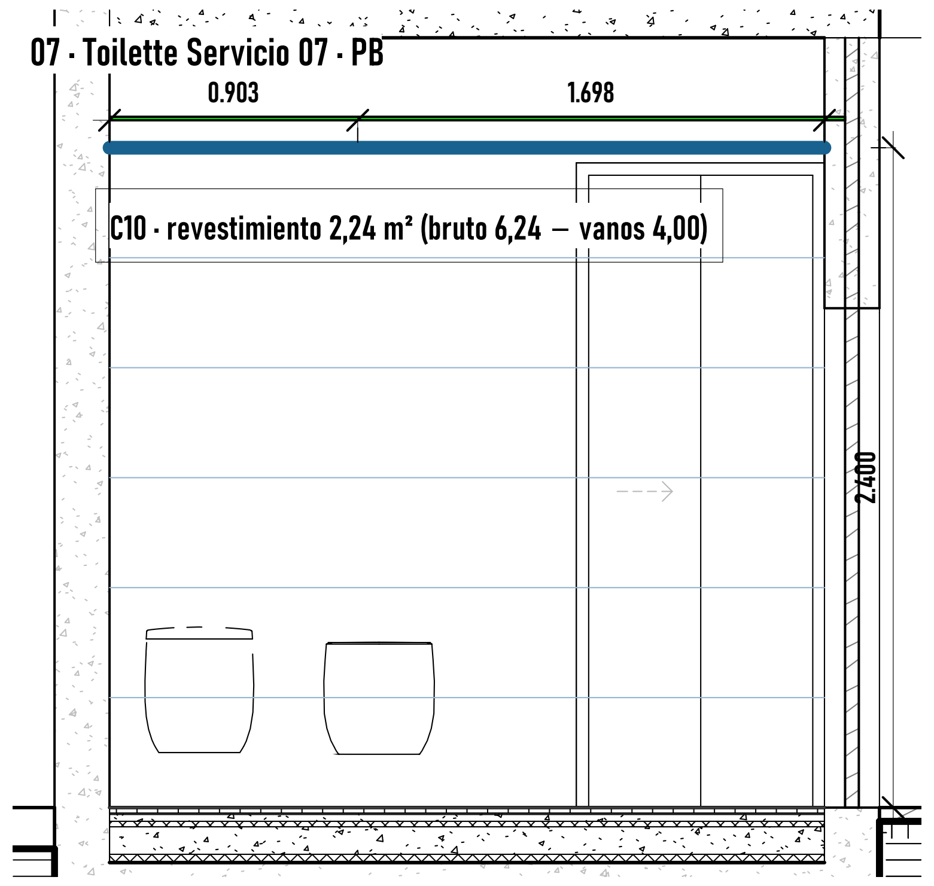
07 · Toilette Servicio 07 · PB
0.903
1.698
C10 · revestimiento 2,24 m² (bruto 6,24 — vanos 4,00)
2.400

PROPUESTA A CONFIRMAR · Revestimientos: baños y toilettes revestidos de 0,00 a 2,40 m; cocina y lavadero franja de 0,60 m sobre mesada (0,90 a 1,50 m); resto de muros pintado hasta 2,60 m; fachada de hormigón visto sin revestimiento. Superficies por cara terminada del local con vanos descontados. Material y formato a definir. El modelo no se modificó.

https://ezeader.myportfolio.com/ezequiel-ader

Consultant
Address
Address
Phone
Fax
e-mail

Consultant
Address
Address
Phone
Fax
e-mail

Consultant
Address
Address
Phone
Fax
e-mail

Consultant
Address
Address
Phone
Fax
e-mail

No.	Description	Date

Angel Luis Brusca

CASA ANGEL

RV-F-PB-04

Project number	0001
Date	18 de Agosto, 2025
Drawn by	Author
Checked by	Checker

Revestimientos · RV-PB-04

Scale	As indicated

10/24/2026 1:17:04 AM