
CASA ÁNGEL · CUBIERTA · ESTRUCTURA DE MADERA

Estructura de madera (vigas VC rotuladas; VP y CR en planilla) 1:60

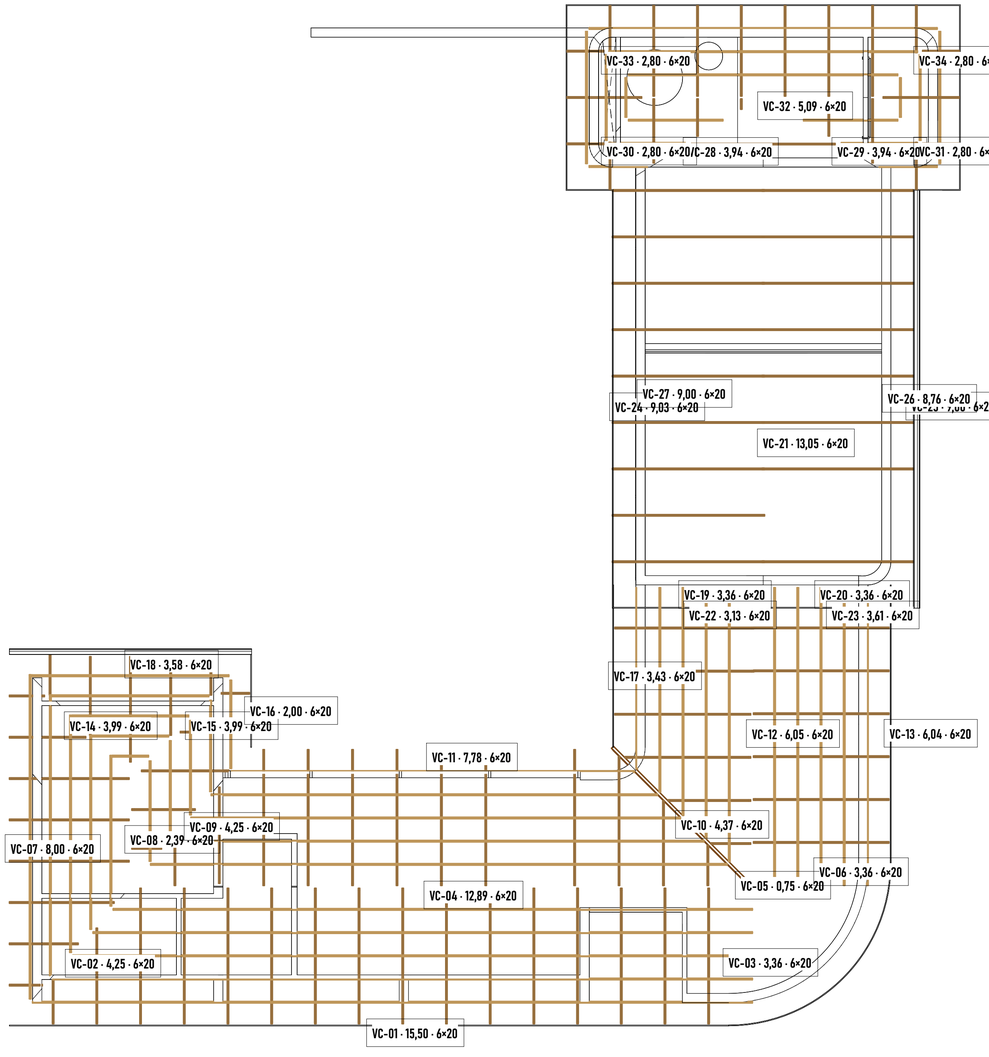

VC 6×20: 34 u, 182,4 ml · VP 3×10: 101 u, 254,8 ml · CR 1,5×5: 60 u, 376,8 ml

Cubierta: geometría nativa; cotas en metros ancladas a extremos (no asociativas). Códigos CU/VC/VP/CR/FA/CA/AL como anotación. Membrana, aislación, cumbreras y bajadas: no modelado / a definir.

https://ezeader.myportfolio.com/ezequiel-ader

Consultant
Address
Address
Phone
Fax
e-mail

Consultant
Address
Address
Phone
Fax
e-mail

Consultant
Address
Address
Phone
Fax
e-mail

Consultant
Address
Address
Phone
Fax
e-mail

No.	Description	Date

Angel Luis Brusca

CASA ANGEL

CUB-02

Project number	0001
Date	18 de Agosto, 2025
Drawn by	Author
Checked by	Checker

Cubierta · 02

Scale 1 : 60

10/23/2026 7:24:00 PM