CASA ÁNGEL · CUBIERTA · FICHA CU-01

CU-01 · 139,1 m² · 26,7° / 30,0°

CU-01 · corte A 1:100

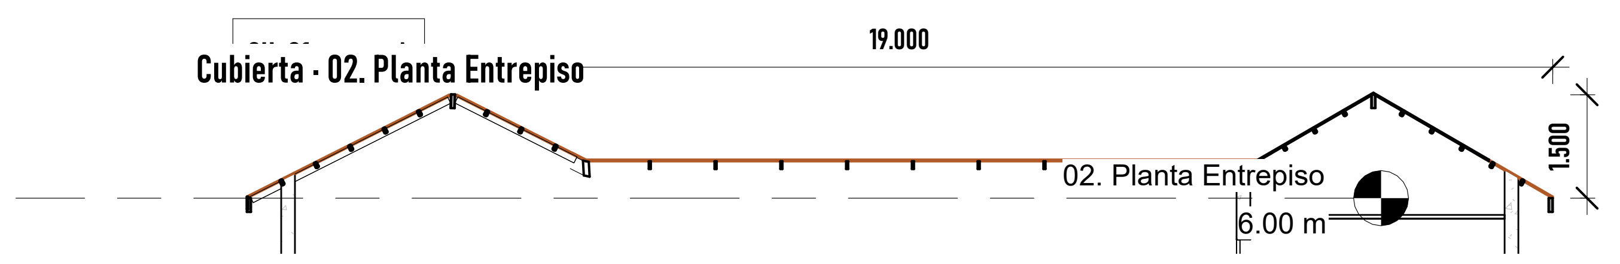

CU-01 · planta 1:60

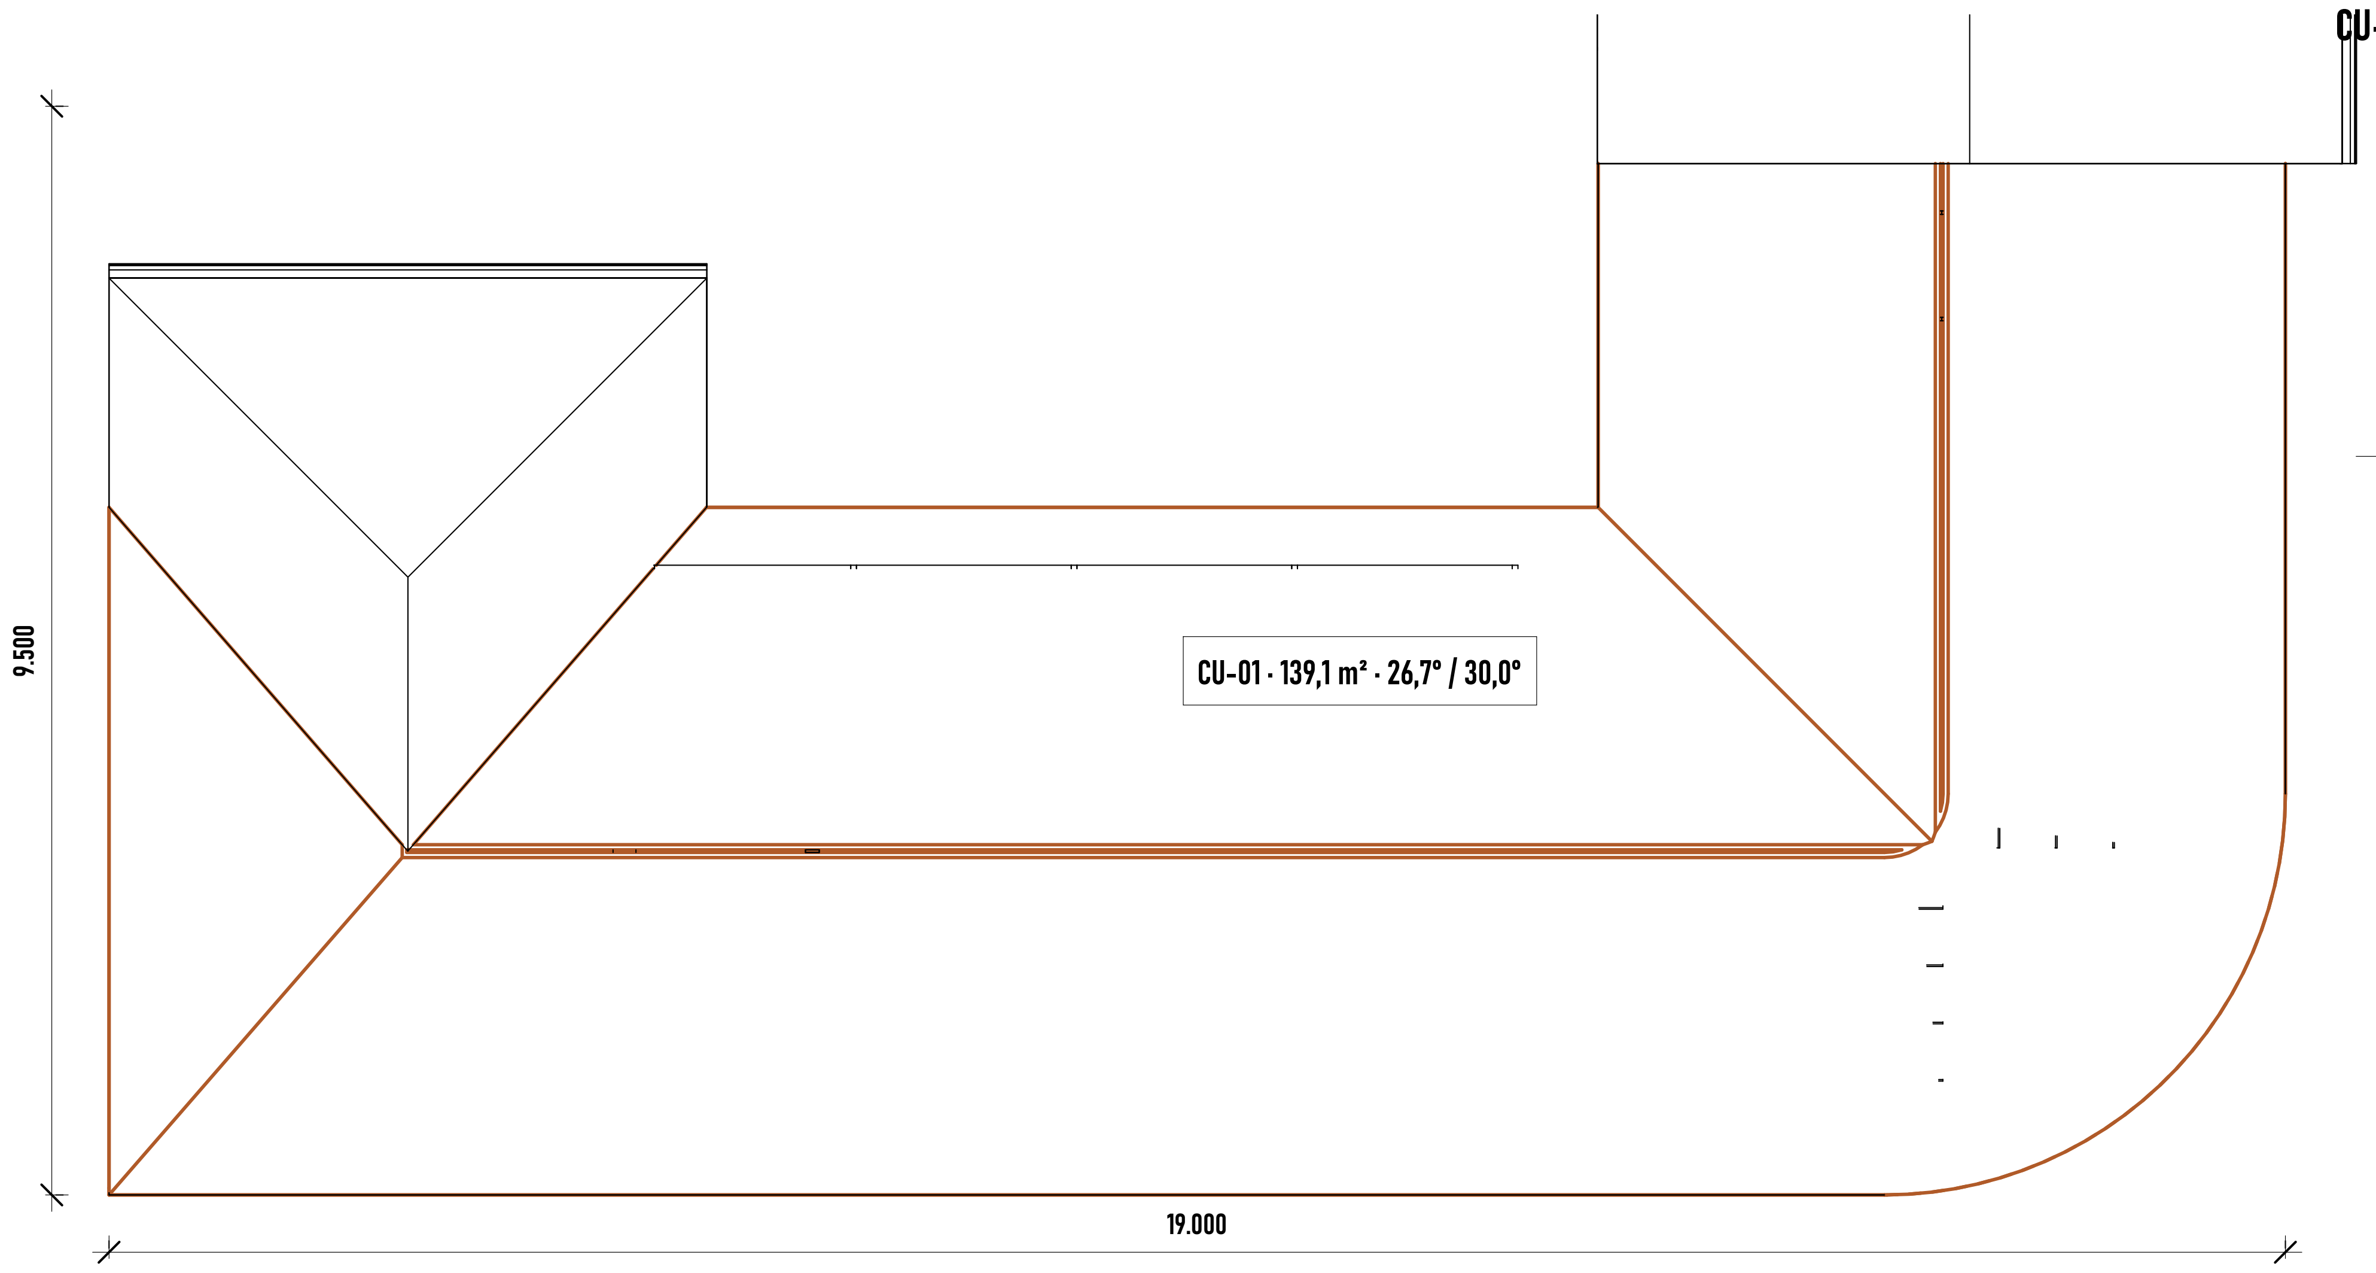

CU-01 · corte B 1:50

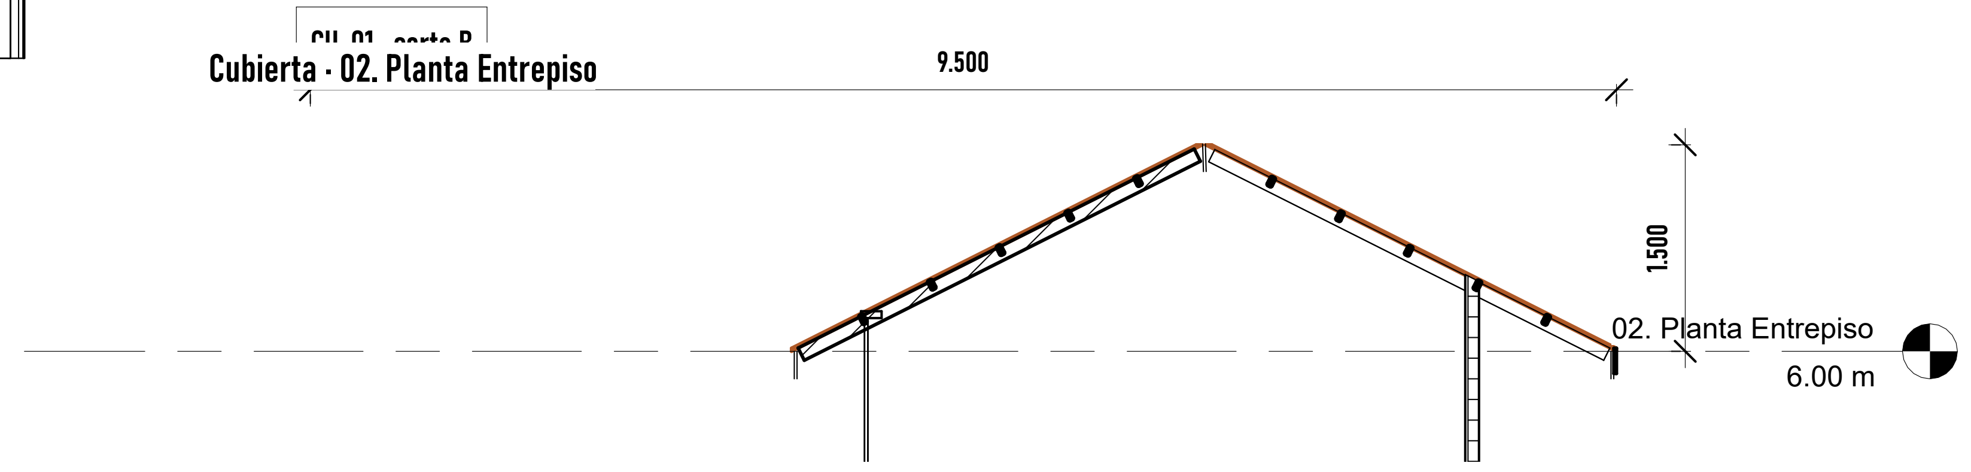

CU-01 · axonométrica 1:100

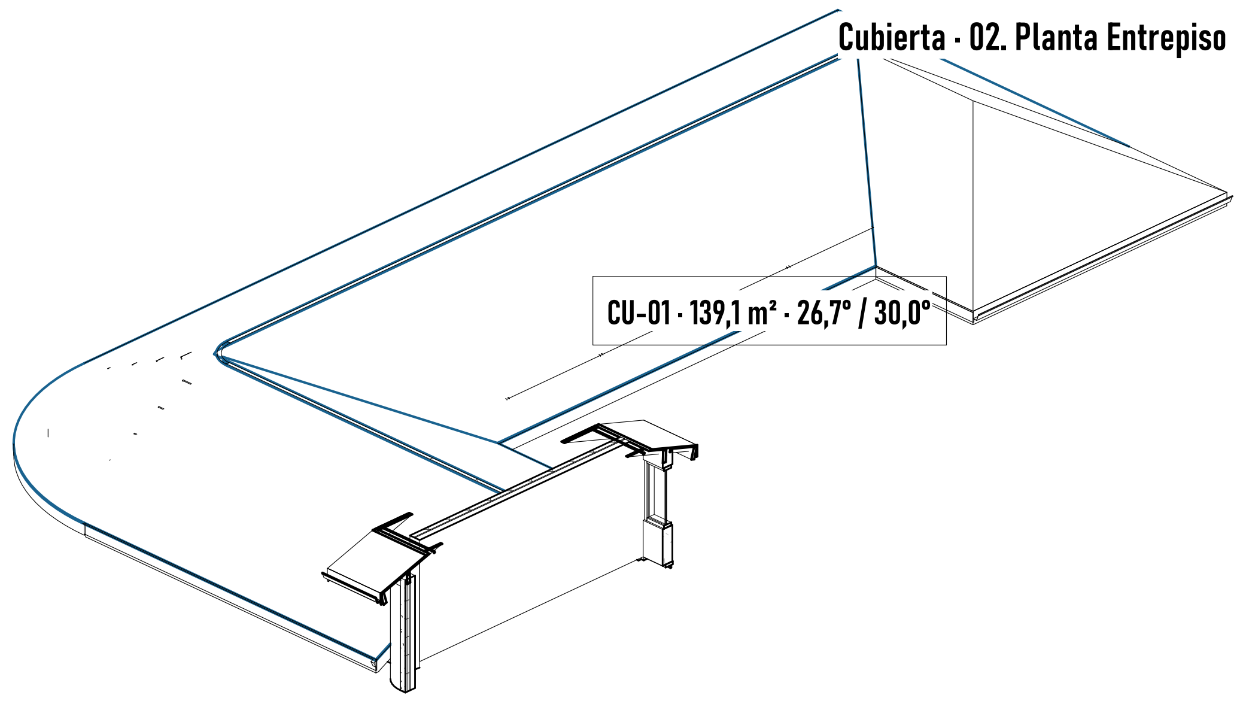
Cubierta · 02. Planta Entrepiso
CU-01 · 139,1 m² · 26,7° / 30,0°

CU-01 · 139,1 m² · 26,7° / 30,0°
Aguas: 46,84 m² a 26,7°; 34,70 m² a 26,7°; 19,76 m² a 26,7°; 16,38 m² a 26,7°; 9,03 m² a 30,0°
Madera bajo este techo: VC 22 u. 109,41 ml · VP 61 u. 165,08 ml · CR 35 u. 233,82 ml
Membrana / aislación: no modeladas (a definir).

Cubierta: geometría nativa; cotas en metros ancladas a extremos (no asociativas). Códigos CU/VC/VP/CR/FA/CA/AL como anotación. Membrana, aislación, cumbreras y bajadas: no modelado / a definir.

https://ezeader.myportfolio.com/ezequiel-ader

Consultant
Address
Address
Phone
Fax
e-mail

Consultant
Address
Address
Phone
Fax
e-mail

Consultant
Address
Address
Phone
Fax
e-mail

Consultant
Address
Address
Phone
Fax
e-mail

No.	Description	Date

Angel Luis Brusca

CASA ANGEL

CUB-F-CU-01

Project number	0001
Date	18 de Agosto, 2025
Drawn by	Author
Checked by	Checker

Cubierta · CU-01

Scale	As indicated

10/23/2026 7:24:04 PM