
CASA ÁNGEL · CUBIERTA · FICHA VC-06

VC-06 · 3,36 · 6×20 · Madera Kerto LVL


VC-06 · planta 1:15

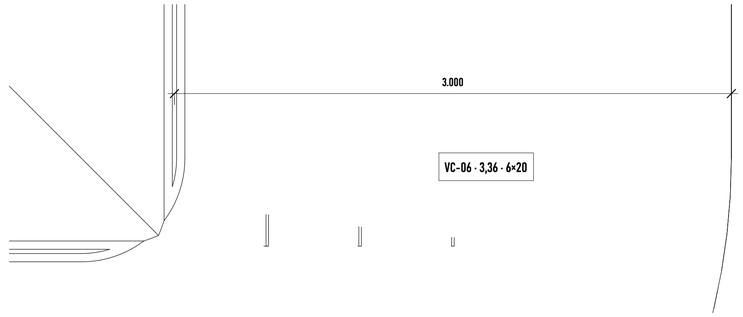


VC-06 · 3,36 · 6×20
Viga Cubierta 200mm x 60mm (Kerto LVL); sin nivel propio, nivel de referencia PE
Largo real 3,36 m · sección 6 × 20 cm · 0,039 m³ madera


VC-06 · axonométrica 1:20

VC-06 · vista 1:20

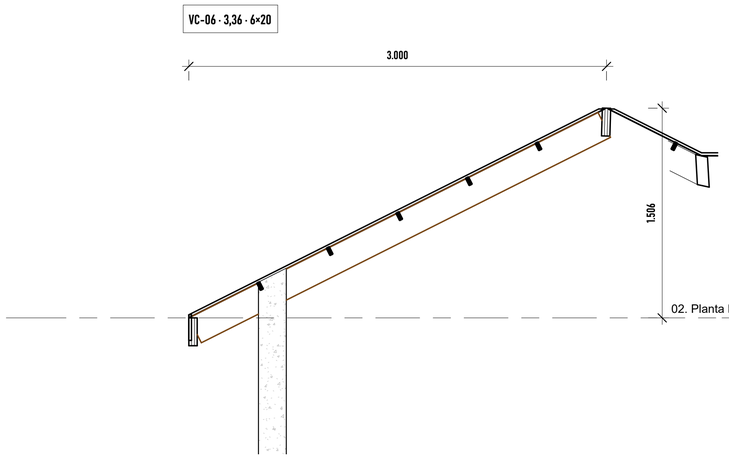

VC-06 · corte 1:20

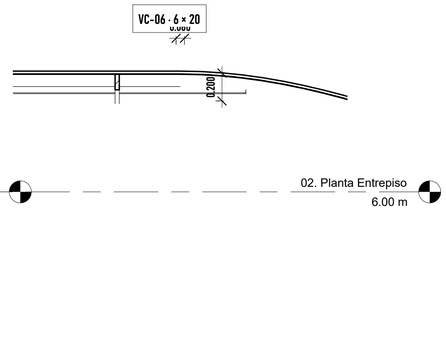

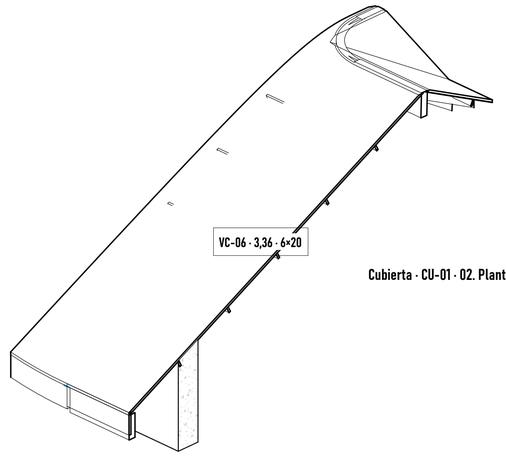

Cubierta · CU-01 · 02. Planta Entrepiso

Cubierta: geometría nativa; cotas en metros ancladas a extremos (no asociativas). Códigos CU/VC/VP/CR/FA/CA/AL como anotación. Membrana, aislación, cumbreras y bajadas: no modelado / a definir.

https://ezeader.myportfolio.com/ezequiel-ader

Consultant
Address
Address
Phone
Fax
e-mail

Consultant
Address
Address
Phone
Fax
e-mail

Consultant
Address
Address
Phone
Fax
e-mail

Consultant
Address
Address
Phone
Fax
e-mail

No.	Description	Date

Angel Luis Brusca

CASA ANGEL

CUB-F-VC-06

Project number	0001
Date	18 de Agosto, 2025
Drawn by	Author
Checked by	Checker

Cubierta · VC-06

Scale: As indicated

10/23/2026 7:24:24 PM