CASA ÁNGEL · CUBIERTA · FICHA VC-20


VC-20 · 3,36 · 6×20 · Madera Kerto LVL

VC-20 · planta 1:10




VC-20 · 3,36 · 6×20
Viga Cubierta 200mm x 60mm (Kerto LVL); sin nivel propio, nivel de referencia PE
Largo real 3,36 m · sección 6 × 20 cm · 0,040 m³ madera


VC-20 · vista 1:25

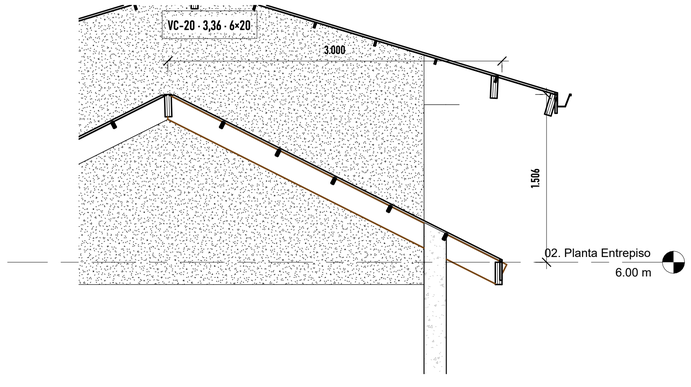

VC-20 · corte 1:25

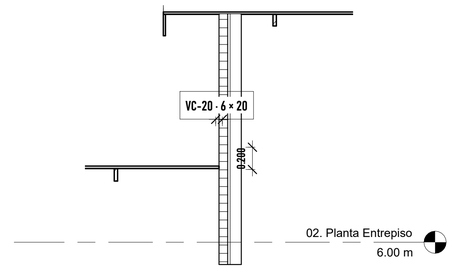

VC-20 · axonométrica 1:25

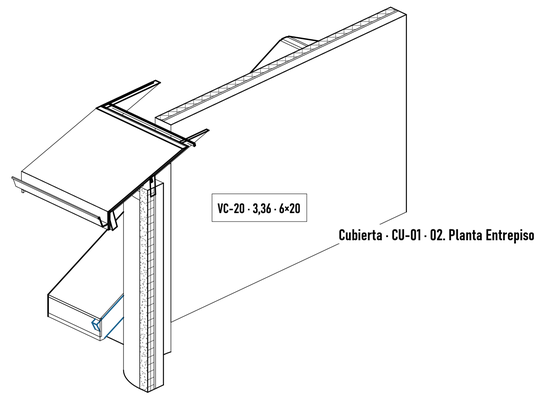

Cubierta: geometría nativa; cotas en metros ancladas a extremos (no asociativas). Códigos CU/VC/VP/CR/FA/CA/AL como anotación. Membrana, aislación, cumbreras y bajadas: no modelado / a definir.

https://ezeader.myportfolio.com/ezequiel-ader

Consultant
Address
Address
Phone
Fax
e-mail

Consultant
Address
Address
Phone
Fax
e-mail

Consultant
Address
Address
Phone
Fax
e-mail

Consultant
Address
Address
Phone
Fax
e-mail

No.	Description	Date

Angel Luis Brusca

CASA ANGEL

CUB-F-VC-20

Project number	0001
Date	18 de Agosto, 2025
Drawn by	Author
Checked by	Checker

Cubierta · VC-20

Scale: As indicated

10/23/2026 7:24:41 PM